


DRENÁŽNÍ ŠACHTA KONTROLNÍ - BETONOVÁ  
NA POTRUBÍ DN 150


M 1:20

ŘEZ A - A

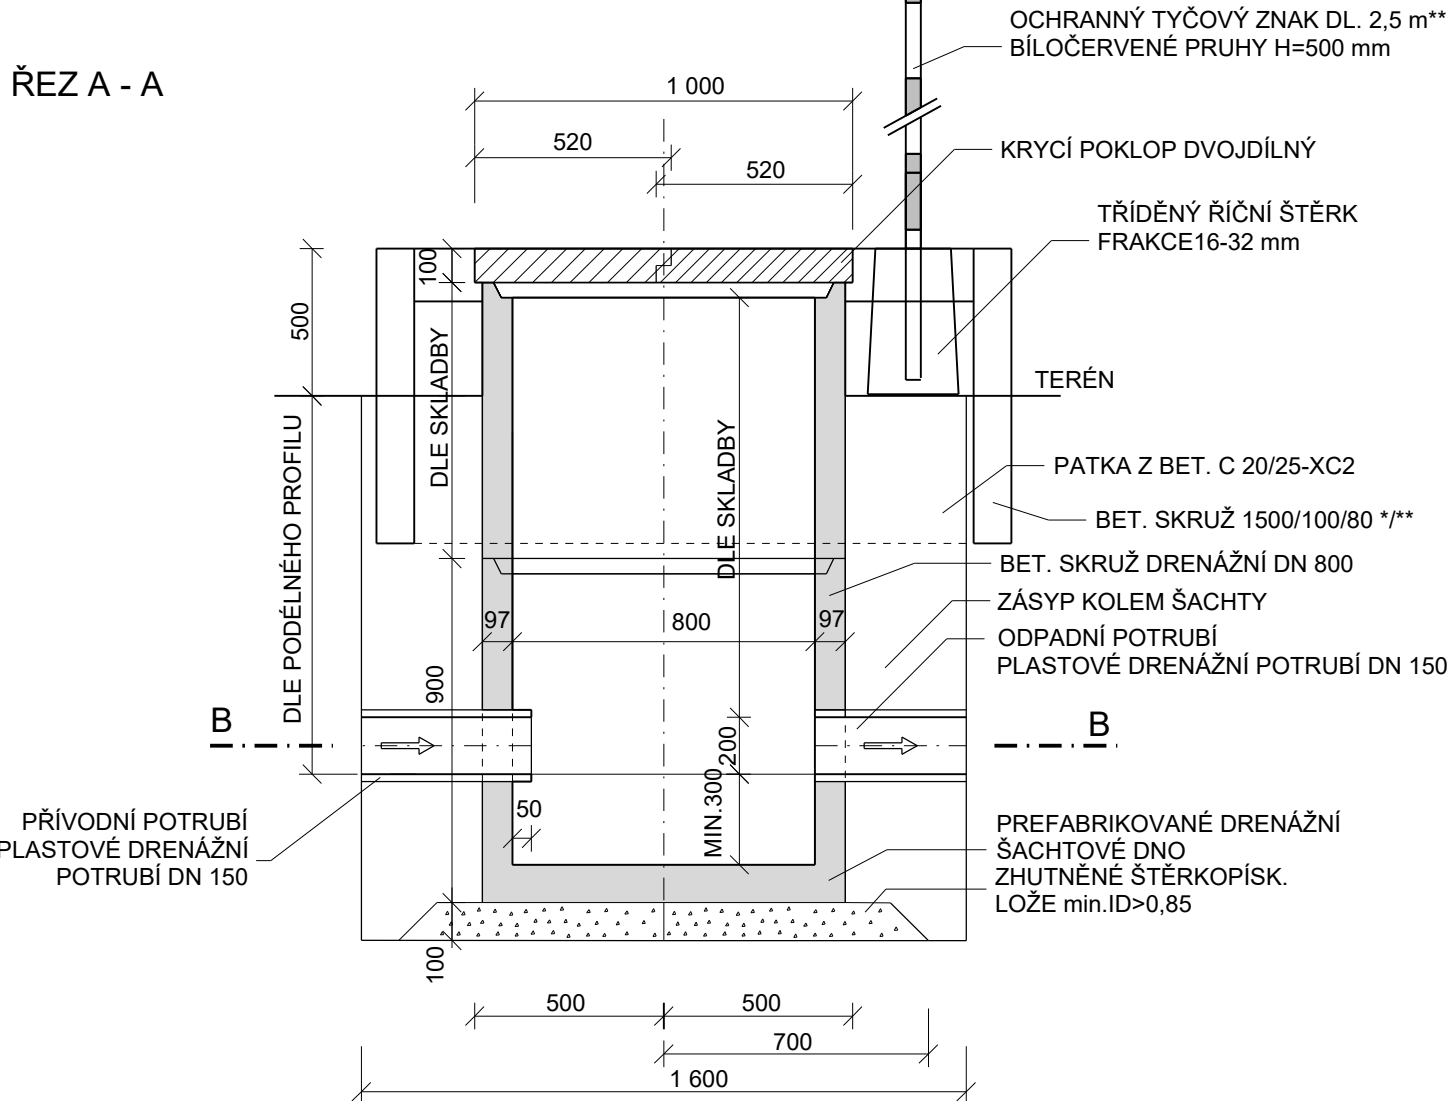

\* - SKRUŽ DN 1500 SE POUŽÍJE V PŘÍPADĚ  
TRASOVÁNÍ MIMO TĚLESO SILNICE / DÁLNICE  
\*\* POUŽÍJE SE I U VSTUPNÍCH ŠACHT NA PODCHODECH

ŘEZ B - B

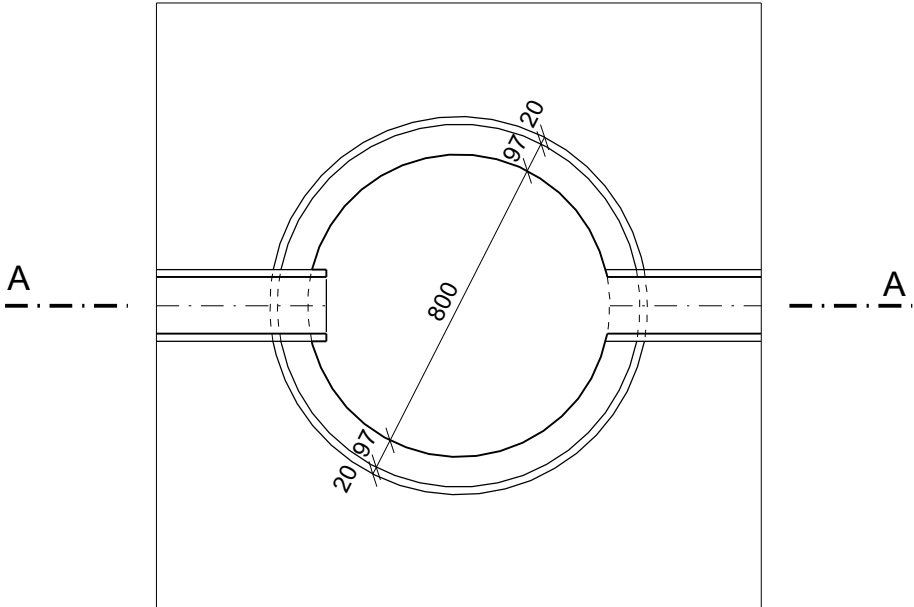


VSTUPNÍ ŠACHTA NA POTRUBÍ DN 200 A DN 250  
NA PODCHODECH KOMUNIKACÍ


M 1:50

ZÁKLADNÍ SESTAVA


ŘEZ A-A'

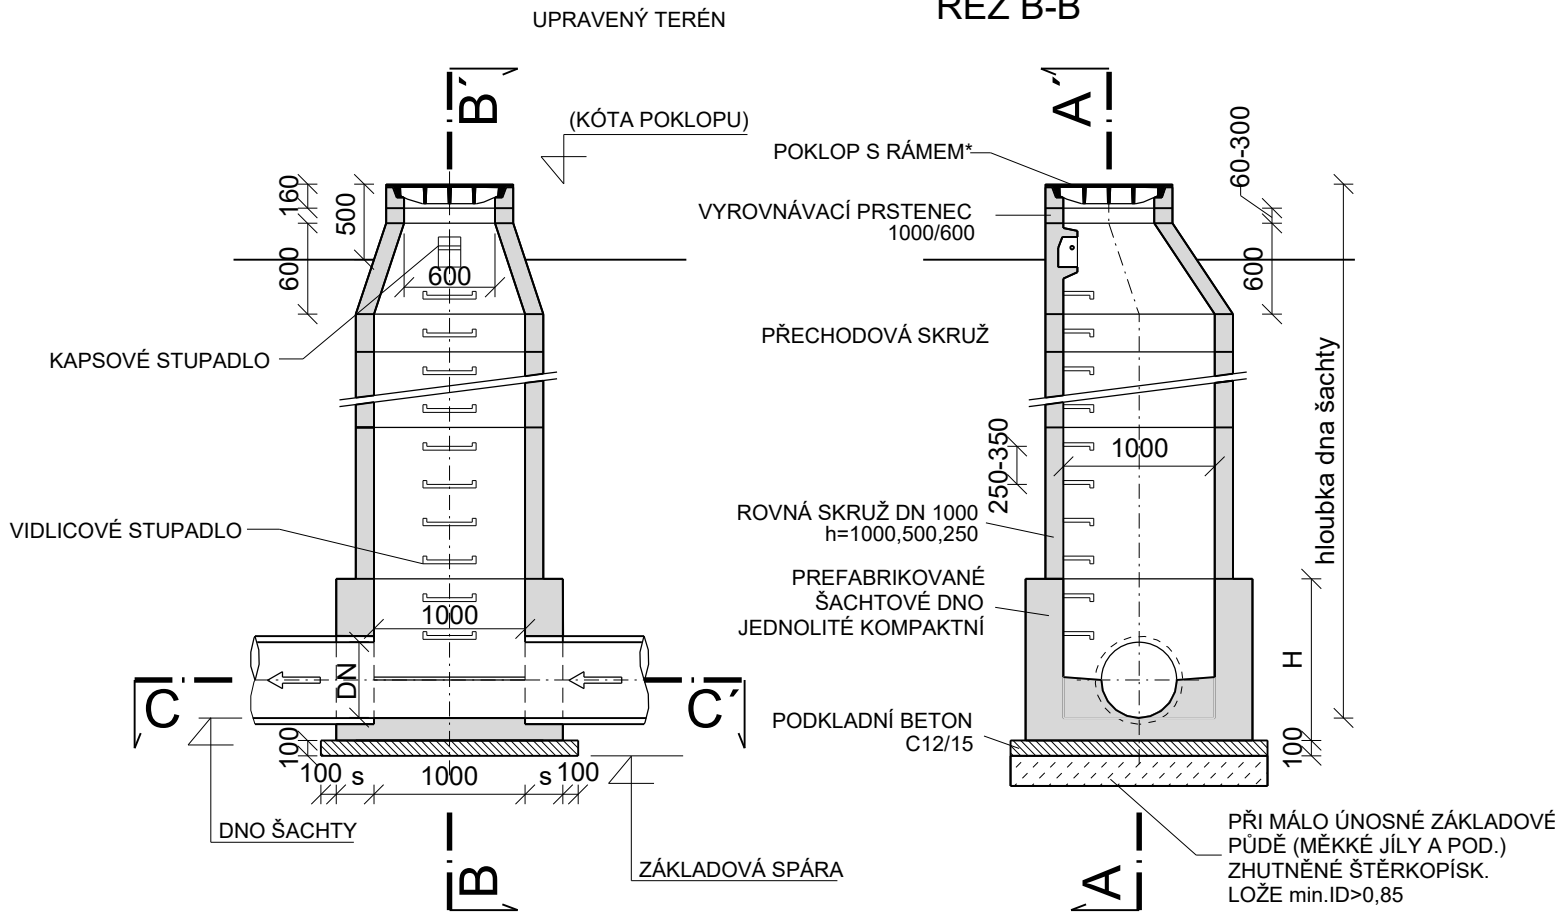

ŘEZ B-B'

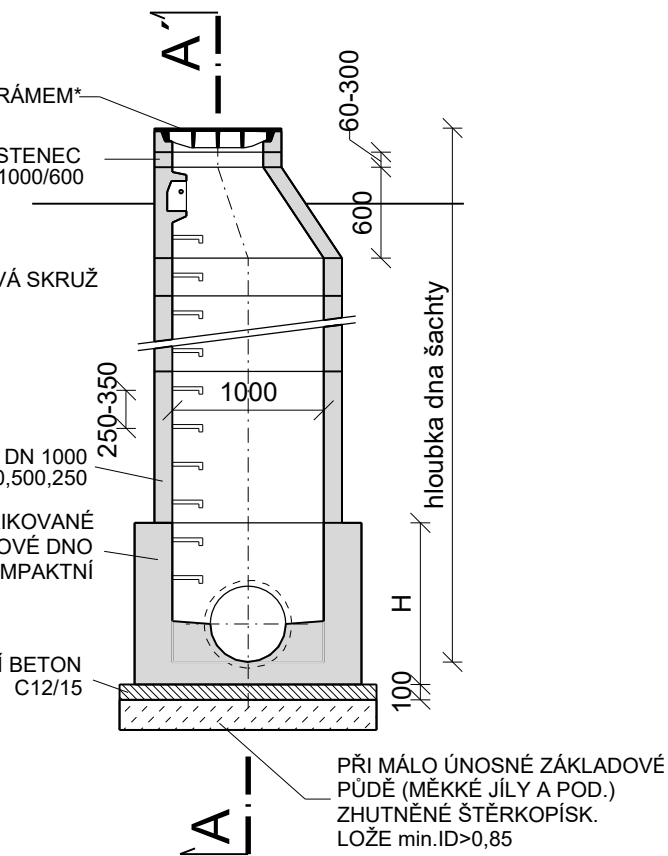

ŘEZ C-C'

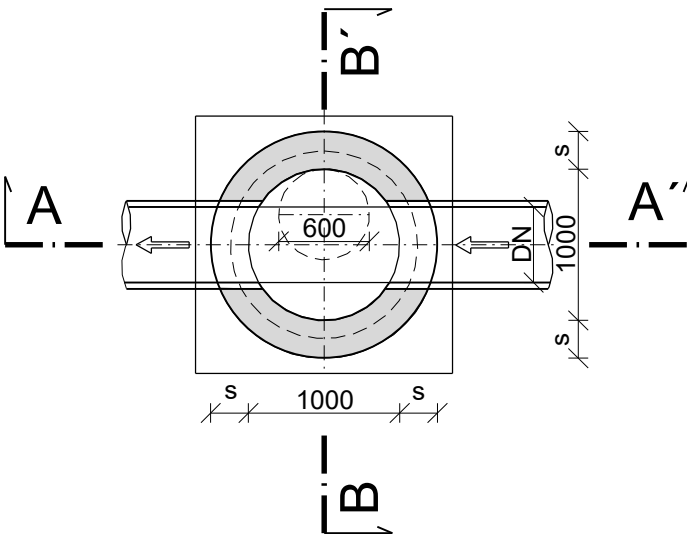

NA STOKÁCH DN 200 - PLAST

| DN      | š    | H   | s   |
|---------|------|-----|-----|
| 200/250 | 1000 | 950 | 190 |

Souřadnicový systém: S-JTSK  
Výškový systém: Bpv

SO 380 Úpravy meliorací

Objednatel:



ŘEDITELSTVÍ  
SILNIC  
A DÁLNIC

Ředitelství silnic a dálnic s. p.

Čerčanská 2023/12, Krč, 140 00 Praha 4

Zhotovitel:



Valbek, spol. s r.o.

Vaňurova 505/17  
460 07 Liberec 3



Vypracoval  
Zodp. projektant  
Tech. kontrola

ING. J. VANCL  
ING. J. VANCL  
ING. D. LANDA

Zak. číslo  
Datum  
Stupeň

21-LI13-001  
02/2025  
PDPS

I/16 MLADÁ BOLESLAV - MARTINOVICE

Akce

Počet formátů

Měřítko

Č. přílohy

3 x A4  
1 : 50 (20)  
Paré

6

Zhotovitel:  
Valbek, spol. s r.o.  
Vaňurova 505/17  
460 07 Liberec 3

Příloha

DRENÁŽNÍ ŠACHTY