


VZOROVÝ ŘEZ JÍMACÍM OBJEKTEM

M 1:50

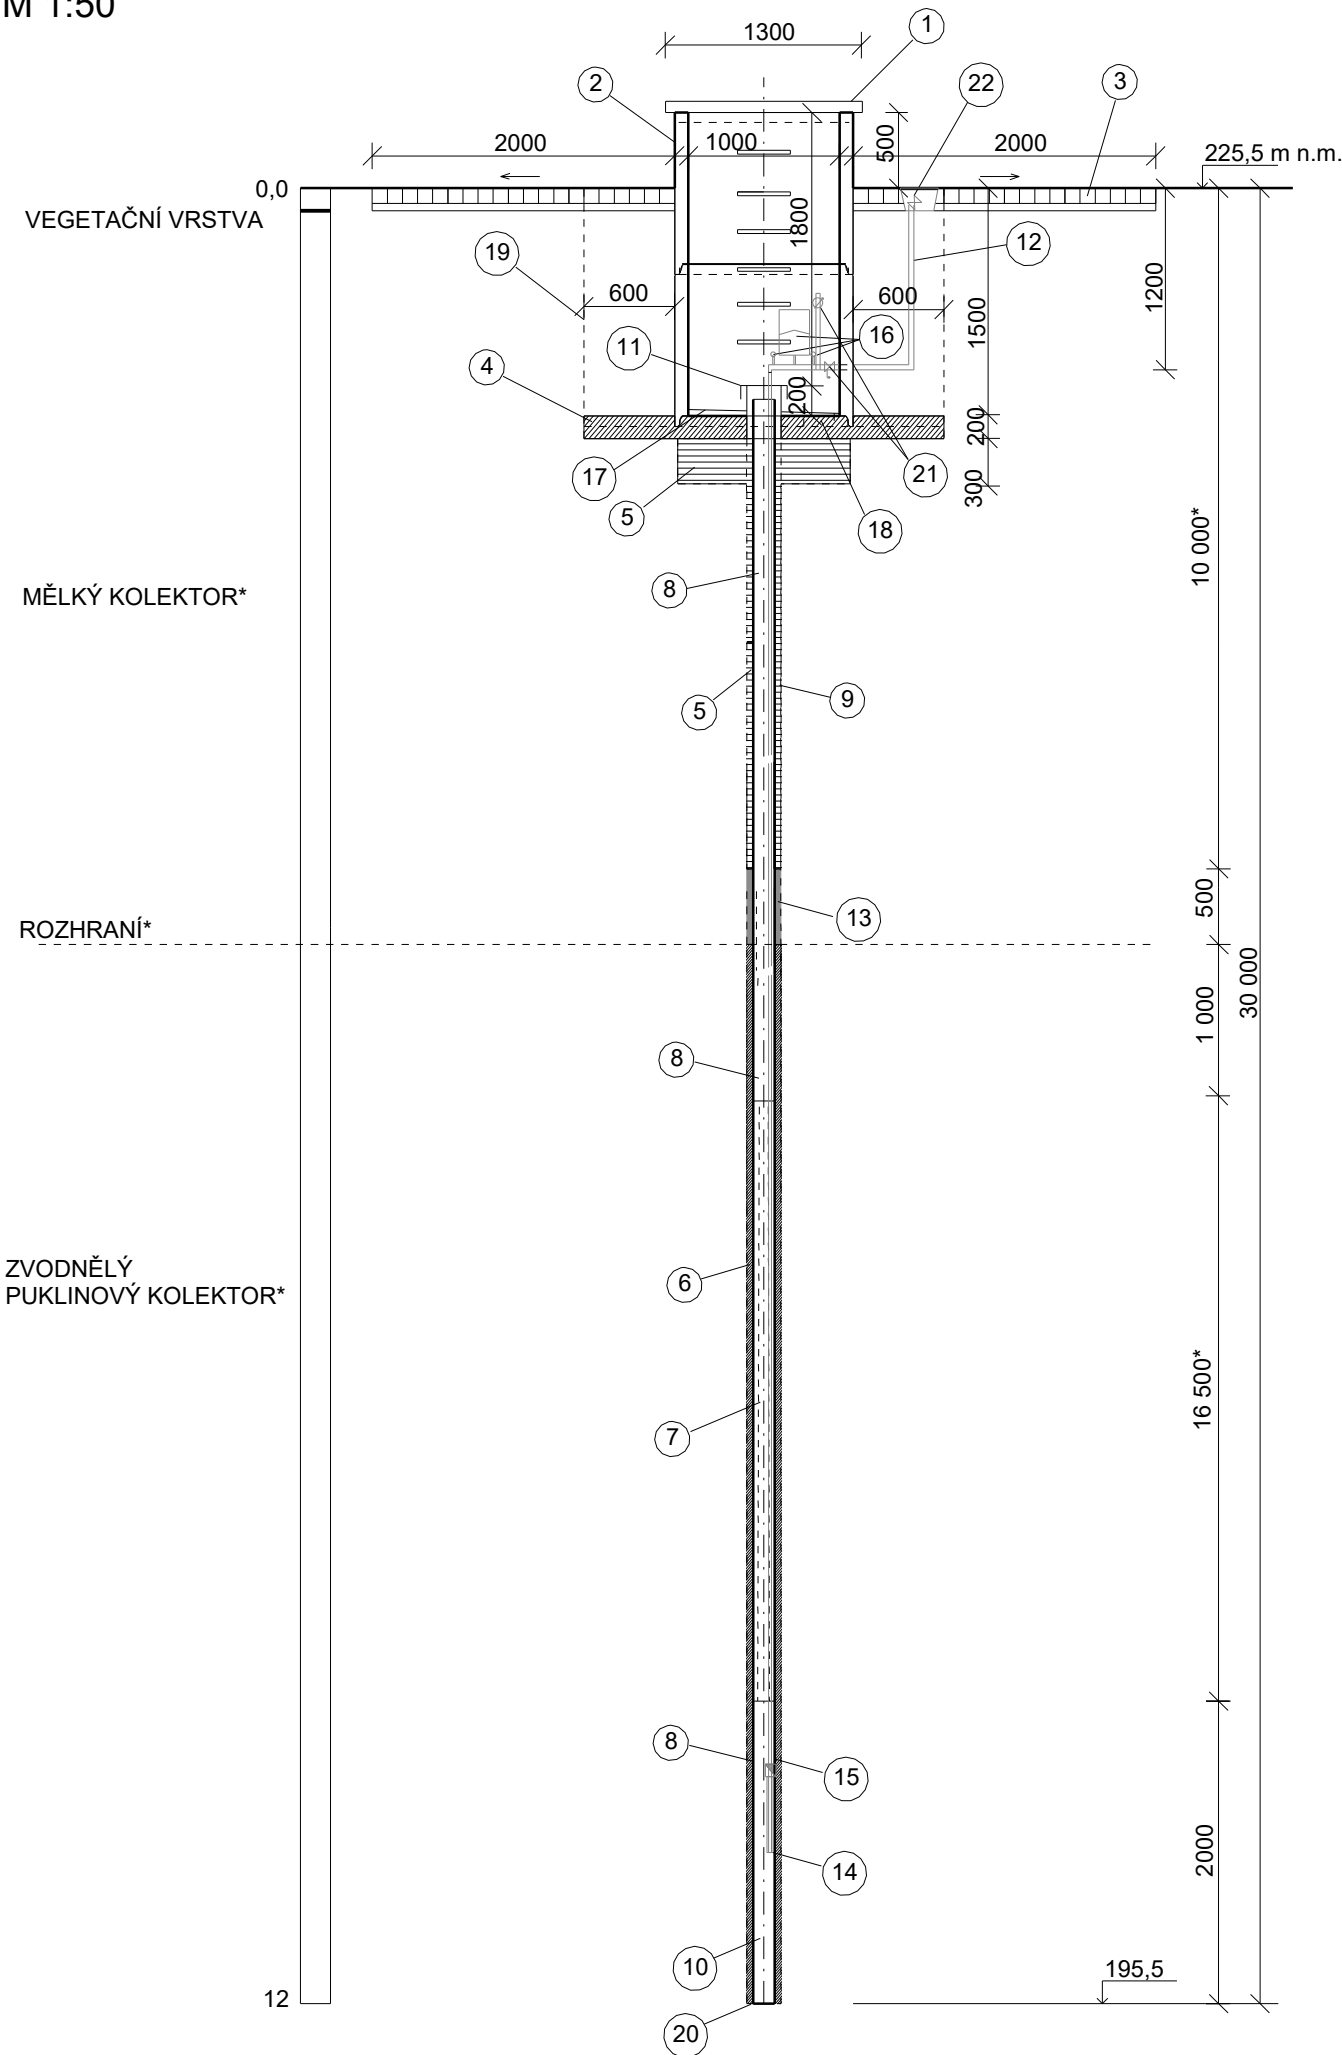

LEGENDA:

- 1

KRYCÍ DESKA - TBN-Q 1300/75 **
- 2

ŠACHTOVÁ SKRUŽ - TBS - Q1000/1000(500/250)/120-SP **
- 3

ZÁMKOVÁ DLAŽBA ŠEDÁ TL. 80 mm DO LOŽE z MC TL. 100mm
- 4

BETONOVÁ DESKA TL. 200 mm C25/30 XF2
- 5

KARI SÍŤ 8/150x150 B St 500 B PŘI DOLNÍM POVRCHU
- 6

TĚSNĚNÍ JÍLOCEMENTEM (BENTONITEM TSB)
- 7

OBSYP FRAKCE 4-8 mm
- 8

ZÁRUBNICE PERFOROVANÁ PLASTOVÁ (PERF. tl. 1,5 mm)
- 9

ZÁRUBNICE PLNÁ PLASTOVÁ MIN. PRŮMĚR 160 mm
- 10

VRT MIN. PRŮMĚR 225 mm; V NESOUDRŽNÝCH ZEMINÁCH
- 11

OCEL. PAŽENÍ PRŮM. min. 305 mm DL. MIN. 8,5m*
- 12

KALNÍK
- 13

KRYT ZHLAVÍ VČETNĚ UCHYCENÍ LANA ČERPADLA
- 14

VÝTLAK HDPE SDR17 PE100 OD/DN 40/32 d40x2,4 mm
- 15

VČETNĚ PŘÍPOJKY NN A SIGNALIZAČNÍCH KABELŮ
- 16

FILTRAČNÍ VRSTVA ŠTĚRKOPÍSKU FRAKCE 0-4 mm
- 17

ČERPADLO PONORNÉ DO VRTU SE ZPĚTNOU KLAPKOU
- 18

SONDY PRO ZAJIŠTĚNÍ OCHRANY PROTI CHODU NA SUCHO
- 19

MANOMETR, TLAKOVÁ NÁDOBA MIN. 8 l, TLAKOVÝ SPÍNAČ,
- 20

SPÁDOVÝ BETON C16/20nXF1
- 21

ČERPACÍ JÍMKA S VTOKOVOU MŘÍŽKOU
- 22

PAŽENÝ VÝKOP
- 23

PLNÉ DNO
- 24

UZAVÍRACÍ VENTIL DN25 - 1'' S VYPOUŠTĚCÍM VENTILEM + VODOMĚR 3/4'' + REDUKCE
- 25

VENTILOVÁ ŠACHTA PLAST - VENTIL 3/4'' + REDUKCE

* BUDE UPŘESNĚNO BĚHEM VRTNÝCH PRACÍ ZA DOZORU HYDROGEOLOGA

** V PŘÍPADĚ ZIMNÍHO PROVOZU S DODATEČNÝM ZATEPLENÍM

Souřadnicový systém: S-JTSK
Výškový systém: Bpv

SO 390.1 Zřízení náhradních vodních zdrojů - p.č. 188/5

Objednatel:



**ŘEDITELSTVÍ
SILNIC
A DÁLNIC**

Ředitelství silnic a dálnic s. p.
Čerčanská 2023/12, Krč, 140 00 Praha 4

Zhotovitel:



Valbek

Valbek, spol. s r.o.
Vaňurova 505/17
460 07 Liberec 3

	Vypracoval	ING. J. VANCL		Zak. číslo	21-LI13-001
	Zodp. projektant	ING. J. VANCL		Datum	02/2025
	Tech. kontrola	ING. D. LANDA		Stupeň	PDPS
	Akce I/16 MLADÁ BOLESLAV - MARTINOVICE			Počet formátů	2 x A4
				Měřítko	1 : 50
Zhotovitel: Valbek, spol. s r.o. Vaňurova 505/17 460 07 Liberec 3	Příloha VZOROVÝ ŘEZ JÍMACÍM OBJEKTEM			Č. přílohy	Paré
				3	