


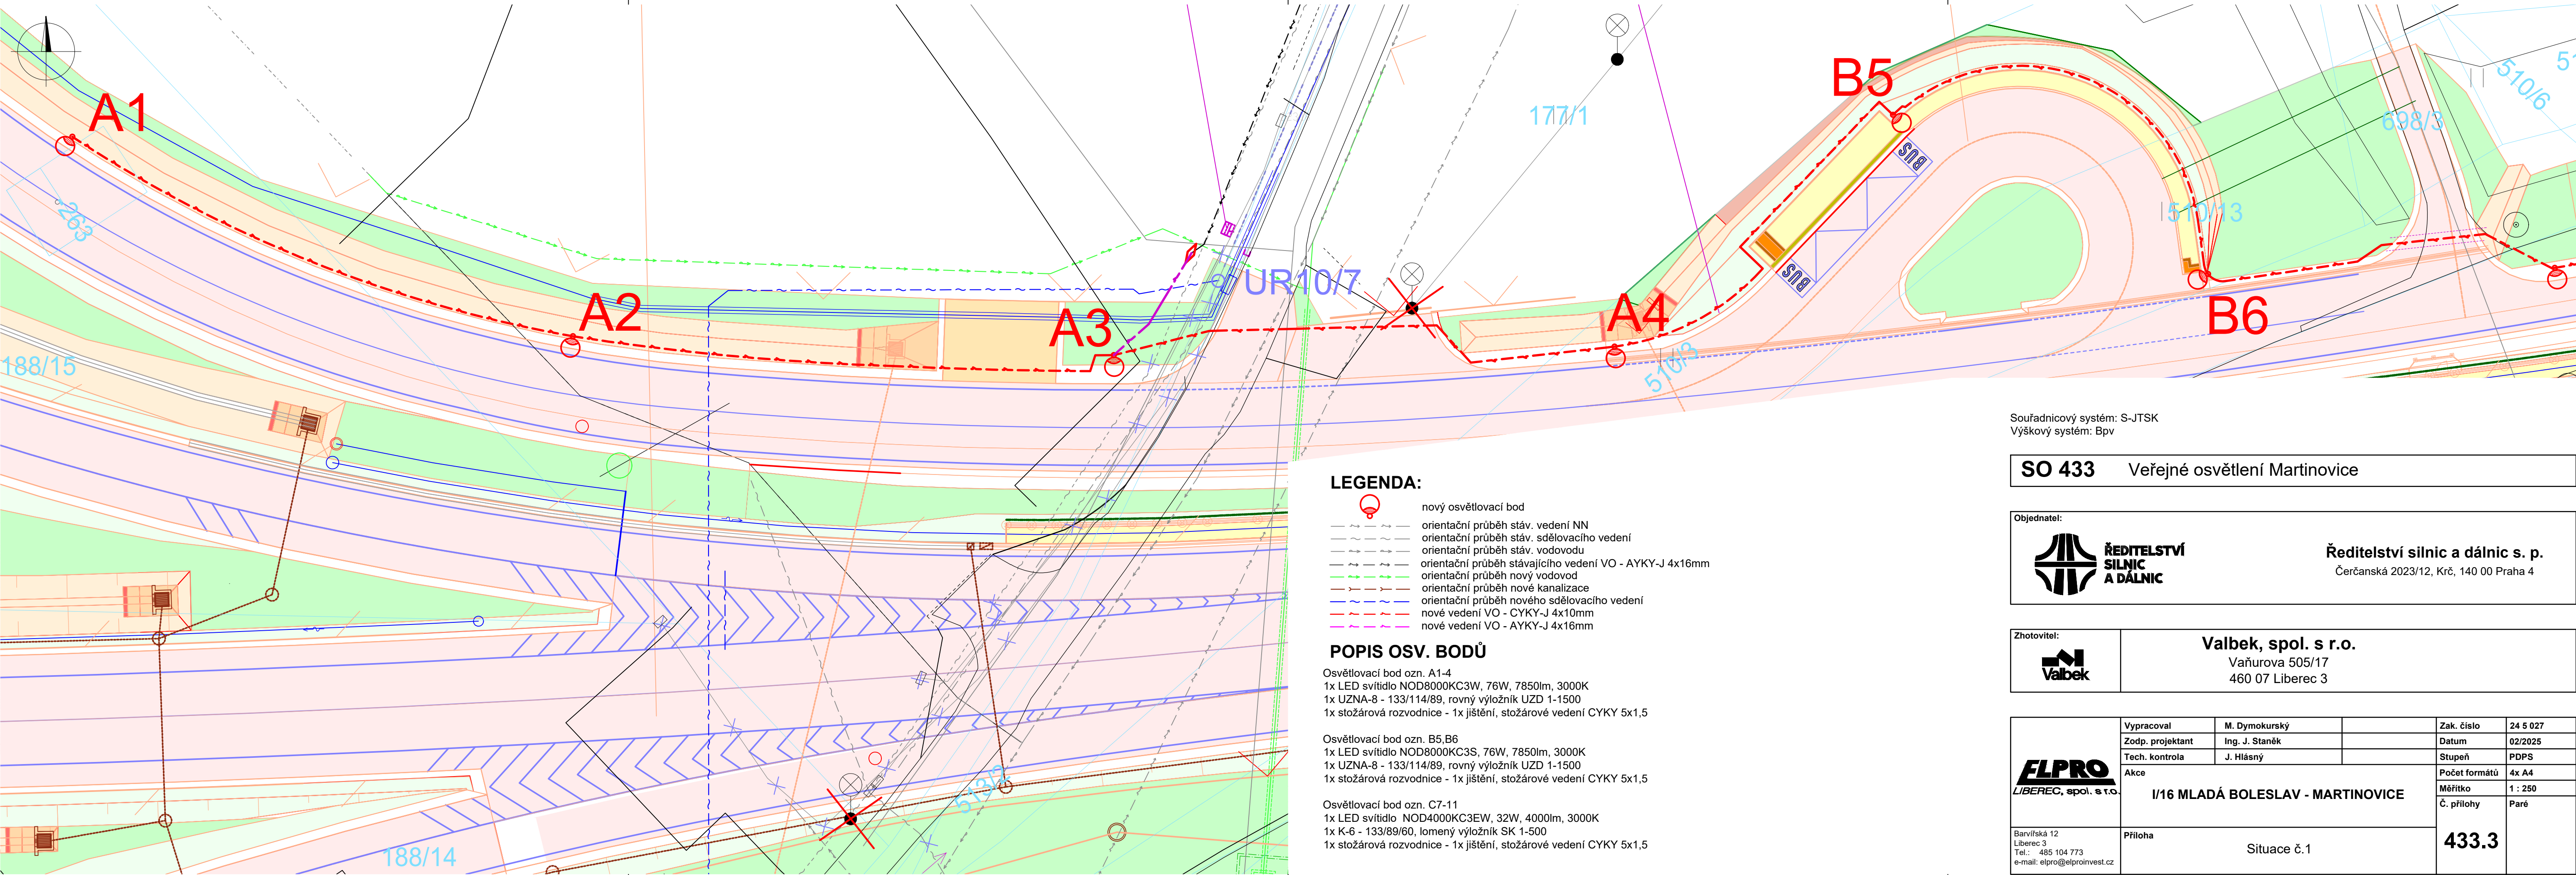

Souřadnicový systém: S-JTSK
Výškový systém: Bpv

SO 433 Veřejné osvětlení Martinovice

Objednatel:



ŘEDITELSTVÍ
SILNIC
A DÁLNIC

Ředitelství silnic a dálnic s. p.
Čerčanská 2023/12, Krč, 140 00 Praha 4

Zhotovitel:



Valbek, spol. s r.o.
Vaňurova 505/17
460 07 Liberec 3



Vypracoval	M. Dymokurský	Zak. číslo	24 5 027
Zodp. projektant	Ing. J. Staněk	Datum	02/2025
Tech. kontrola	J. Hlásný	Stupeň	PDPS
Akce		Počet formátů	4x A4
I/16 MLADÁ BOLESLAV - MARTINOVICE		Měřítko	1 : 250
		Č. přílohy	Paré
		433.3	
Příloha		Situace č.1	

Barviřská 12
Liberec 3
Tel.: 485 104 773
e-mail: elpro@elproinvest.cz