


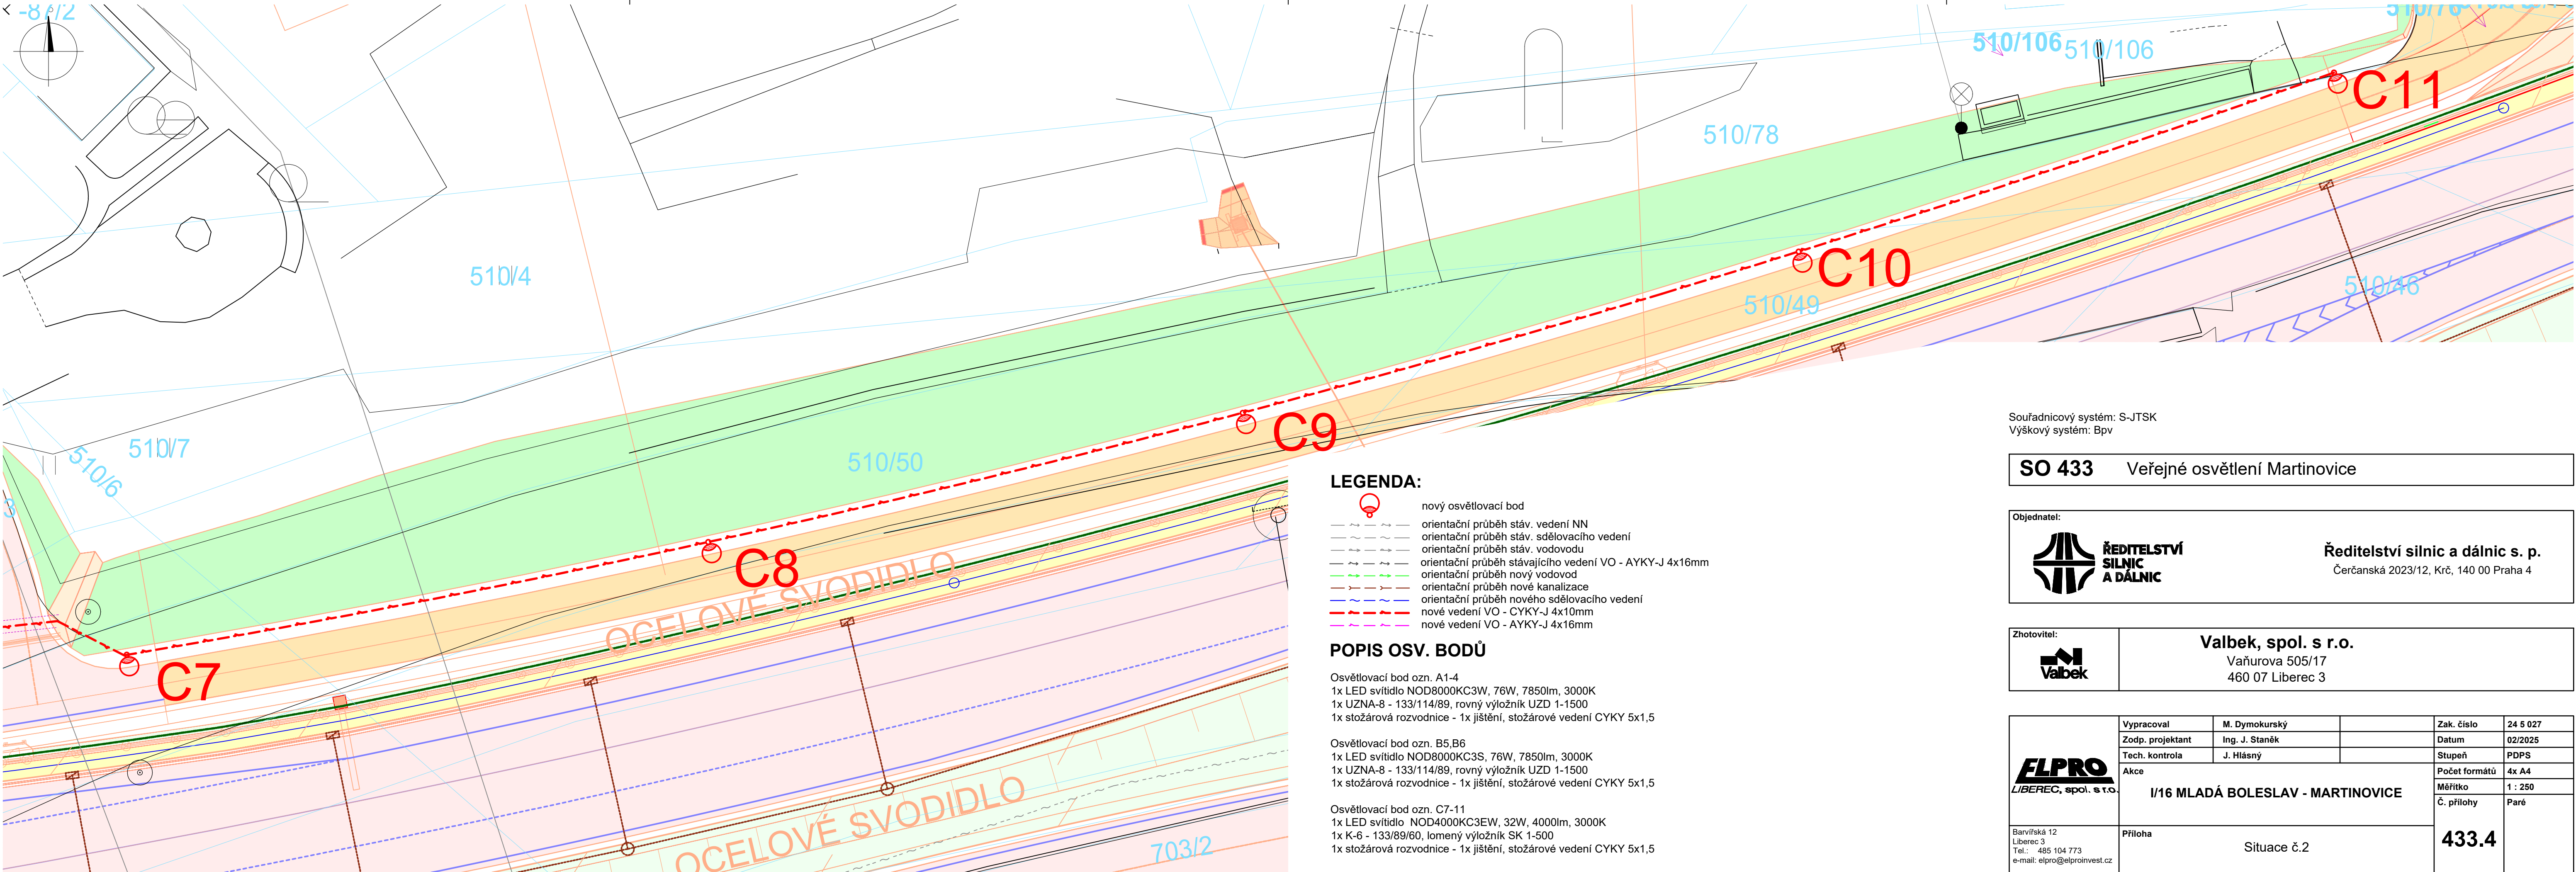

Souřadnicový systém: S-JTSK
Výškový systém: Bpv

SO 433 Veřejné osvětlení Martinovice

Objednatel:



**ŘEDITELSTVÍ
SILNIC
A DÁLNIC**

Ředitelství silnic a dálnic s. p.
Čerčanská 2023/12, Krč, 140 00 Praha 4

Zhotovitel:



Valbek, spol. s r.o.
Vaňurova 505/17
460 07 Liberec 3

 LIBEREC, spol. s r.o.	Vypracoval	M. Dymokurský		Zak. číslo	24 5 027
	Zodp. projektant	Ing. J. Staněk		Datum	02/2025
	Tech. kontrola	J. Hlásný		Stupeň	PDPS
	Akce			Počet formátů	4x A4
	I/16 MLADÁ BOLESLAV - MARTINOVICE			Měřítko	1 : 250
Barviřská 12 Liberec 3 Tel.: 485 104 773 e-mail: elpro@elproinvest.cz	Příloha Situace č.2			Č. přílohy	Paré
				433.4	