
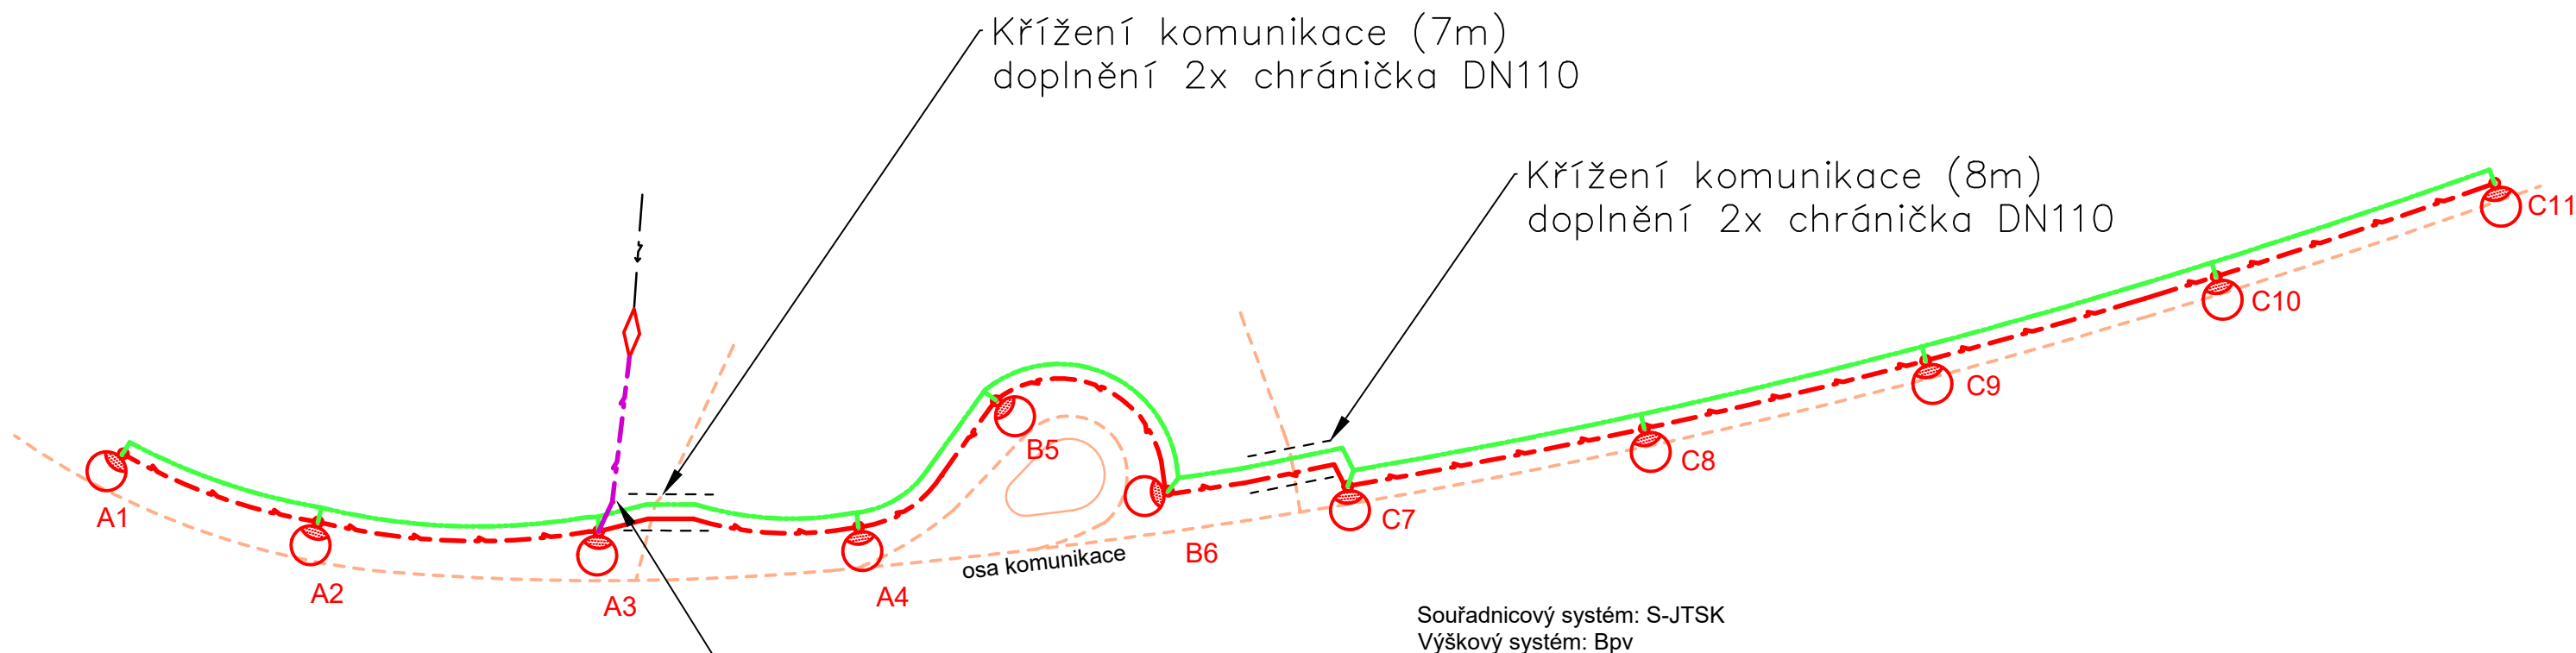


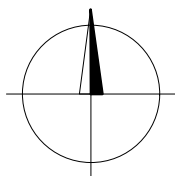

LEGENDA:

- nový osvětlovací bod
- nový osvětlovací bod
- stávající vedení NN AYKY 4x16 mm²
- orientační průběh nové kanalizace
- nové vedení VO - CYKY-J 4x10mm
- nové vedení VO - AYKY-J 4x16mm
- osa komunikace

Kabelová spojka NN
napojení na stávající vedení

Souřadnicový systém: S-JTSK
Výškový systém: Bpv

SO 433 Veřejné osvětlení Martinovice

Objednatel:



Ředitelství silnic a dálnic s. p.
Čerčanská 2023/12, Krč, 140 00 Praha 4

Zhotovitel:



Valbek, spol. s r.o.
Vaňurova 505/17
460 07 Liberec 3

POPIS OSV. BODŮ

Osvětlovací bod ozn. A1-4
1x LED svítidlo NOD8000KC3W, 76W, 7850lm, 3000K
1x UZNA-8 - 133/114/89, rovný výložník UZD 1-1500
1x stožárová rozvodnice - 1x jištění, stožárové vedení CYKY 5x1,5

Osvětlovací bod ozn. B5,B6
1x LED svítidlo NOD8000KC3S, 76W, 7850lm, 3000K
1x UZNA-8 - 133/114/89, rovný výložník UZD 1-1500
1x stožárová rozvodnice - 1x jištění, stožárové vedení CYKY 5x1,5

Osvětlovací bod ozn. C7-11
1x LED svítidlo NOD4000KC3EW, 32W, 4000lm, 3000K
1x K-6 - 133/89/60, lomený výložník SK 1-500
1x stožárová rozvodnice - 1x jištění, stožárové vedení CYKY 5x1,5

 LIBEREC, spol. s r.o.	Vypracoval	M. Dymokurský		Zak. číslo	24 5 027
	Zodp. projektant	Ing. J. Staněk		Datum	02/2025
	Tech. kontrola	J. Hlásný		Stupeň	PDPS
	Akce			Počet formátů	2x A4
	I/16 MLADÁ BOLESLAV - MARTINOVICE			Měřítko	
Barvířská 12 Liberec 3 Tel.: 485 104 773 e-mail: elpro@elproinvest.cz	Příloha Schéma VO			Č. přílohy	Paré
				433.5	