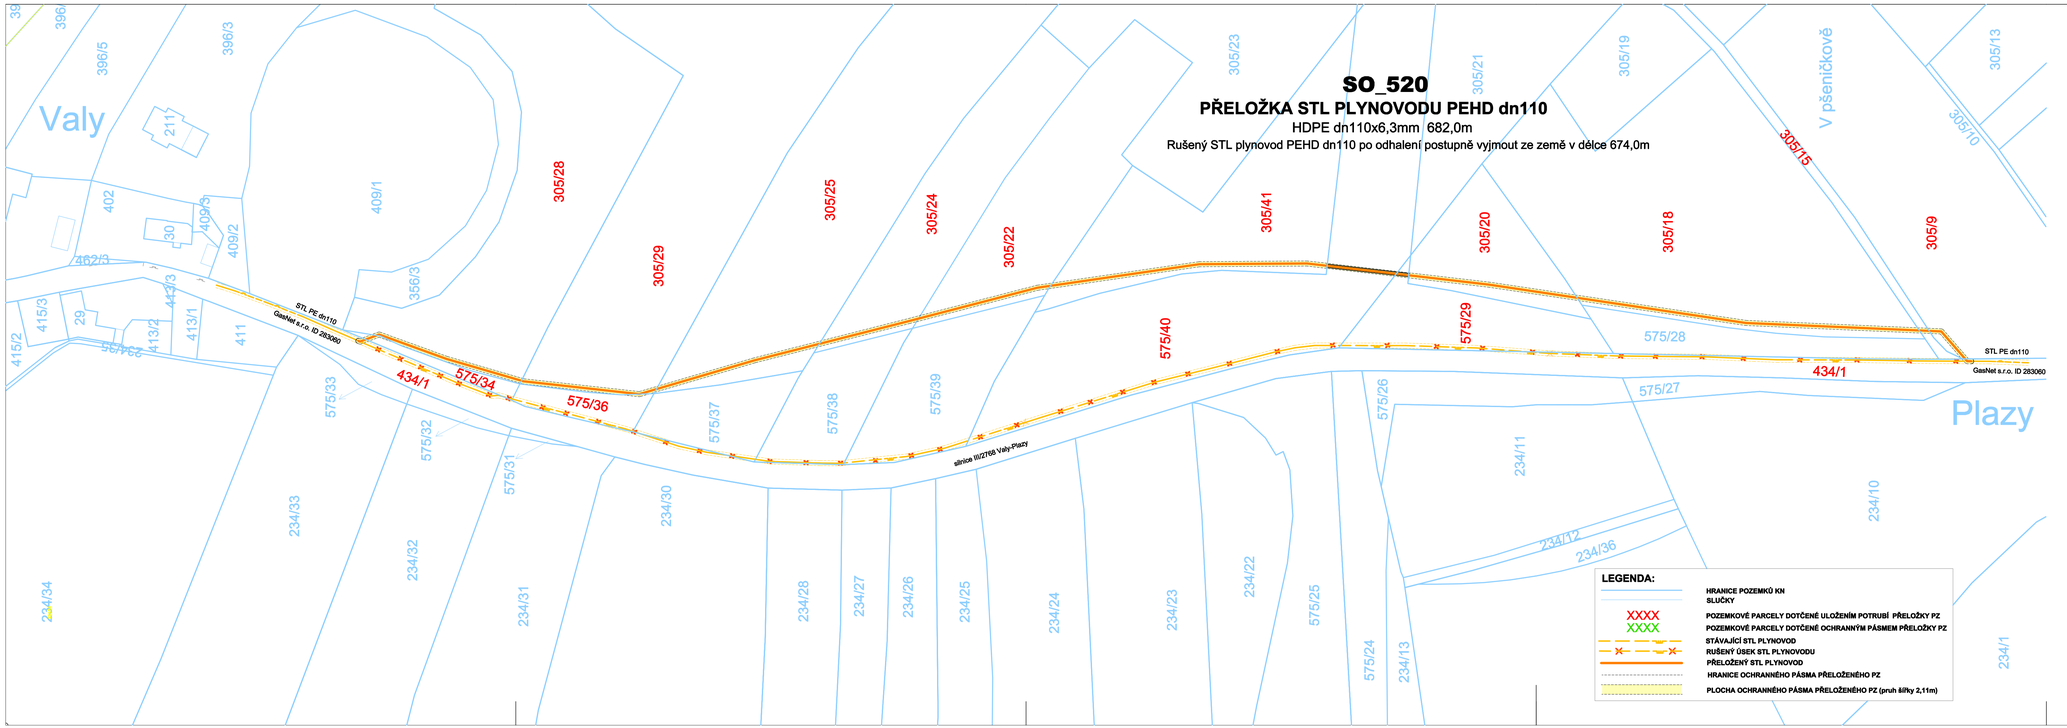


SO_520

PŘELOŽKA STL PLYNOVODU PEHD dn110

HDPE dn110x6,3mm 682,0m

Rušený STL plynovod PEHD dn110 po odhalení postupně vyjmout ze země v délce 674,0m

TABULKA DOTČENÝCH POZEMKŮ

ČPP	VLASTNÍK	DL. ULOŽENÍ (m) STL
434/1	Středočeský kraj, Zborovská 81/11, Smíchov, 15000 Praha 5 Krajská správa a údržba silnic Středočeského kraje, p.o., Zborovská 81/11, Smíchov, 15000 Praha 5	6,20
575/34	Česká Republika Ředitelství silnic a dálnic s. p., Čerčanská 2023/12, Krč, 14000 Praha 4	4,76
305/28	Hendrych Josef, č. p. 35, 29301 Dolní Stakory 1/3 Hendrychová Anna, 29301 Dolní Stakory 1/3	62,74
305/29	Kočová Božena, Erbenova 875, Mladá Boleslav II, 29301 Mladá Boleslav	56,10
575/34	Česká Republika Ředitelství silnic a dálnic s. p., Čerčanská 2023/12, Krč, 14000 Praha 4	0,10
305/25	Čubová Daniela Ing., Reporyjské náměstí 11, Reporyje, 15500 Praha 5 1/2 Janů Ivana JUDr., Zavadilova 1731/28, Dejvice, 16000 Praha 6 1/6 Kaliper Jiří Ing., Zoulcovice 110, 26705 Nižbor 1/9 Kaliper Václav Ing., Na Dubích 1164, Mladá Boleslav III, 29301 2/9	67,90
305/24	Hoffmanová Zdeňka, Nad Skalkou 577, 29401 Bakov nad Jizerou 1/2 Plzrta Karel, č. p. 75, 29431 Ptákovà Lhota 1/2	42,10
305/22	Skramovský Anna, č. p. 8, 29301 Plazy 1/2 Skramovský Petr, č. p. 8, 29301 Plazy 1/2	56,00
305/41	Kočová Božena, Erbenova 875, Mladá Boleslav II, 29301 Mladá Boleslav	114,60
305/40	Česká Republika Ředitelství silnic a dálnic s. p., Čerčanská 2023/12, Krč, 14000 Praha 4	28,60
575/29	Česká Republika Ředitelství silnic a dálnic s. p., Čerčanská 2023/12, Krč, 14000 Praha 4	5,17
305/20	Cíla Josef, č. p. 36, 29301 Plazy 1/4 Riesnerová Jaroslava, č. p. 36, 29301 Plazy 3/4	70,00
305/18	Římskokatolická farnost Plazy, Kateřiny Millibé 55/10, Mladá Boleslav I, 29301 Mladá Boleslav	141,60
305/15	Obec Plazy, č. p. 46, 29301 Plazy	4,10
305/9	Římskokatolická farnost Plazy, Kateřiny Millibé 55/10, Mladá Boleslav I, 29301 Mladá Boleslav	20,00

k.ú. Plazy
721590

Souřadnicový systém: S-JTSK
Výškový systém: Bpv

SO 520 Přeložka STL plynu v km 2,225

Objednatel:

Ředitelství silnic a dálnic s. p.
Čerčanská 2023/12, Krč, 140 00 Praha 4

Valbek, spol. s r.o.
Vaňurova 505/17
460 07 Liberec 3

LEGENDA:

- HRANICE POZEMKŮ KN SLUČKY
- XXXX / XXXX — POZEMKOVÉ PARCELY DOTČENÉ ULOŽENÍM POTRUBÍ PŘELOŽKY PZ
- POZEMKOVÉ PARCELY DOTČENÉ OCHRANNÝM PÁSMEM PŘELOŽKY PZ
- STÁVAJÍCÍ STL PLYNOVOD
- RUŠENÝ ÚSEK STL PLYNOVODU
- PŘELOŽKY STL PLYNOVOD
- HRANICE OCHRANNÉHO PÁSMA PŘELOŽENÉHO PZ
- PLOCHA OCHRANNÉHO PÁSMA PŘELOŽENÉHO PZ (pruh šířky 2,11m)

Zhotovitel:
PETR KARMAZÍN
projektování staveb

Zhotovitel:
Petr Karmazín - projektování staveb
Tvrdošická 26
Jablonec n.N. 466 06
tel.: 483 317 150
e-mail: karmazinplyn@volny.cz

Vypracoval	Ing. POPR Petr	Zak. číslo	21-IJ13-001
Zodp. projektant	Ing. POPR Petr	Datum	02/2025
Tech. kontrola	Karmazín Petr	Stupeň	PDPS
Akce:	I/16 MLADÁ BOLESLAV - MARTINOVICE	Počet formátů	5 x A4
		Měřítko	1 : 1000
Příloha:	ZÁKRES DO KATASTRÁLNÍ MAPY	Č. přílohy: 2.	Paré :