



PROPOJ "A" PE dn110/110 staniční 0,00m

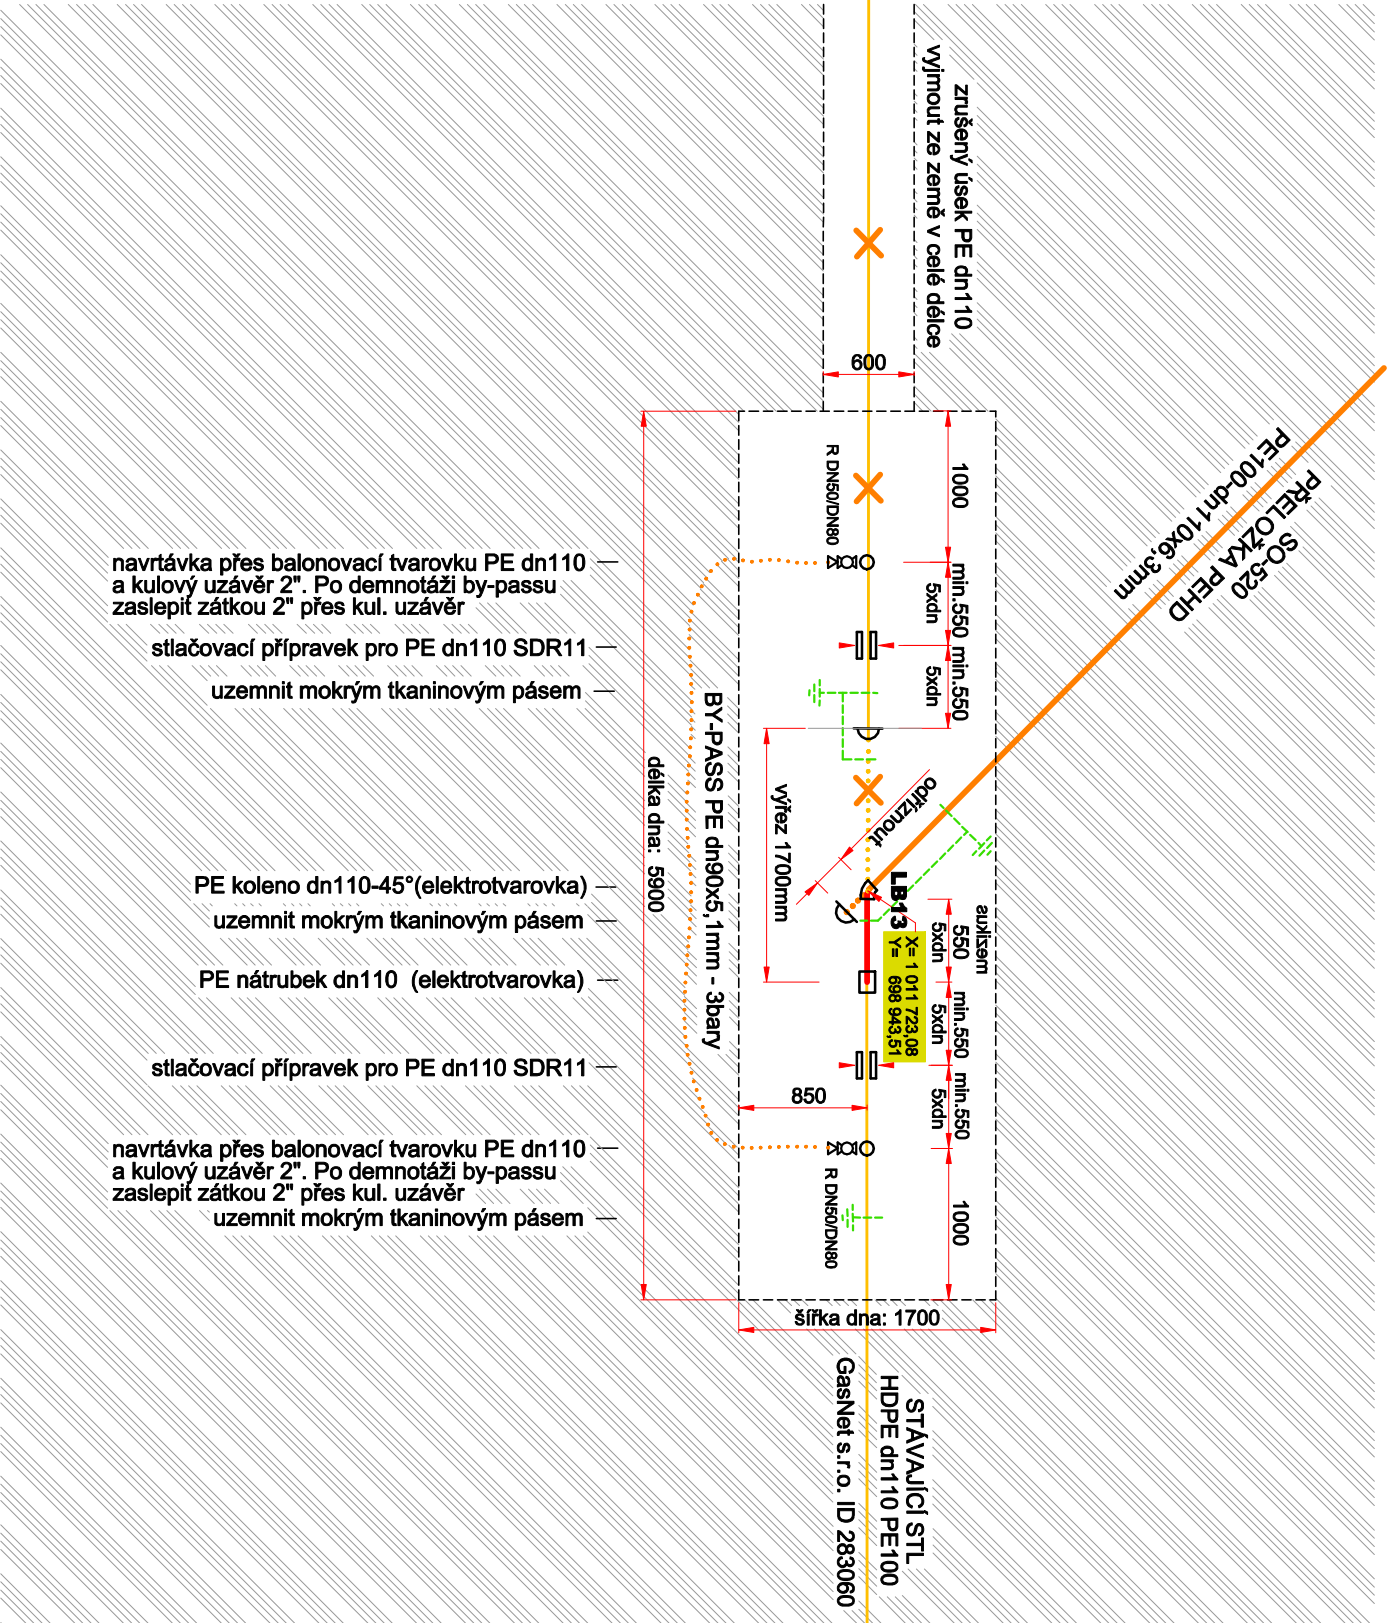

PROPOJ "B" PE dn110/110 staniční 680,85m

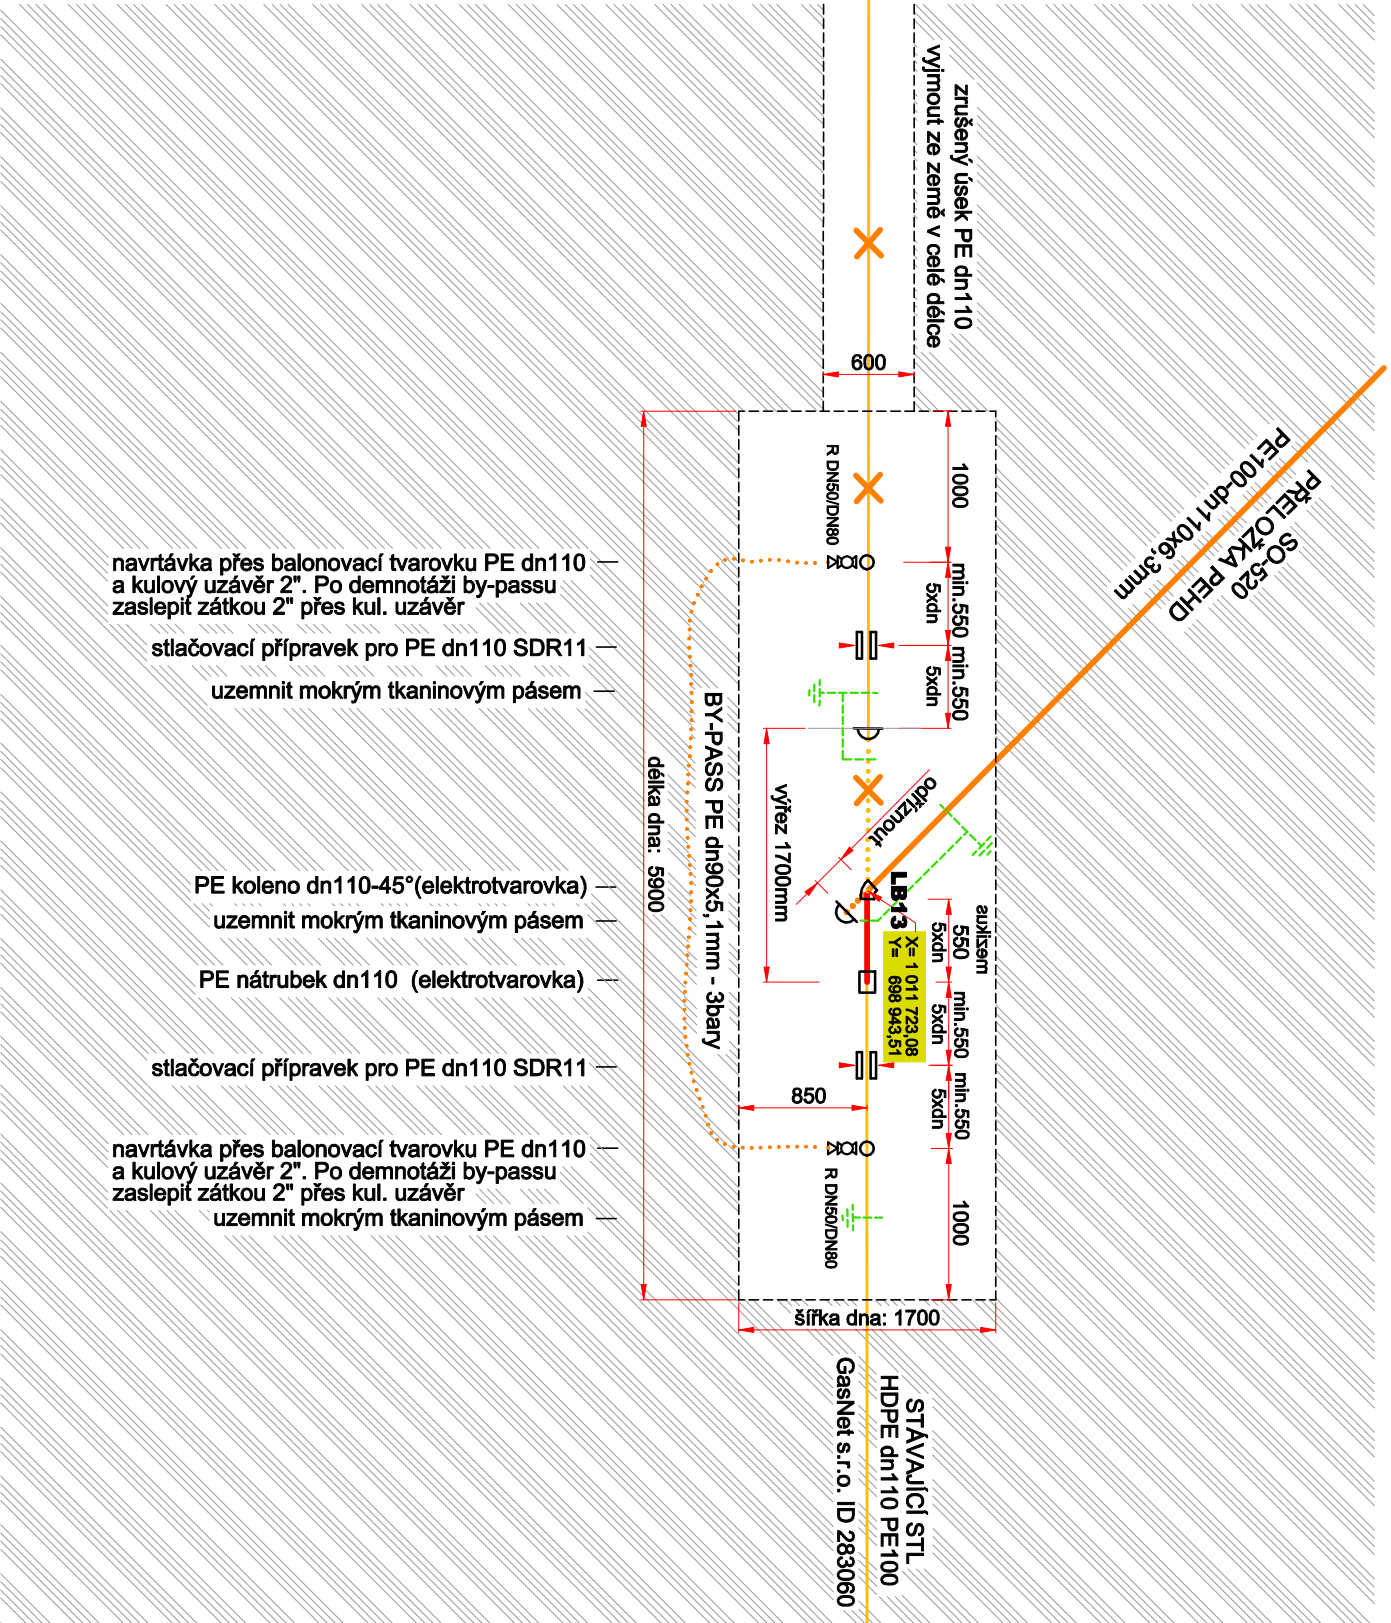

PO SEMNUTÍ STLAČOVACÍH PŘÍPRAVKŮ BUDE TVAR POTRUBÍ ZPĚTNĚ UPRAVEN ZAKRUHOVACÍM PŘÍPRAVKEM PO DOBU MIN. 1 HODINY

PO CELU DOBU UZAVÍRKY BUDE ZAJIŠTĚNO NÁHRADNÍ ZÁSOBOVÁNÍ POTRUBNÍM BY-PASEM NÁPOJENÝM NA SAMOSTATNÉ NAVRTÁVKY. POPOŠAŇA A OŠADÍ SE DELEŇA OPRÁVARENSKÁ TVAROVKA NEBO TRMEN A KAŽDE MÍSTO SE GEODETICKY ZEJMĚŘÍ DO GDO.

PROFIL BY PÁSU BUDE STANOVEN VE SPOLUPRÁCI S PROVOZOVATELEM PZ PŘI ODSOUHLASOVÁNÍ PRACOVNÍHO POSTUPU PRÁCI V ZÁVISLOSTI NA KONKRETNÍM TERÉNU. PROPOJOVACÍ PRÁCI A AKTIVNÍ SITUACE NA PL. VYKONÁVÁNÍ SÍTI

CHLADNUTÍ STANOVENOU VÝROBCEM ELEKTROTVAROVKY!

OD POUČKU POTRUBÍ A min. 1000mm VE SMĚRU POTRUBÍ OD PROVÁDĚNÝCH SVARŮ NEBO TVAROVEK HLoubKA ŠACHTY

PRO Dvě OSOBY S BŘE MENEM, DLE MAŘE NÍ VLADY č. 591/2006 BUDOU STĚ NY VÝKOPU HLUBŠÍ HO NEŽ 1,50m
PAŤE NÝ PAŽE NÍM, NEBO BUDOU STĚ NY VYSAHOVA NY VE SKLO NÚ 2:1

POŽÁDÁVKY NA BEZPEČNOST PRACÍ A PROTIPOŽÁRNÍ BEZPEČNOST. ISOL I WEDENY V TECHNICKÉ ZPRAVĚ PN

Souřadnicový systém: S-JTSK Výškový systém: Bpv	
SO 520	Přeložka STL plynu v km 2,225

Zhotovitel: Petř Karmařin - projektování staveb Turkovičkova 26 Jablonec n. L. 4601 06 Tel: 603 517 150 e-mail: karmarzp@century.cz		Zak. číslo 21-L113-001	
Vyraboval	Ing. POPR Petr	Datum	02/2025
Zodp. projektant	Ing. POPR Petr	Stupeň	PDPS
Tech. kontrola	Karmařin Petr	Počet formátů	3 x A4
Akos: I/16 MLADÁ BOLESLAV - MARTINOVICE		Měřítko	1 : 50
Příloha:		Č. přílohy:	Právé :
DETAIL PROPOJOVACÍCH PRACÍ		5.	