


VOLNÝ TERÉN - POLE

mimo tělesa budovaných komunikací (hloubka do 1,50m)

mocnost vrstvy ornice a podomíči v jednotlivých částech trasy:

stanícení 0,00 ~ 200,00m		30cm+10cm
stanícení 200,00 ~ 300,00m		30cm+20cm
stanícení 300,00 ~ 420,00m		30cm+30cm
stanícení 420,00 ~ 680,00m		30cm+60cm

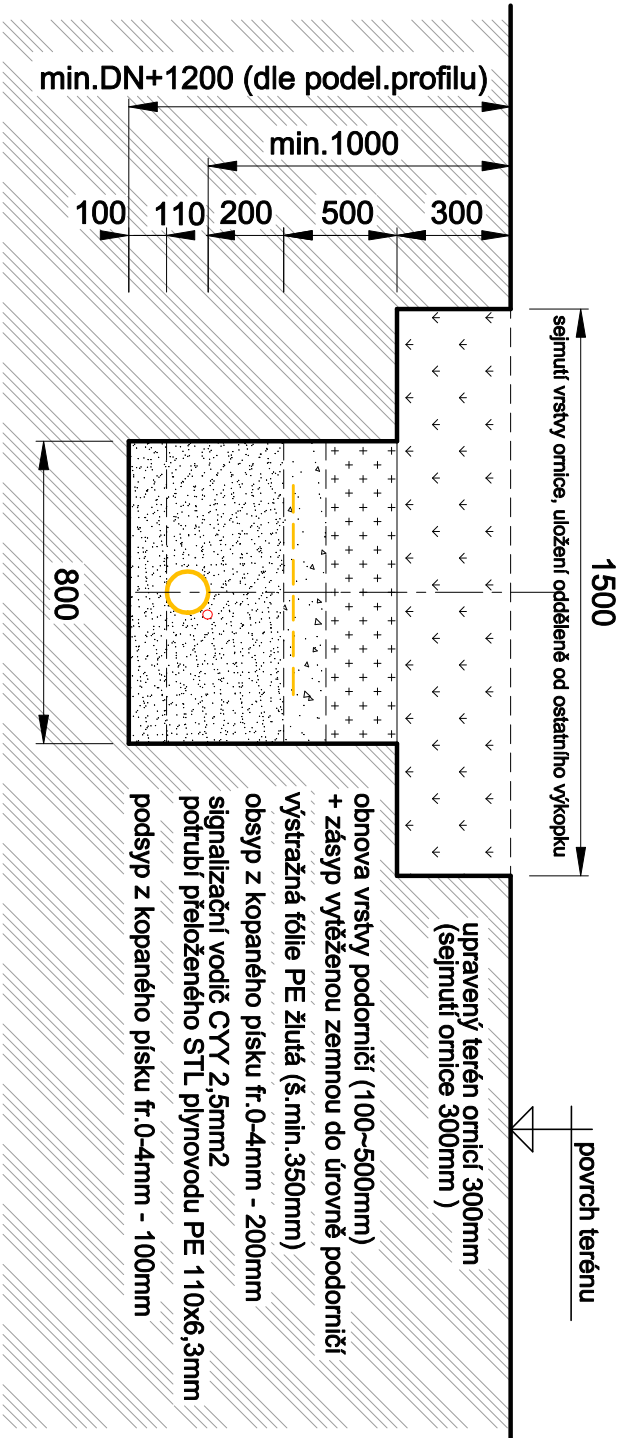

POZNÁMKA:

Výkopy budou prováděny a zajištěny dle zásad Nařízení vlády č.591/2006 Sb.

Stěny výkopu výšky větší než 1,50m opatřit pažením nebo upravit do sklonu 2:1

Polohu odhaleného potrubí plynovodu v propojovacích šachtách zabezpečit vyvěšením

na nosníky napříč výkopu a následně podepřít montážními podpěrami.,

Veškeré zemní práce ve vzdálenosti menší než 1,5m od potrubí budou provedeny výhradně

ručně podle podřínek stanovených provozovatelem PZ a předpisem TřP GAS 700 03 a

po ověření polohy PZ ručně kopanými sondami.

POZNÁMKA:

Příklady hutnění lože pod potrubím k dosažení 88% PS:

1) 2x manuální hutnění urovnané vrstvy tl. do 10cm dusáním

2) 1x hutnění vrstvy 10cm deskovým vibrátorem 50-100kg s dvojitou deskou

Příklady hutnění obsypu potrubí k dosažení 95% PS:

1) 4x manuální hutnění vrstev po max. výšce 8cm dusáním z obou stran potrubí

2) 4x hutnění vrstev po max. výšce 15cm deskovým vibrátorem 50-100kg s dvojitou deskou současně z obou stran potrubí

Souřadnicový systém: S-JTSK

Výškový systém: Bpv

SO 520 Přeložka STL plynu v km 2,225

Objednatel:



ŘEDITELSTVÍ
SILNIC
A DÁLNIC

Ředitelství silnic a dálnic s. p.
Čerčanská 2023/12, Krč, 140 00 Praha 4



Valbek, spol. s r.o.

Vaňurova 505/17
460 07 Liberec 3



Zhotovitel:
PETR KARMAZIN
projektování staveb

Vypracoval Ing. POŘP Petr
Zodp. projektant Ing. POŘP Petr
Tech. kontrola Karmazin Petr
Akce: I/16 MLADÁ BOLESLAV - MARTINOVICE


Zak. číslo 21-L113-001
Datum 02/2025
Stupeň PDPS
Počet formátů 3 x A4
Měřítko 1 : 20
Č. přílohy: 6.

Přiložka: VZOROVÉ PŘÍČNÉ ŘEZY VÝKOPEM

Zhotovitel:
Petr Karmazin - projektování staveb
Turešská 26
Jablonec n.L. 468 08
tel: 483 317 150
e-mail: karmazindp@volny.cz

BUDOVANÉ TĚLESO SILNICE I/16 (SO-101)

terén upravený sejmutím ornice a podomíči vrstvy v rámci SO-020 Příprava staveniště

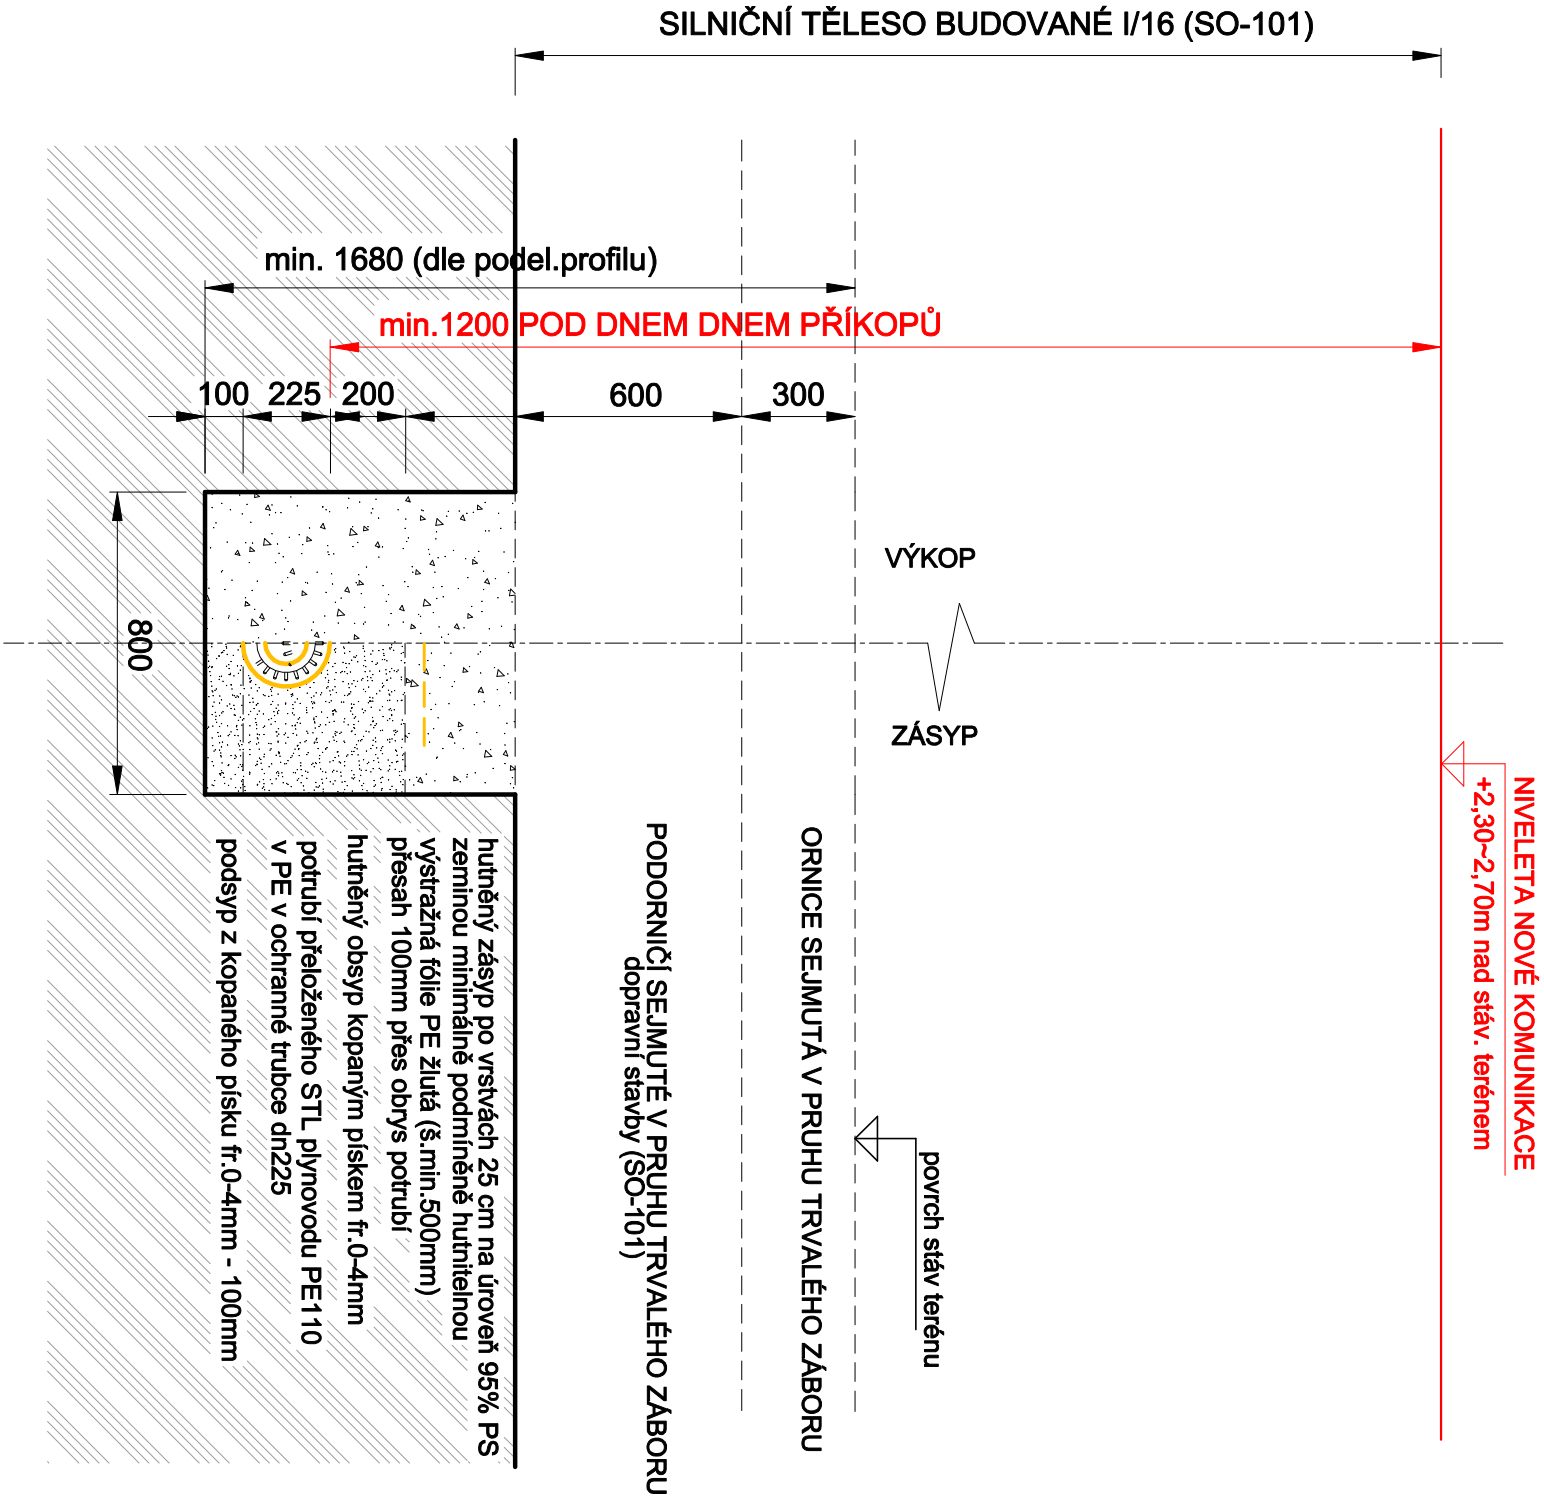

VÝKOP

ZÁSYP

ORNICE SEJMUTÁ V PRUHU TRVALÉHO ZÁBORU

PODOMÍČI SEJMUTÉ V PRUHU TRVALÉHO ZÁBORU
dopravní stavby (SO-101)

hutněný zásyp po vstřevách 25 cm na úroveň 95% PS
zemnínou minimálně podomíčně hutněnou
výstražná fólie PE žlutá (š.min.500mm)
přesah 100mm přes obrys potrubí
hutněný obsyp kopaným pískem fr.0-4mm
potrubí přeloženého STL plynovodu PE110
v PE v ochranné trubce dn225
podšyp z kopaného písku fr.0-4mm - 100mm