



PŮDORYS ČÁST 1 1:250

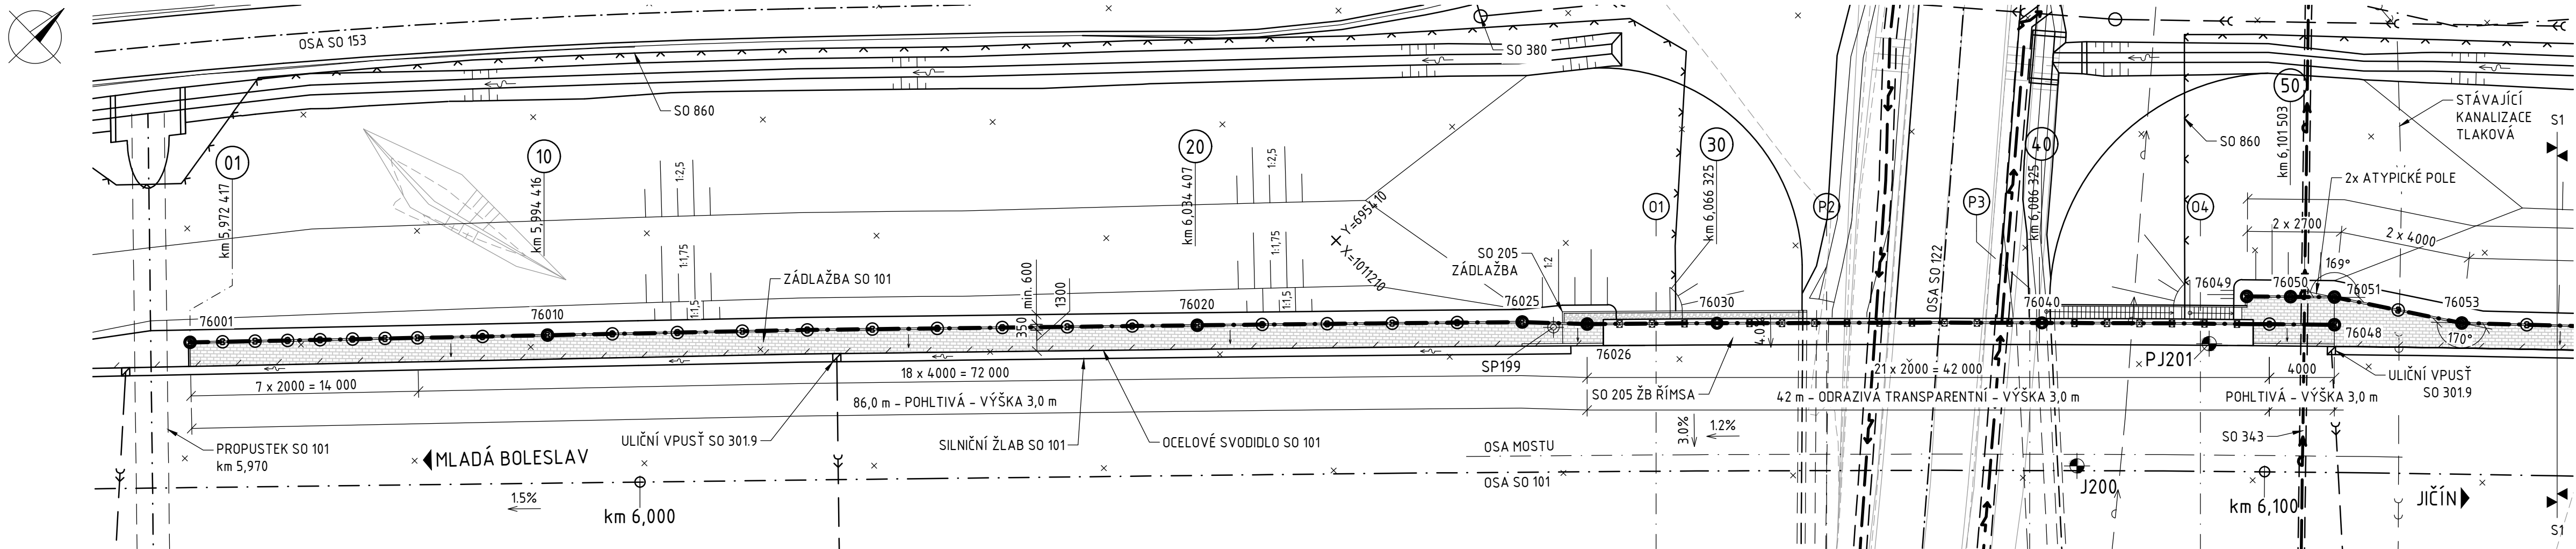

PŮDORYS ČÁST 2 1:250

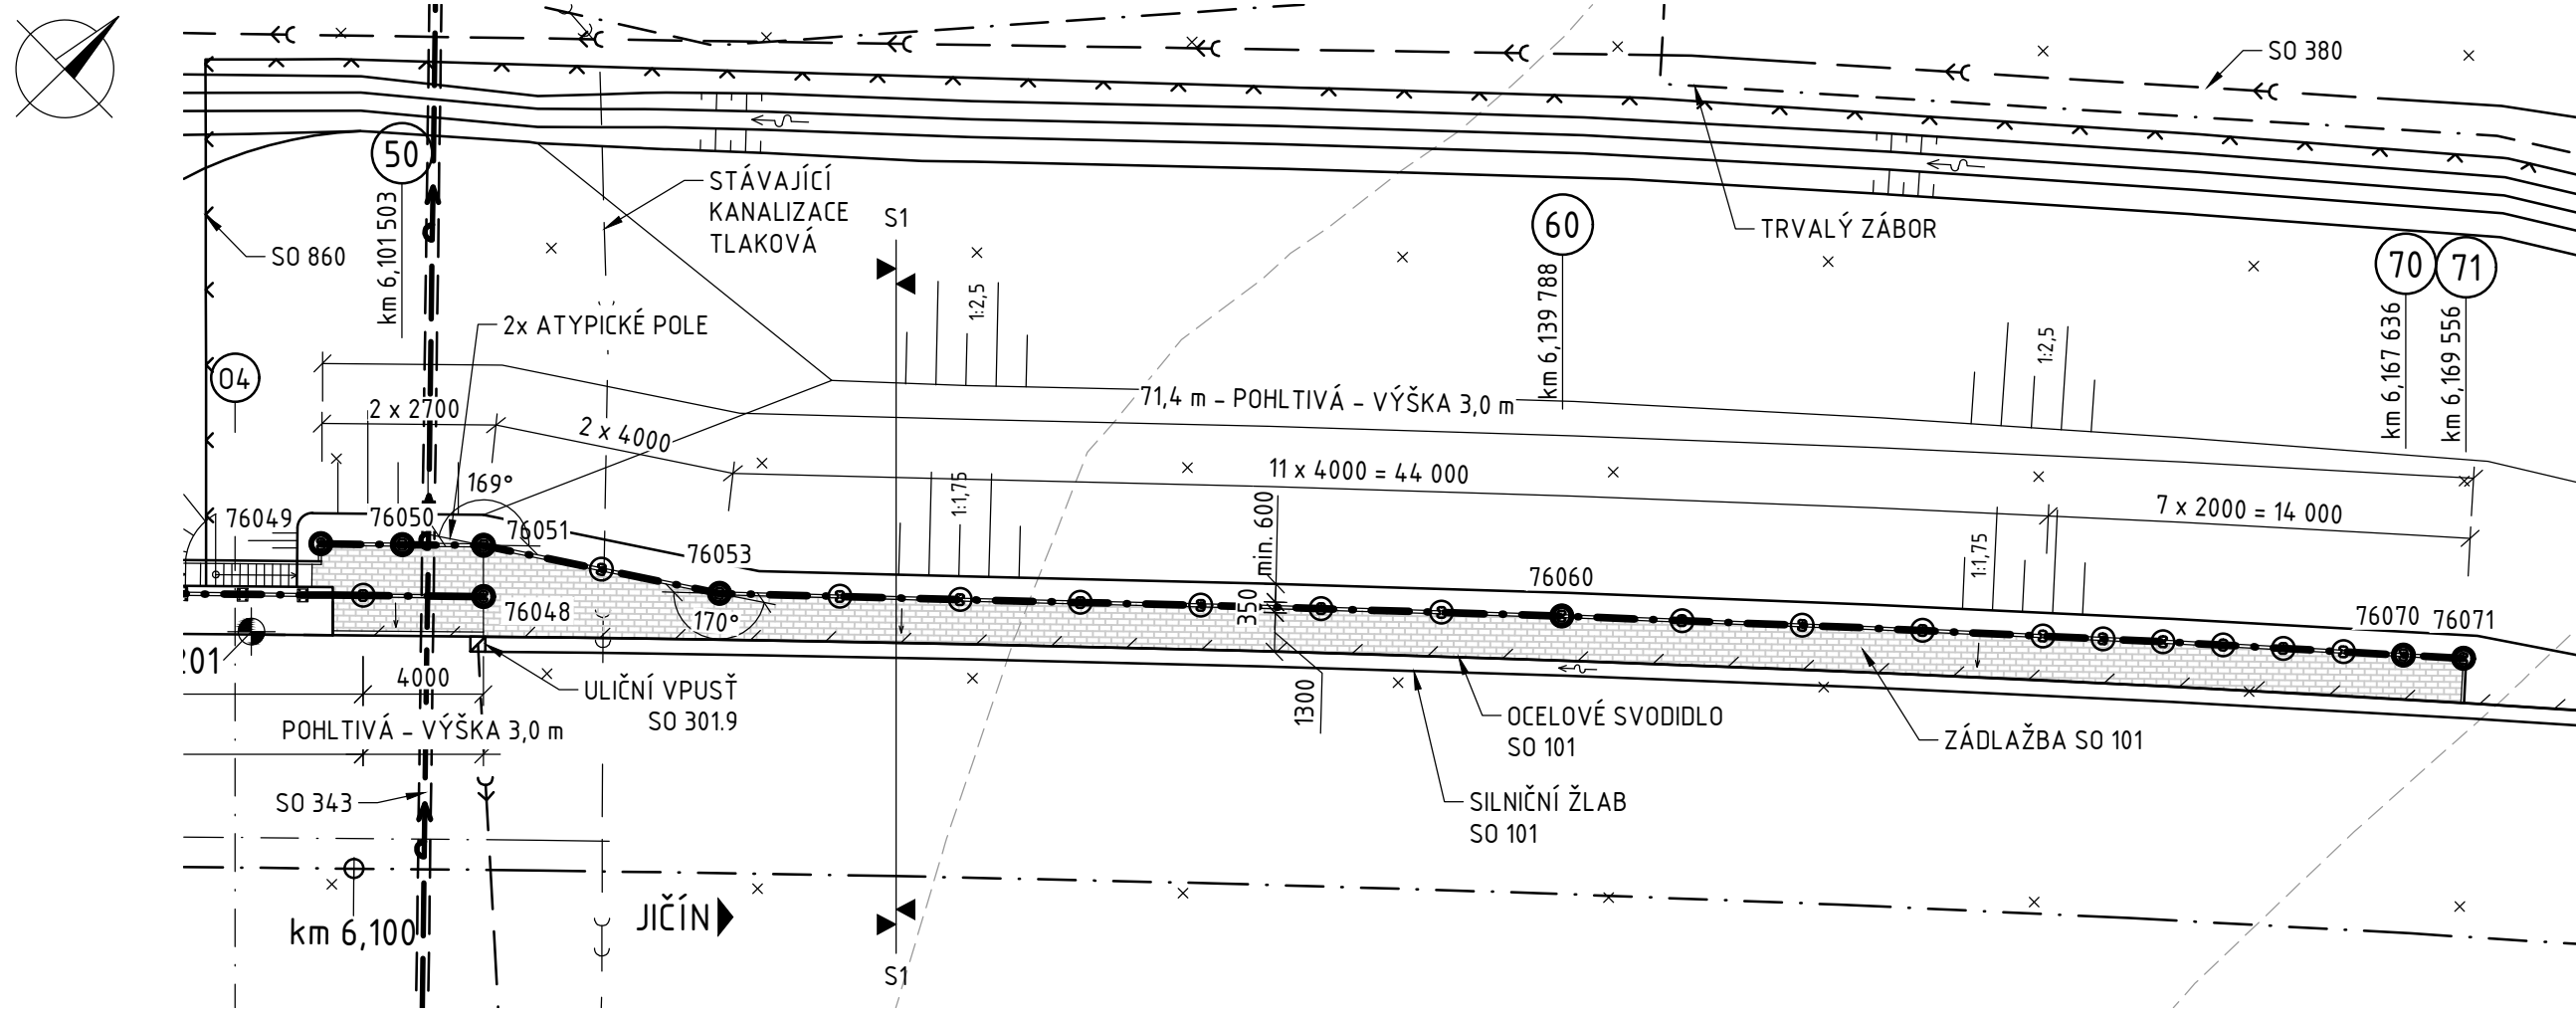

SOUŘADNICE VYTÝČOVACÍCH BODŮ

BOD	Y [m]	X [m]
76001	695454,872	1011264,786
76010	695439,803	1011248,758
76020	695412,257	1011219,754
76025	695398,408	1011205,325
76026	695395,521	1011202,556
76030	695389,963	1011196,802
76040	695375,985	1011182,498
76048	695363,308	1011169,719
76049	695368,335	1011172,353
76050	695366,429	1011170,442
76051	695364,522	1011168,530
76053	695357,900	1011164,042
76060	695337,777	1011144,572
76070	695317,283	1011125,494
76071	695315,806	1011124,146


LEGENDA

TRVALÝ ZÁBOR	---
DOČASNÝ ZÁBOR nad 1 rok	---
DOČASNÝ ZÁBOR do 1 roku	---


POZNÁMKY:

- VYTÝČOVACÍ ODCHYLKY: E 4.5.1 - GVS - SEZNAM SOUŘADNIC
- NEDÍLNOU SOUČÁSTÍ VÝKRESU JSOU SPECIFIKACE A POZNÁMKY UVEDENÉ NA VÝKRESE TECHNICKÝCH SPECIFIKACÍ A POZNÁMEK


VZOROVÝ PŘÍČNÝ ŘEZ NA NÁSYPU 1:50

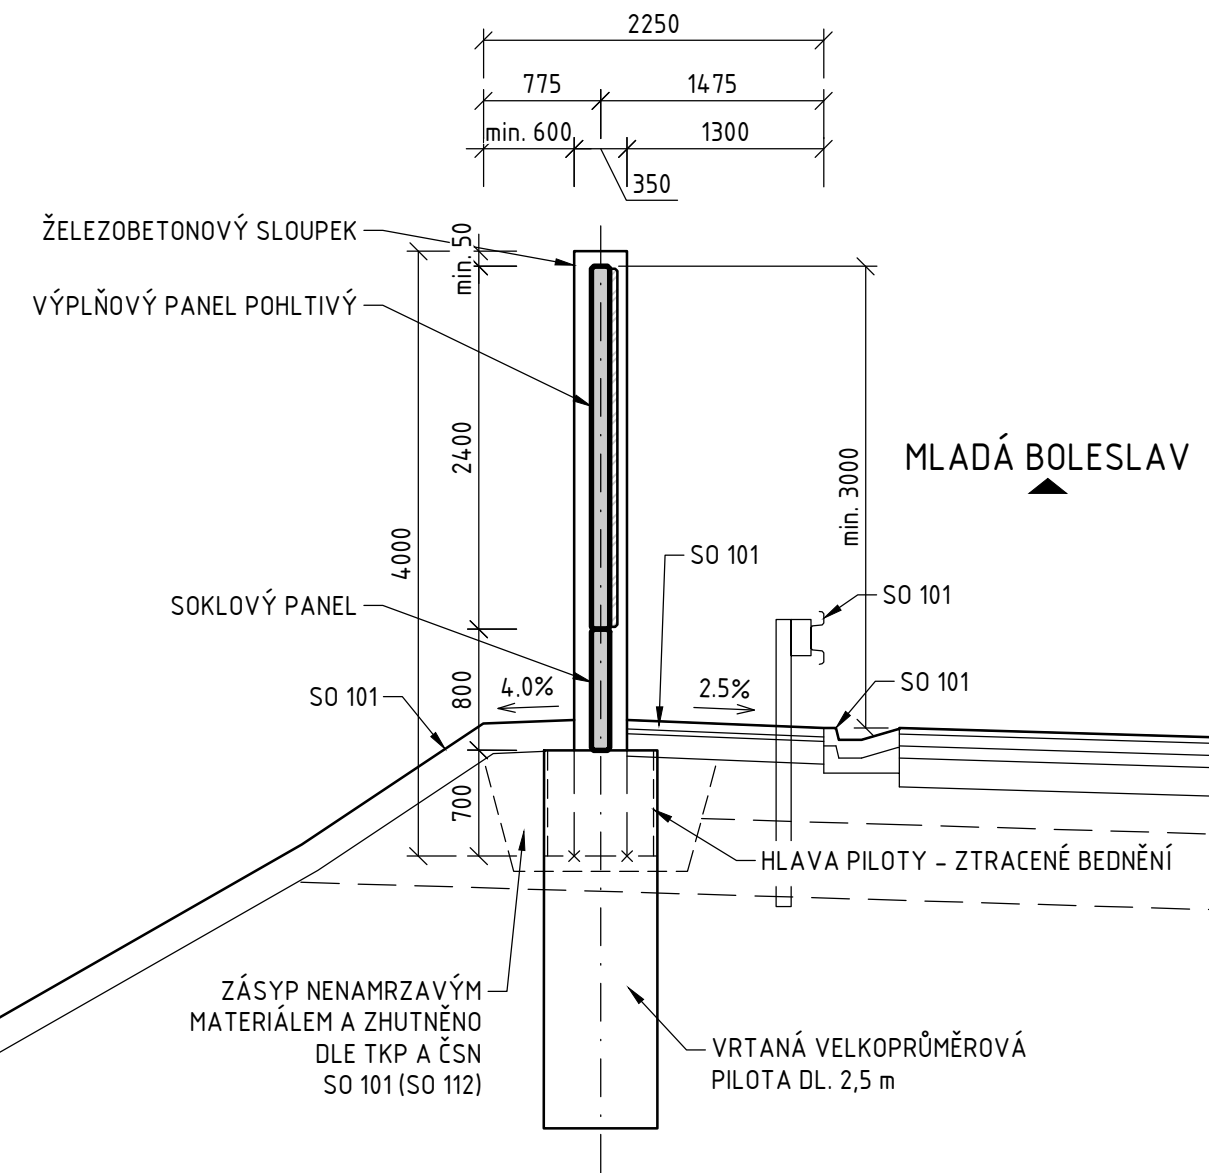

VZOROVÝ PŘÍČNÝ ŘEZ NA MOSTĚ 1:50

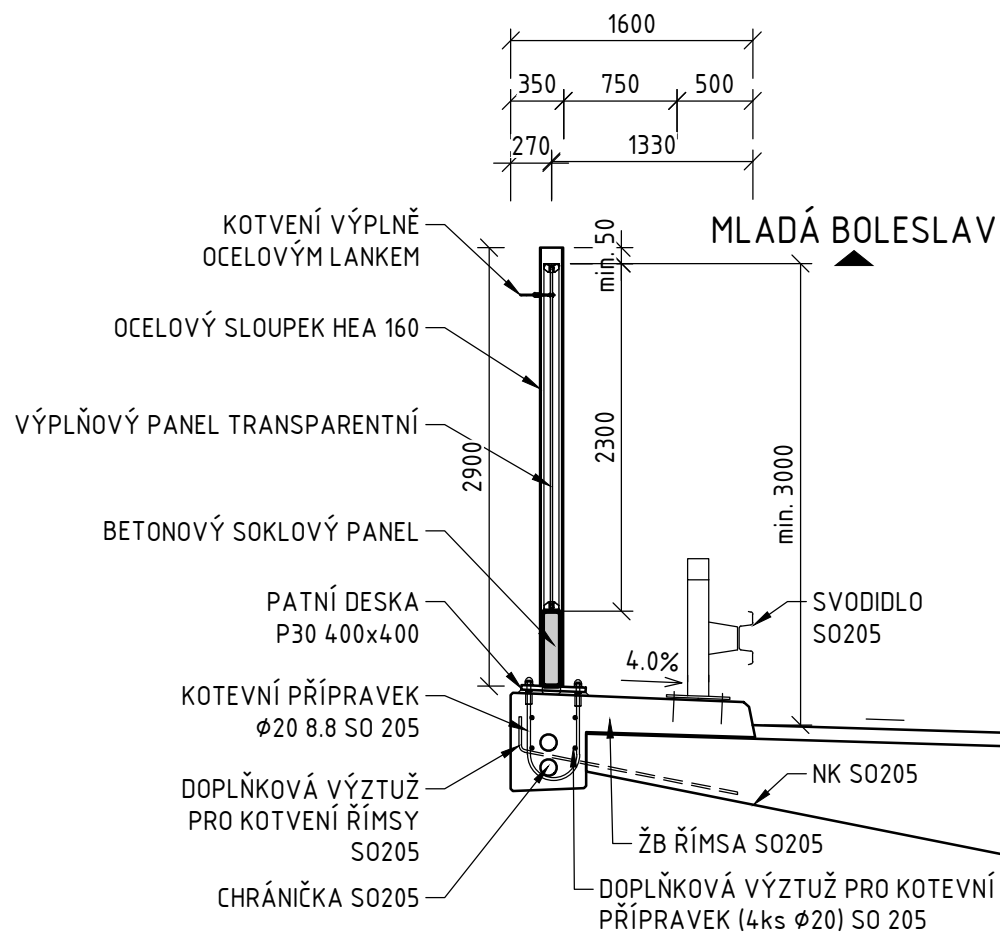

DETAIL PATNÍ DESKY 1:10

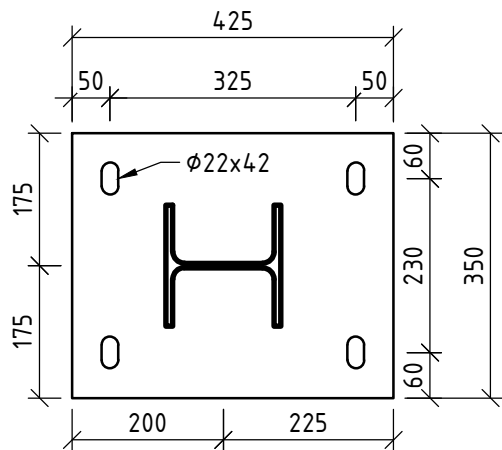


SOUVISEJÍCÍ OBJEKTY:

- SO 020 PŘÍPRAVA ÚZEMÍ
- SO 101 SILNICE I/16 MLADÁ BOLESLAV - MARTINOVICE
- SO 122 PŘELOŽKA SILNICE III/27612 V km 6,080
- SO 153 PŘÍSTUPY NA POZEMKY K.Ú. SUKORADY U MLADÉ BOLESLAVI
- SO 190 DOPRAVNÍ ZNAČENÍ
- SO 205 MOST NA I/16 PŘES PŘELOŽKU III/27612 V km 6,080
- SO 301.x ODVODNĚNÍ I/16
- SO 343 PŘELOŽKA VODOVODU PVC 160 V km 6,091
- SO 380 ÚPRAVY MELIORACÍ ZÚ - KÚ
- SO 413 PŘELOŽKA SLOUPOVÉ TRAFOSTANICE 22 kV, km 6,060
- SO 430 PŘELOŽKA KABELOVÝCH VEDENÍ NN km 6,060 - 6,075
- SO 461 PŘELOŽKA VEDENÍ SEK CETIN km 6,085
- SO 801 VEGETAČNÍ ÚPRAVY
- SO 810 KÁČENÍ ZELENĚ
- SO 830 REKULTIVACE PLOCH DOČASNÉHO ZÁBORU
- SO 860 OPLOCENÍ

SCHEMA VÝZTUŽE PILOTY 1:10

SPOTŘEBA VÝZTUŽE PILOT 55 kg/m3

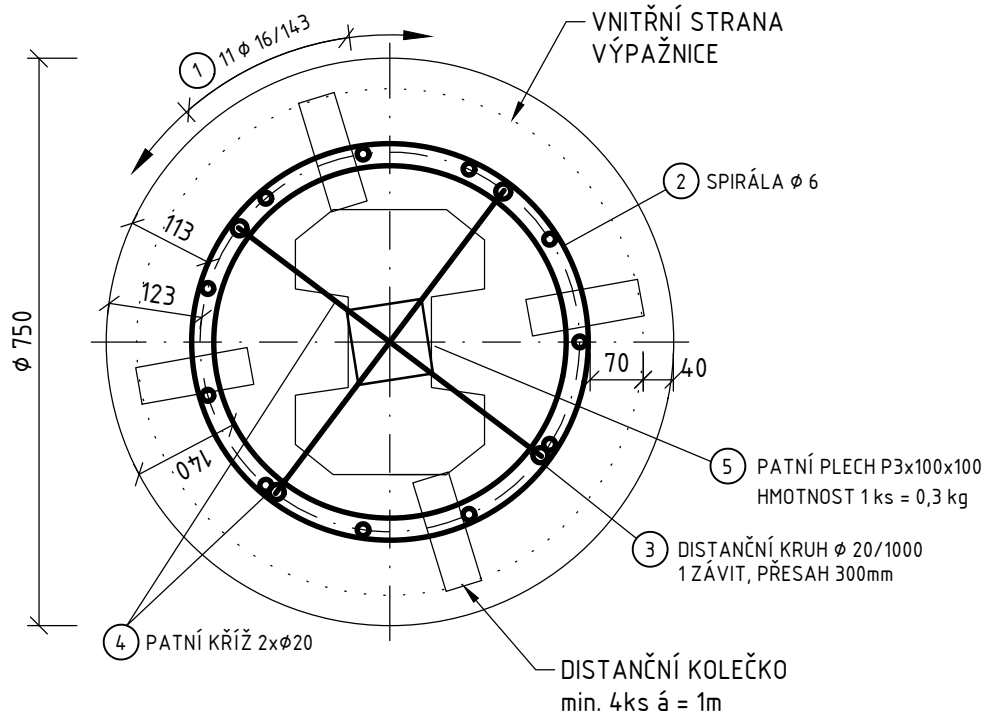

Souřadnicový systém: S-JTSK
Výškový systém: Bpv

SO 760 PROTIHLUKOVÁ STĚNA V km 6,1 VLEVO



Ředitelství silnic a dálnic s. p.
Čerčanská 2023/12, Krč, 140 00 Praha 4



Valbek, spol. s r.o.
Vaňurova 505/17
460 07 Liberec 3



Vypracoval	ING. T. JAKUBÍČEK	Zak. číslo	21-L113-001
Zodp. projektant	ING. T. JAKUBÍČEK	Datum	02/2025
Tech. kontrola	ING. I. BELDA	Stupeň	PDPS
Akce	I/16 MLADÁ BOLESLAV - MARTINOVICE	Počet formátů	8 x A4
Měřítko	1:250, 50, 10	Č. přílohy	Paré
Zhotovitel:	Příloha	03	
Valbek, spol. s r.o. Vaňurova 505/17 460 07 Liberec 3	PŮDORYS, VZOROVÉ PŘÍČNÉ ŘEZY, SCHEMA VÝZTUŽE PILOT		