


I/16 MLADÁ BOLESLAV - MARTINOVICE  
SO 801 VEGETAČNÍ ÚPRAVY  
SITUACE km 0,0 - 1,2 M 1:1 000

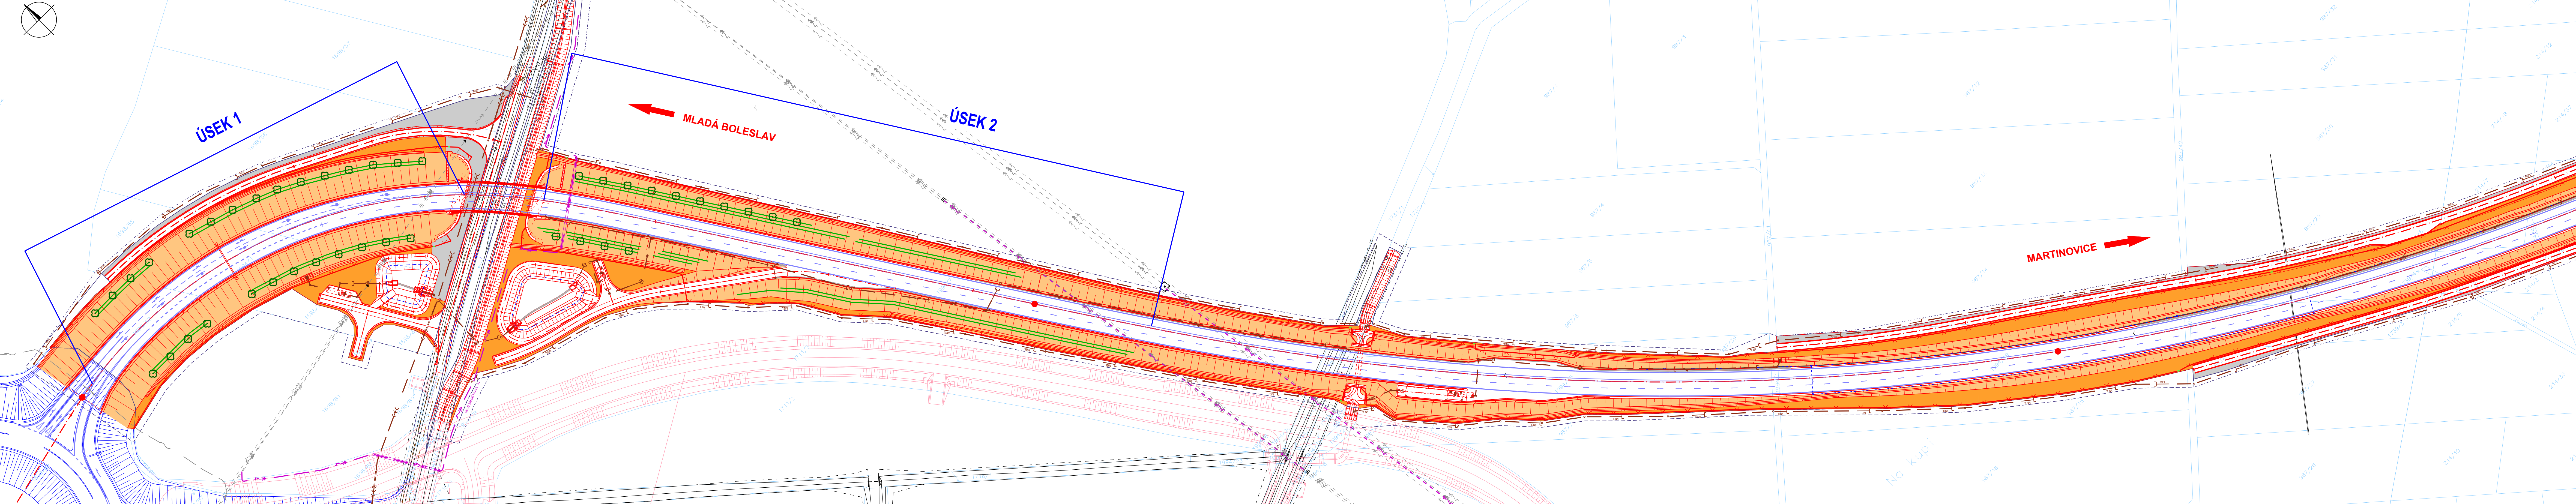

- LEGENDA
- Vegetační úpravy ve správně RSD
- ZATRAVNĚNÍ V ROVINĚ
  - ZATRAVNĚNÍ VE SVAHU
  - LUCNÍ SMĚS
  - VÝSADBA KEŘŮ PLOŠNĚ
  - VÝSADBA KEŘŮ V PÁSECH
  - VÝSADBA LISTNATÝCH STROMŮ
  - VÝSADBA JEHLIČNATÝCH STROMŮ
  - POPIŇAVÉ ROSTLINY
- Vegetační úpravy ostatních správů
- ZATRAVNĚNÍ
  - VÝSADBA KEŘŮ PLOŠNĚ
  - VÝSADBA KEŘŮ V PÁSECH
  - VÝSADBA STROMŮ

Souřadnicový systém: S-JTSK  
Výškový systém: Bpv

SO 801 Vegetační úpravy

Objednatel:



Ředitelství silnic a dálnic s. p.  
Čerčanská 2023/12, Krč, 140 00 Praha 4

Zhotovitel:



Valbek, spol. s r.o.  
Vaňurova 505/17  
460 07 Liberec 3

HIP:

ING. T. KLIMENT




Ing. S. SOKOLÁŘOVÁ  
Ing. S. SOKOLÁŘOVÁ  
Ing. K. TUŠEROVÁ  
I/16 MLADÁ BOLESLAV - MARTINOVICE

Zak. číslo  
Datum  
Stupeň  
Počet formátů  
Měřítko  
Č. přílohy

21-LH3-001  
02/2025  
PDPs  
7 x A4  
1 : 1000  
Paré

Zhotovitel:

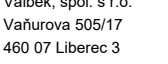

Valbek, spol. s r.o.  
Vaňurova 505/17  
460 07 Liberec 3

Příloha

SITUACE km 0,0-1,2

2