


I/16 MLADÁ BOLESLAV - MARTINOVICE
SO 801 VEGETAČNÍ ÚPRAVY
SITUACE km 1,2 - 2,2 M 1:1 000

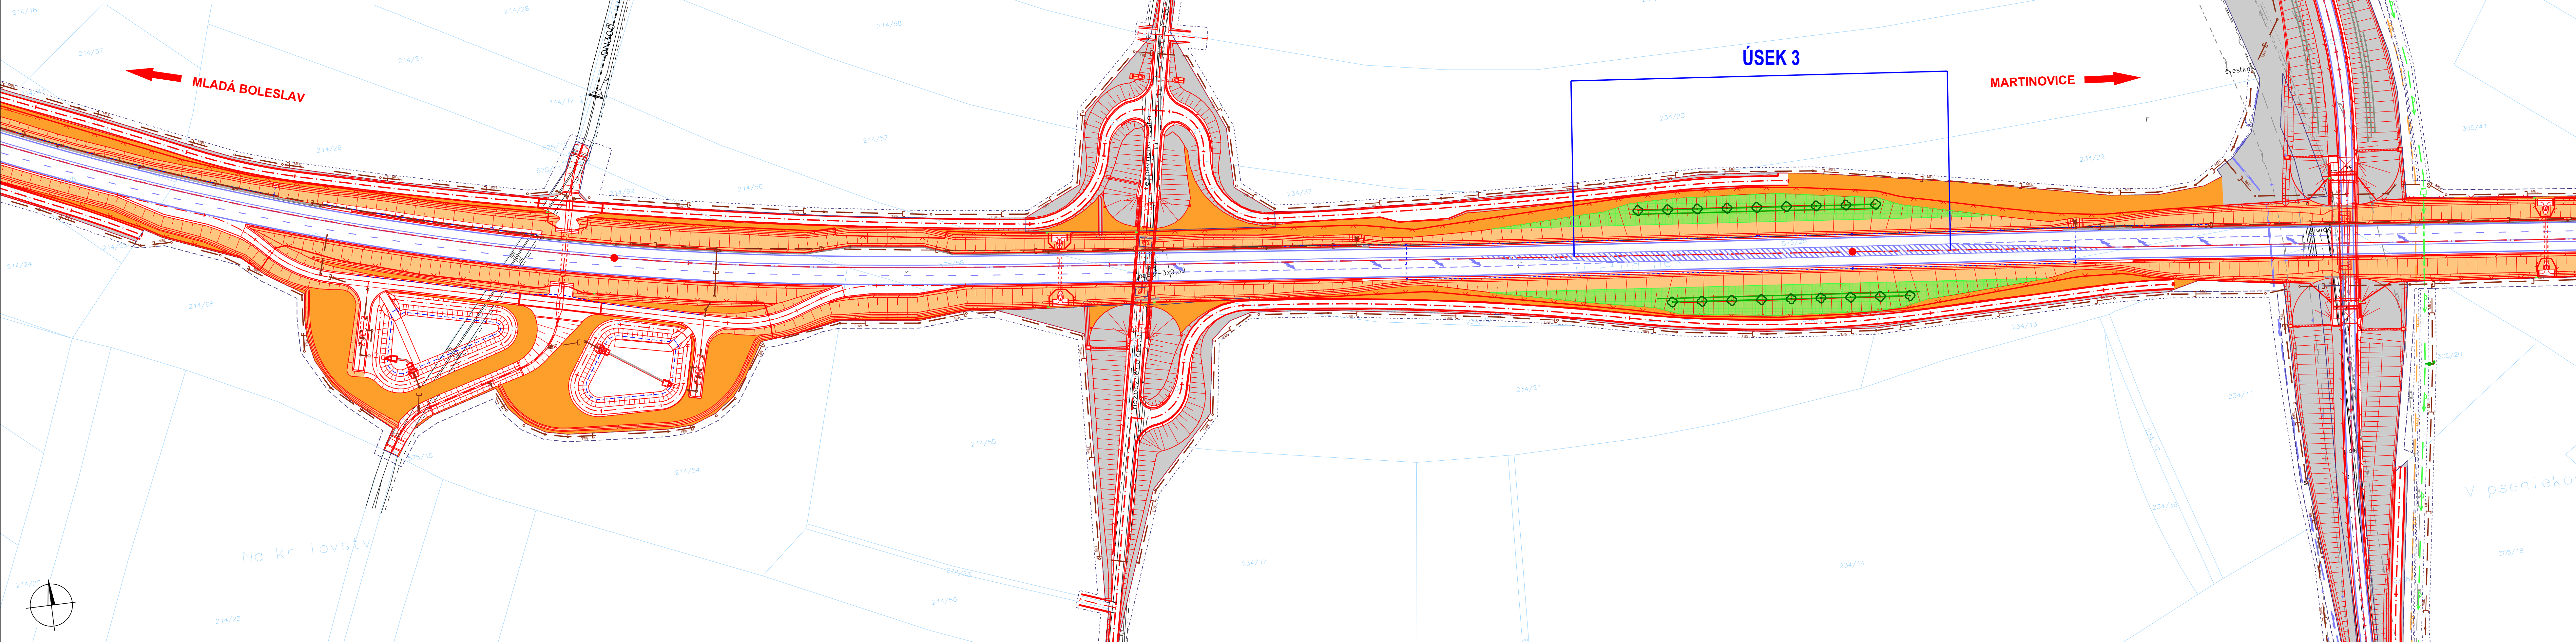

- LEGENDA
- Vegetační úpravy ve správné RSD
- ZATRAVNĚNÍ V ROVINĚ
 - ZATRAVNĚNÍ VE SVAHU
 - LUČNÍ SMĚS
 - VÝSADBA KEŘŮ PLOŠNĚ
 - VÝSADBA KEŘŮ V PÁSECH
 - VÝSADBA LISTNATÝCH STROMŮ
 - VÝSADBA JEHLIČNATÝCH STROMŮ
 - POPINÁVÉ ROSTLINY
 - Vegetační úpravy ostatních správců
 - ZATRAVNĚNÍ
 - VÝSADBA KEŘŮ PLOŠNĚ
 - VÝSADBA KEŘŮ V PÁSECH
 - VÝSADBA STROMŮ

Souřadnicový systém: S-JTSK
Výškový systém: Bpv

SO 801 Vegetační úpravy

Objednatel:

**ŘEDITELSTVÍ
SILNIC
A DÁLNIC**

Ředitelství silnic a dálnic s. p.
Čerčanská 2023/12, Krč, 140 00 Praha 4

Zhotovitel:	Valbek, spol. s r.o. Vaňurova 505/17 460 07 Liberec 3	HIP:
		ING. T. KLIMENT

	Vypracoval	ING. Š. SOKOLÁŘOVÁ	Zak. číslo	21-L113-001
	Zodp. projektant	ING. Š. SOKOLÁŘOVÁ	Datum	02/2025
	Tech. kontrola	ING. K. TUŠEROVÁ	Stupeň	PDPS
	I/16 MLADÁ BOLESLAV - MARTINOVICE		Počet formátů	6 x A4
			Měřítko	1 : 1000
Zhotovitel:	Příloha		Č. přílohy	Paré
Valbek, spol. s r.o. Vaňurova 505/17 460 07 Liberec 3			3	
	SITUACE km 1,2-2,2			