


I/16 MLADÁ BOLESLAV - MARTINOVICE
SO 801 VEGETAČNÍ ÚPRAVY
SITUACE km 2,2 - 3,2 M 1:1 000

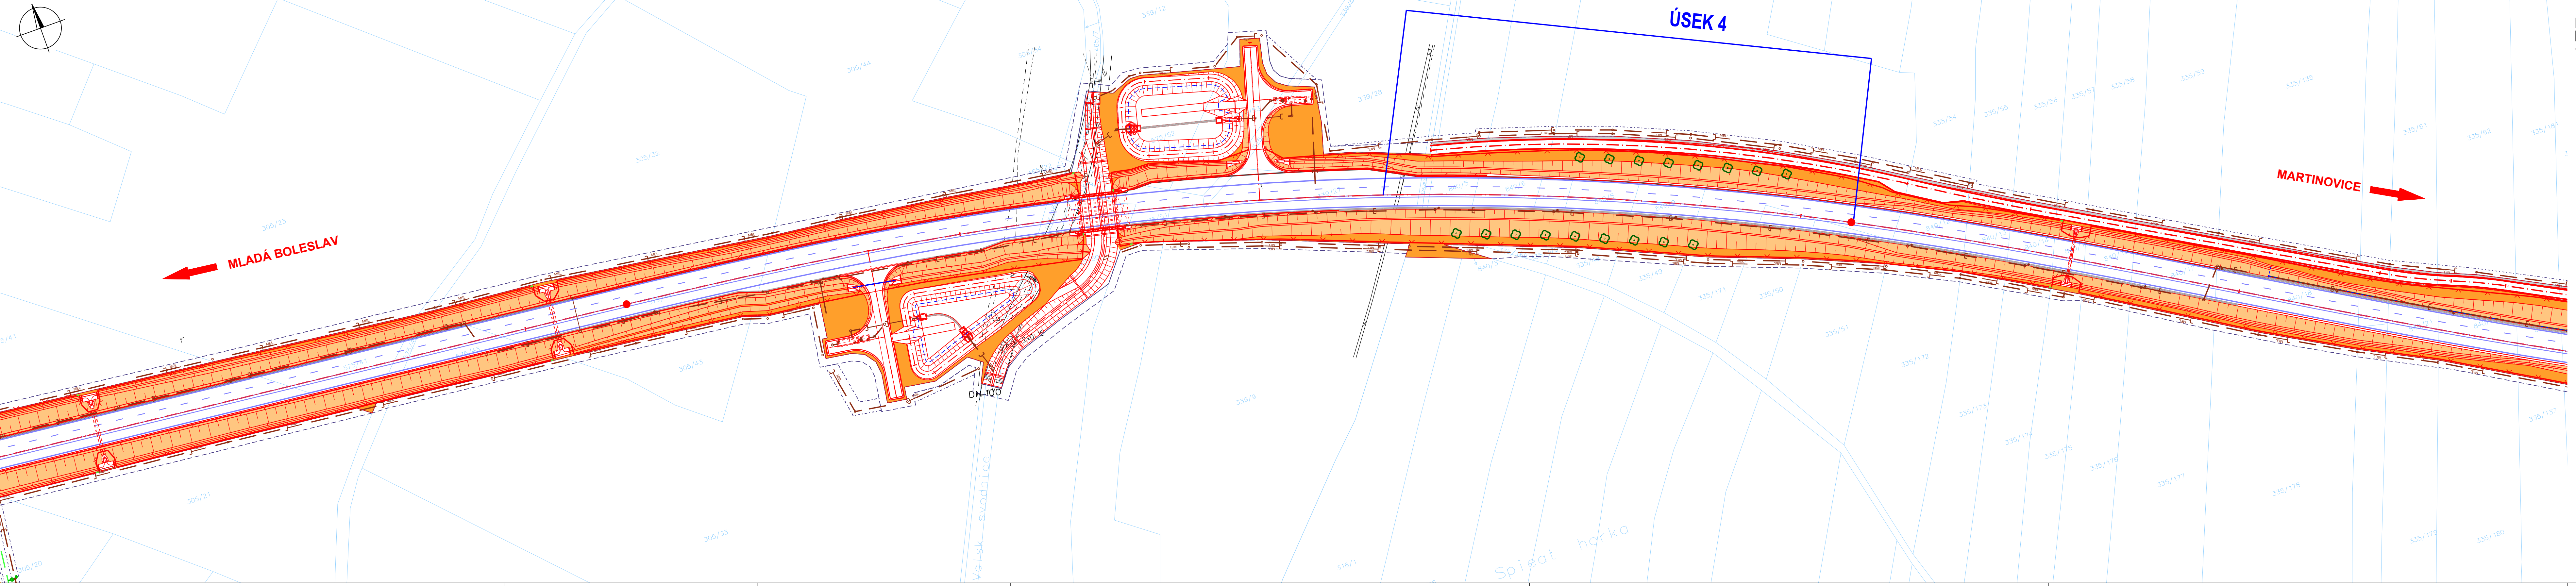

- LEGENDA
- Vegetační úpravy ve správné RSD
- ZATRAVNĚNÍ V ROVINĚ
 - ZATRAVNĚNÍ VE SVAHU
 - LUČNÍ SMĚS
 - VÝSADBA KERŮ PLOŠNĚ
 - VÝSADBA KERŮ V PÁSECH
 - VÝSADBA LISTNATÝCH STROMŮ
 - VÝSADBA JEHLIČNATÝCH STROMŮ
 - POPÍNAVÉ ROSTLINY
 - Vegetační úpravy ostatních správců
 - ZATRAVNĚNÍ
 - VÝSADBA KERŮ PLOŠNĚ
 - VÝSADBA KERŮ V PÁSECH
 - VÝSADBA STROMŮ

Souřadnicový systém: S-JTSK
Výškový systém: Bpv

SO 801 Vegetační úpravy

Objednatel:



**ŘEDITELSTVÍ
SILNIC
A DÁLNIC**

Ředitelství silnic a dálnic s. p.
Čerčanská 2023/12, Krč, 140 00 Praha 4

Zhotovitel:	 Valbek	Valbek, spol. s r.o. Vaňurova 505/17 460 07 Liberec 3	HIP: ING. T. KLIMENT
-------------	---	--	-------------------------

 Valbek	Vypracoval	ING. Š. SOKOLÁŘOVÁ	Zak. číslo	21-LI13-001
	Zdp. projektant	ING. Š. SOKOLÁŘOVÁ	Datum	02/2025
	Tech. kontrola	ING. K. TUŠEROVÁ	Stupeň	PDPS
	Akce I/16 MLADÁ BOLESLAV - MARTINOVICE		Počet formátů	6 x A4
			Měřítko	1 : 1000
Zhotovitel: Valbek, spol. s r.o. Vaňurova 505/17 460 07 Liberec 3	Příloha	SITUACE km 2,2-3,2		Č. přílohy 4