


I/16 MLADÁ BOLESLAV - MARTINOVICE
SO 801 VEGETAČNÍ ÚPRAVY
SITUACE km 3,2 - 4,3 M 1:1 000

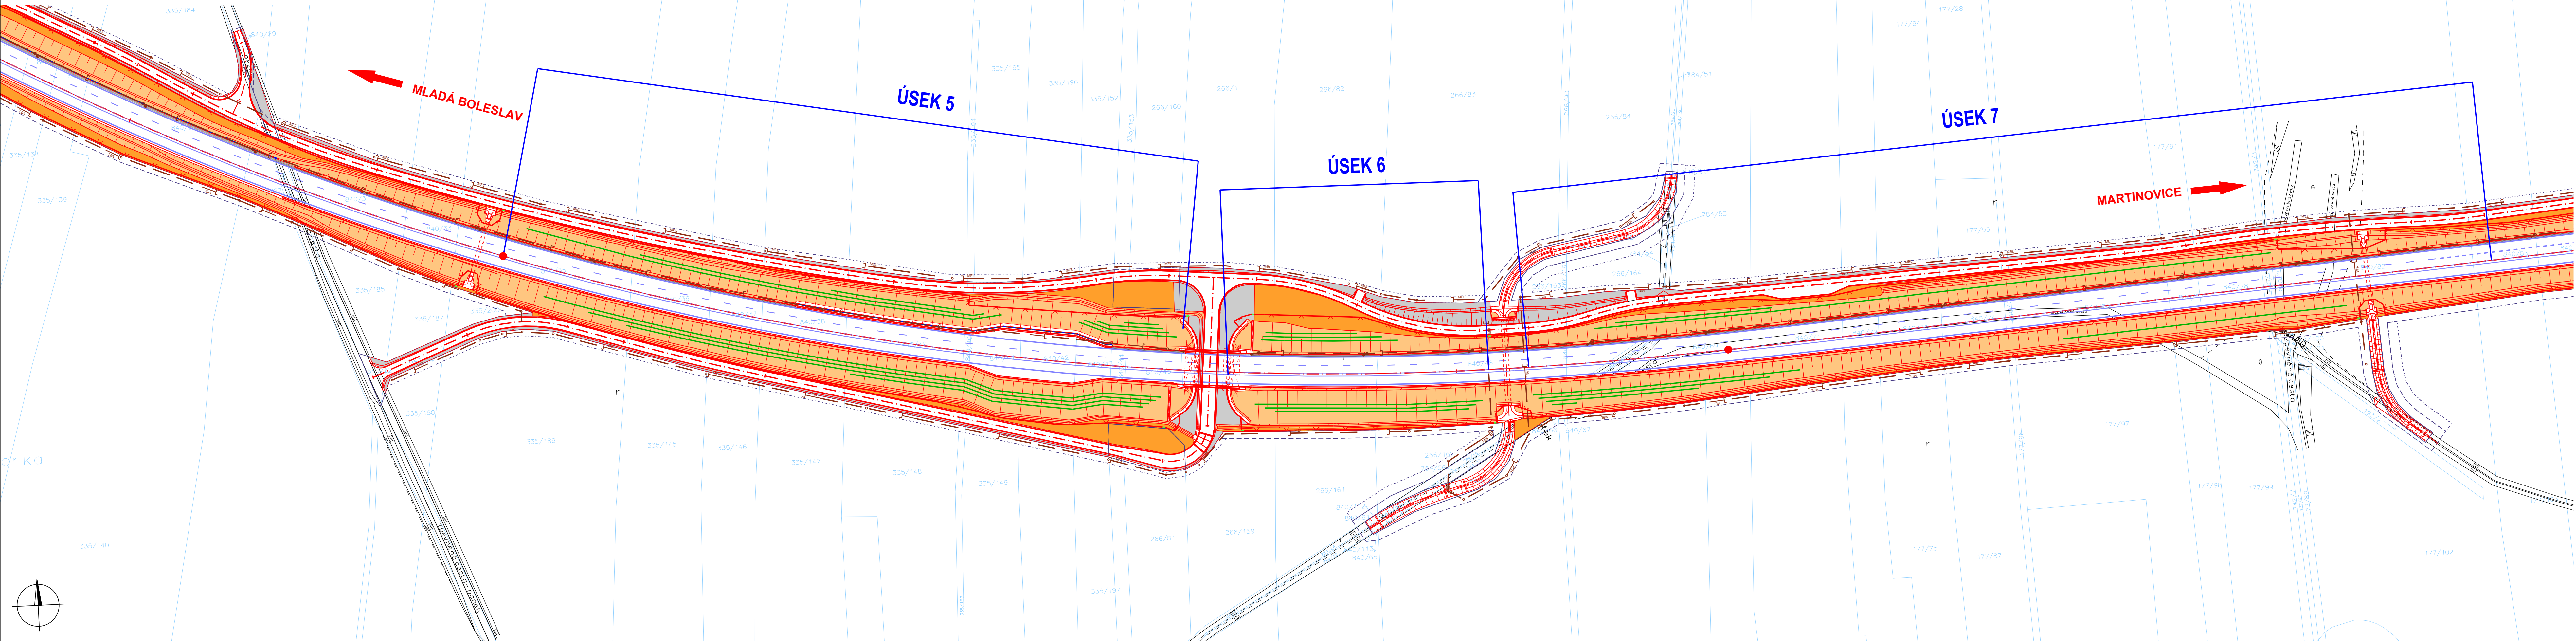

- LEGENDA
- Vegetační úpravy ve správné RSD
- ZATRAVNĚNÍ V ROVINĚ
 - ZATRAVNĚNÍ VE SVAHU
 - LUČNÍ SMĚS
 - VÝSADBA KEŘŮ PLOŠNĚ
 - VÝSADBA KEŘŮ V PÁSECH
 - VÝSADBA LISTNATÝCH STROMŮ
 - VÝSADBA JEHLIČNATÝCH STROMŮ
 - POPÍNAVÉ ROSTLINY
- Vegetační úpravy ostatních správců
- ZATRAVNĚNÍ
 - VÝSADBA KEŘŮ PLOŠNĚ
 - VÝSADBA KEŘŮ V PÁSECH
 - VÝSADBA STROMŮ

Souřadnicový systém: S-JTSK
Výškový systém: Bpv

SO 801 Vegetační úpravy

Objednatel:



Ředitelství silnic a dálnic s. p.
Čerčanská 2023/12, Krč, 140 00 Praha 4

Zhotovitel:



Valbek, spol. s r.o.
Vaňurova 505/17
460 07 Liberec 3

HIP:

ING. T. KLIMENT



Vypracoval: ING. Š. SOKOLÁŘOVÁ
Zodp. projektant: ING. Š. SOKOLÁŘOVÁ
Tech. kontrola: ING. K. TUŠEROVÁ
Akce: I/16 MLADÁ BOLESLAV - MARTINOVICE

Zak. číslo: 21-L113-001
Datum: 02/2025
Stupeň: PDPS
Počet formátů: 6 x A4
Měřítko: 1 : 1000
Č. přílohy: Paré

Zhotovitel:

Valbek, spol. s r.o.
Vaňurova 505/17
460 07 Liberec 3

Příloha

SITUACE km 3,2-4,3

5