


I/16 MLADÁ BOLESLAV - MARTINOVICE
SO 801 VEGETAČNÍ ÚPRAVY
SITUACE km 4,3 - 5,3 M 1:1 000

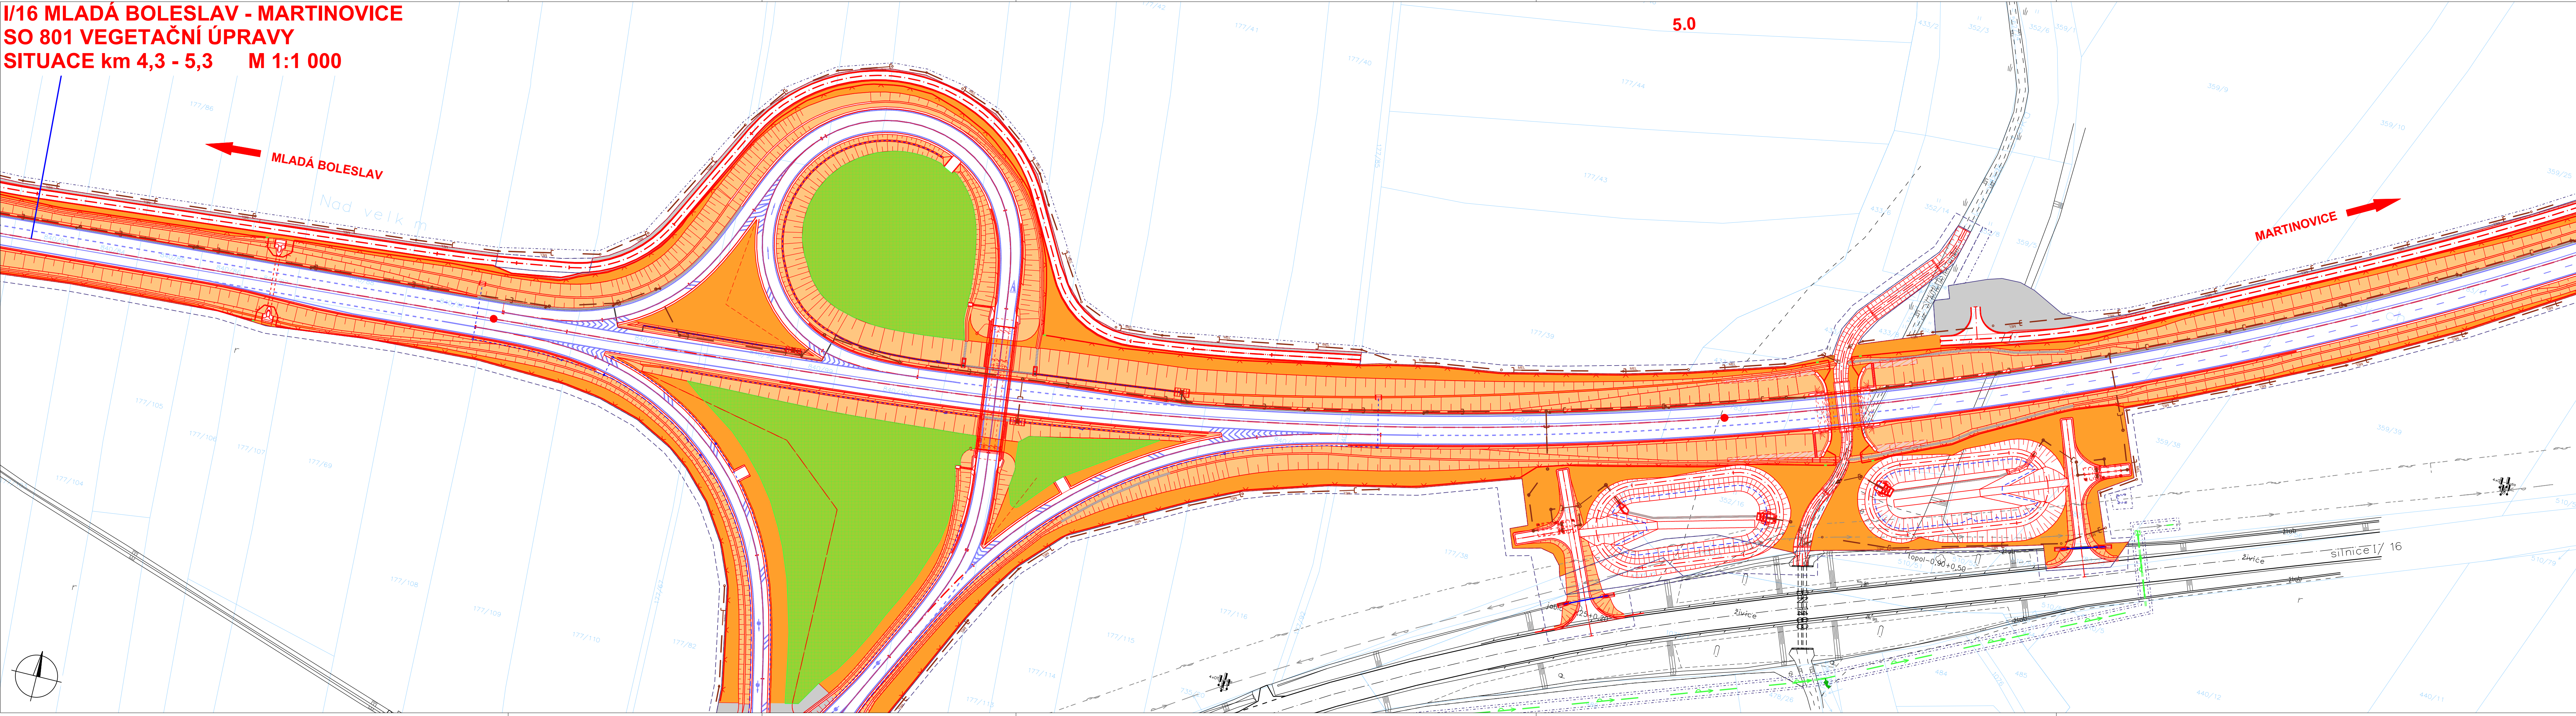

- LEGENDA
- Vegetační úpravy ve správné RSD
 - ZATRAVNĚNÍ V ROVINĚ
 - ZATRAVNĚNÍ VE SVAHU
 - LUČNÍ SMĚS
 - VÝSADBA KEŘŮ PLOŠNĚ
 - VÝSADBA KEŘŮ V PÁSECH
 - VÝSADBA LISTNATÝCH STROMŮ
 - VÝSADBA JEHLIČNATÝCH STROMŮ
 - POPIŇAVÉ ROSTLINY
 - Vegetační úpravy ostatních správců
 - ZATRAVNĚNÍ
 - VÝSADBA KEŘŮ PLOŠNĚ
 - VÝSADBA KEŘŮ V PÁSECH
 - VÝSADBA STROMŮ

Souřadnicový systém: S-JTSK
Výškový systém: Bpv

SO 801 Vegetační úpravy

Objednatel:



**ŘEDITELSTVÍ
SILNIC
A DÁLNIC**

Ředitelství silnic a dálnic s. p.
Čerčanská 2023/12, Krč, 140 00 Praha 4

Zhotovitel:



Valbek

Valbek, spol. s r.o.
Vaňurova 505/17
460 07 Liberec 3

HIP:

ING. T. KLIMENT

	Vypracoval	ING. Š. SOKOLÁŘOVÁ	<i>JSK</i>	Zak. číslo	21-LI13-001
	Zodp. projektant	ING. Š. SOKOLÁŘOVÁ	<i>JSK</i>	Datum	02/2025
	Tech. kontrola	ING. K. TUŠEROVÁ	<i>TuŠ</i>	Stupeň	PDPS
	Akce	I/16 MLADÁ BOLESLAV - MARTINOVICE			Počet formátů
Zhotovitel: Valbek, spol. s r.o. Václavova 505/17 480 07 Liberec 3	Příloha	SITUACE km 4,3-5,3		Měřítko	1 : 1000
				Č. přílohy	Paré
				6	