


I/16 MLADÁ BOLESLAV - MARTINOVICE
SO 801 VEGETAČNÍ ÚPRAVY
SITUACE SO 125 M 1:1 000

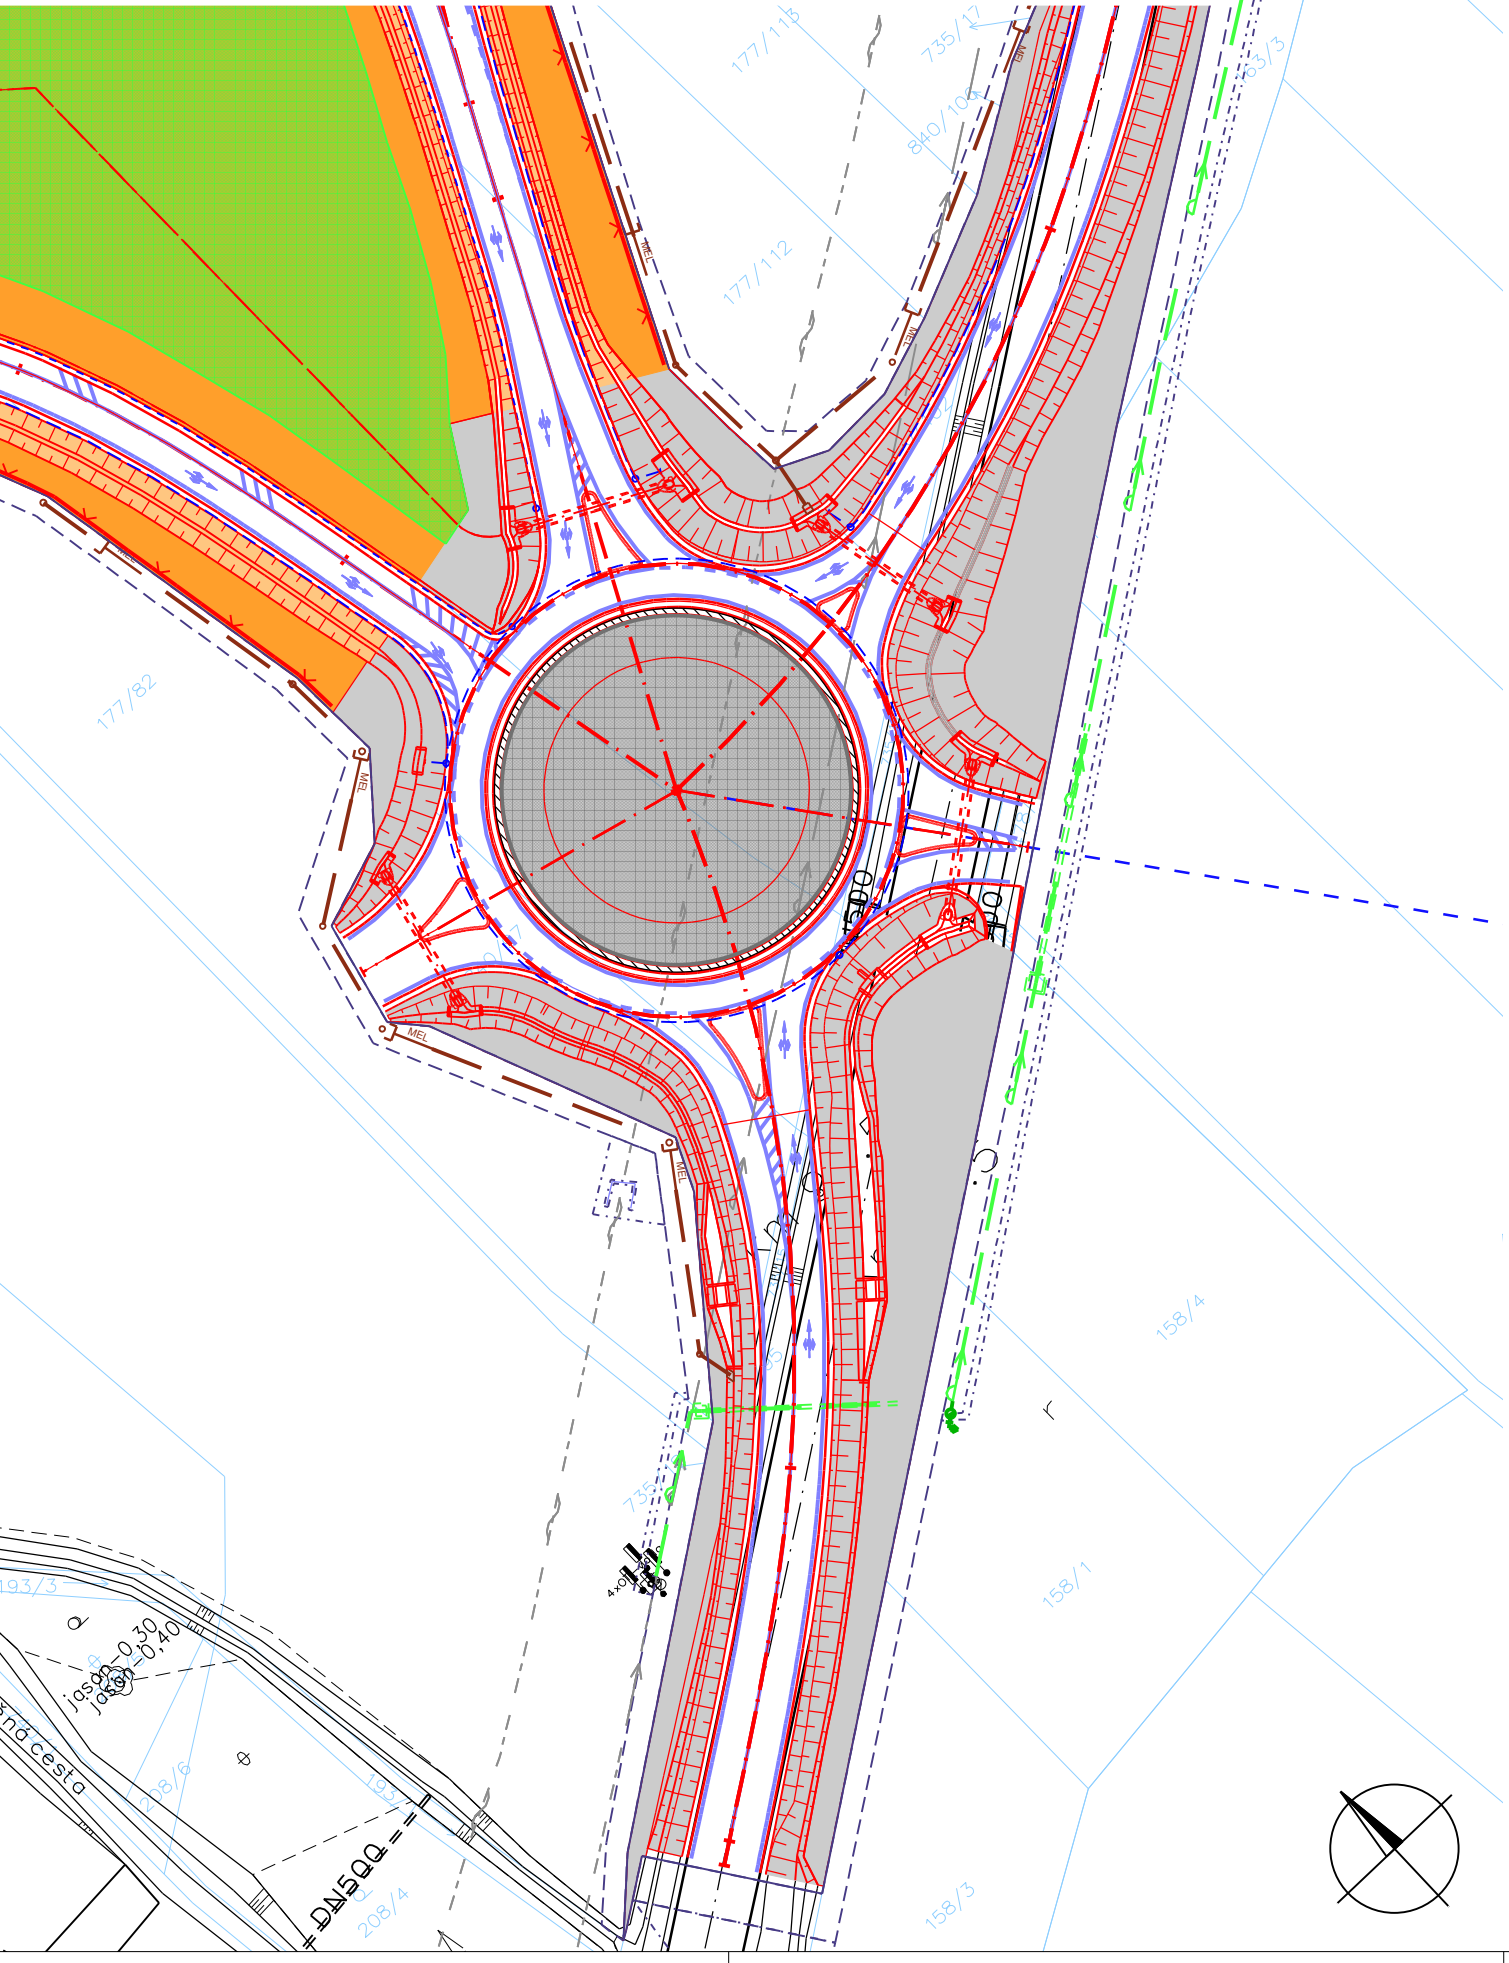

- LEGENDA
- Vegetační úpravy ve správně ŘSD
- ZATRAVNĚNÍ V ROVINĚ
 - ZATRAVNĚNÍ VE SVAHU
 - LUČNÍ SMĚS
 - VÝSADBA KEŘŮ PLOŠNĚ
 - VÝSADBA KEŘŮ V PÁSECH
 - VÝSADBA LISTNATÝCH STROMŮ
 - VÝSADBA JEHLIČNATÝCH STROMŮ
 - POPÍNAVÉ ROSTLINY
- Vegetační úpravy ostatních správců
- ZATRAVNĚNÍ
 - VÝSADBA KEŘŮ PLOŠNĚ
 - VÝSADBA KEŘŮ V PÁSECH
 - VÝSADBA STROMŮ

Souřadnicový systém: S-JTSK
Výškový systém: Bpv

SO 801 Vegetační úpravy

Objednatel:



**ŘEDITELSTVÍ
SILNIC
A DÁLNIC**

Ředitelství silnic a dálnic s. p.
Čerčanská 2023/12, Krč, 140 00 Praha 4

Zhotovitel: 	Valbek, spol. s r.o. Vaňurova 505/17 460 07 Liberec 3		HIP:
			ING. T. KLIMENT

	Vypracoval	ING. Š. SOKOLÁŘOVÁ		Zak. číslo	21-LI13-001
	Zodp. projektant	ING. Š. SOKOLÁŘOVÁ		Datum	02/2025
	Tech. kontrola	ING. K. TUŠEROVÁ		Stupeň	PDPS
	Akce I/16 MLADÁ BOLESLAV - MARTINOVICE			Počet formátů	2 x A4
				Měřítko	1 : 1000
Zhotovitel: Valbek, spol. s r.o. Vaňurova 505/17 460 07 Liberec 3	Příloha SITUACE SO 125			Č. přílohy	Paré
				7	