


**I/16 MLADÁ BOLESLAV - MARTINOVICE
SO 801 VEGETAČNÍ ÚPRAVY
SITUACE km 6,4 - 7,5 M 1:1 000**

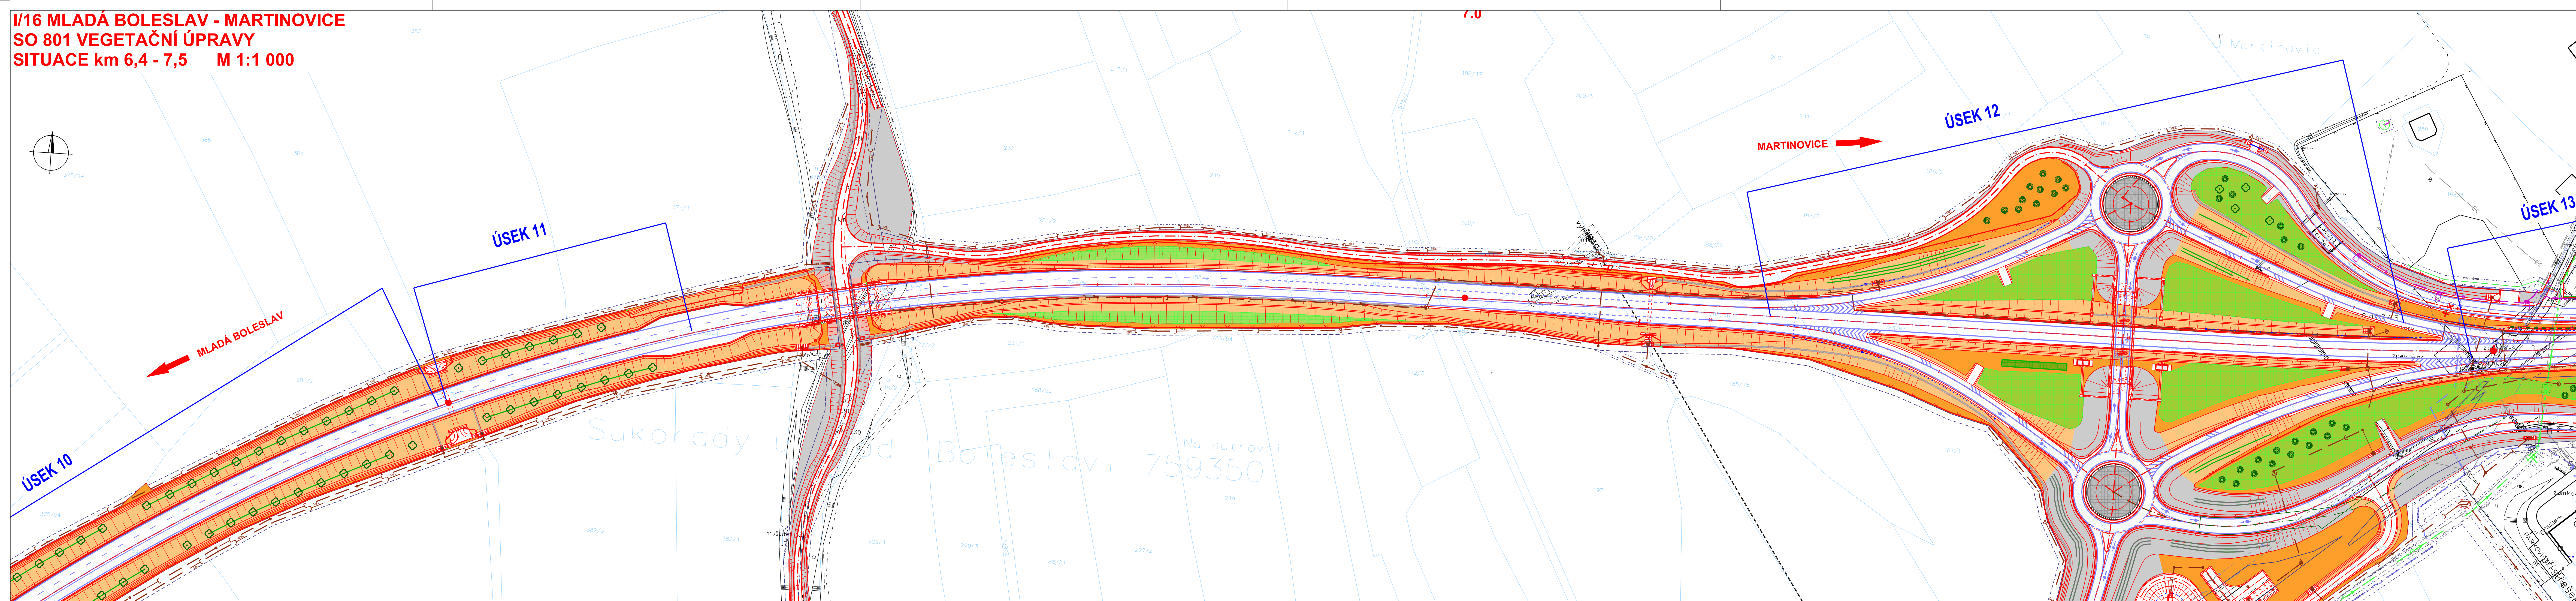

LEGENDA

Vegetační úpravy ve správné ŘSD

-  ZATRAVNĚNÍ V ROVINĚ
-  ZATRAVNĚNÍ VE SVAHU
-  LUČNÍ SMĚS
-  VÝSADBA KERŮ PLOŠNĚ
-  VÝSADBA KERŮ V PÁSEČ
-  VÝSADBA LISTNATÝCH STROMŮ
-  VÝSADBA JEHLIČNATÝCH STROMŮ
-  POPLINAVÉ ROSTLINY

Vegetační úpravy ostatních správců

-  ZATRAVNĚNÍ
-  VÝSADBA KERŮ PLOŠNĚ
-  VÝSADBA KERŮ V PÁSEČ
-  VÝSADBA STROMŮ

Souřadnicový systém: S-JTSK
Výškový systém: Bpv

SO 801 Vegetační úpravy

Objednatel



Ředitelství silnic a dálnic s. p.
Čerčanská 2023/12, Krč, 140 00 Praha 4

Zhotovitel:



Valbek, spol. s r.o.
Vaňurova 505/17
460 07 Liberec 3

	HIP
--	-----

ING. T. KLIMEN



Vypracoval	ING. Š. SOKOLÁŘOVÁ	<i>JS</i>
Zodp. projektant	ING. Š. SOKOLÁŘOVÁ	<i>JS</i>
Tech. kontrola	ING. K. TUŠEROVÁ	<i>Tu</i>
Akce		
I/16 MLADÁ BOLESLAV - MARTINOV		

Zhotovitel:
Valbek, spol. s r.o.
Vaňurova 505/17
460 07 Liberec 3

Příloha	SITUACE km 6,4-7,5
---------	--------------------

--	--

9