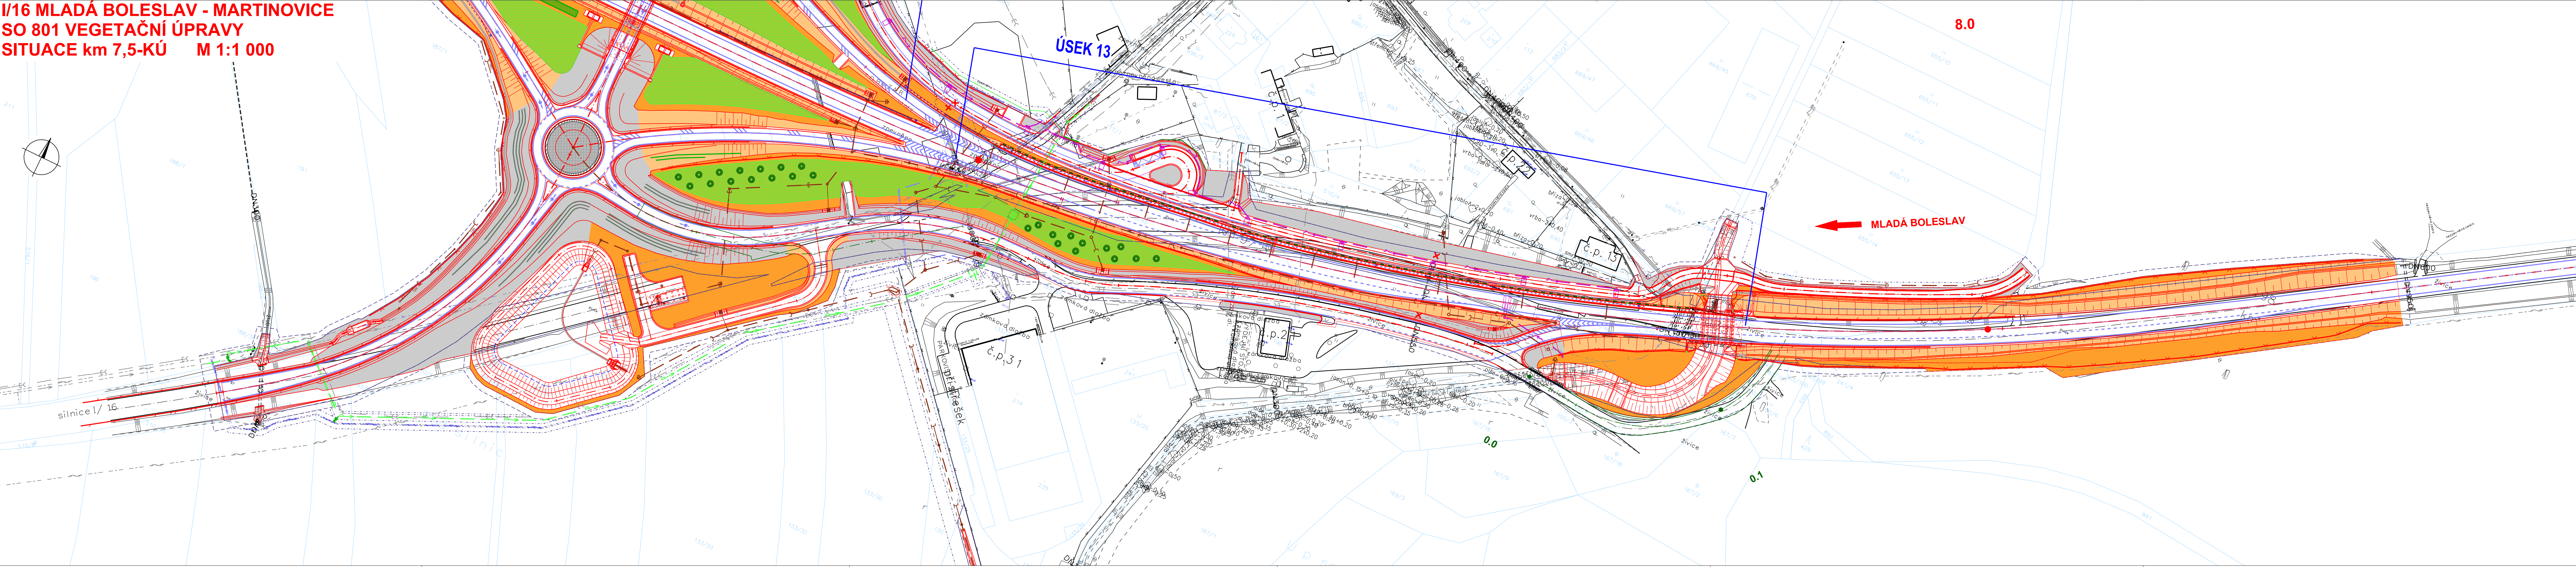


I/16 MLADÁ BOLESLAV - MARTINOVICE
SO 801 VEGETAČNÍ ÚPRAVY
SITUACE km 7,5-KÚ M 1:1 000



LEGENDA

Vegetační úpravy ve správně ŘSD

ZATRAVNĚNÍ V ROVINĚ

ZATRAVNĚNÍ VE SVAHU

LÚČNÍ SMĚS

VÝSADBA KEŘŮ PLOŠNĚ

VÝSADBA KEŘŮ V PÁSECH

VÝSADBA LISTNATÝCH STROMŮ

VÝSADBA JEHLIČNATÝCH STROMŮ

POPINÁVÉ ROSTLINY

Vegetační úpravy ostatních správců

ZATRAVNĚNÍ

VÝSADBA KEŘŮ PLOŠNĚ

VÝSADBA KEŘŮ V PÁSECH

VÝSADBA STROMŮ

Souřadnicový systém: S-JTSK
Výškový systém: Bpv

SO 801 Vegetační úpravy

Objednatel:



Ředitelství
silnic
a dálnic

Ředitelství silnic a dálnic s. p.
Čerčanská 2023/12, Krč, 140 00 Praha 4

Zhotovitel:

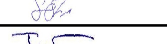
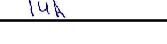


Valbek

Valbek, spol. s r.o.
Vaňurova 505/17
460 07 Liberec 3

HIP:

ING. T. KLIMENT

 Valbek	Vypracoval	ING. Š. SOKOLÁŘOVÁ		Zak. číslo	21-L113-001
	Zodp. projektant	ING. Š. SOKOLÁŘOVÁ		Datum	02/2025
	Tech. kontrola	ING. K. TUŠEROVÁ		Stupeň	PDPS
	Akce	I/16 MLADÁ BOLESLAV - MARTINOVICE		Počet formátů	7 x A4
Zhotovitel: Valbek, spol. s r.o. Vaňurova 505/17 460 07 Liberec 3	Příloha		SITUACE km 7,5-KÚ	Mřítko	1 : 1000
				Č. přílohy	Paré
				10	