


I/16 MLADÁ BOLESLAV - MARTINOVICE
SO 830 Rekultivace ploch dočasného záboru
SITUACE km 2,0-2,3 M 1:2000

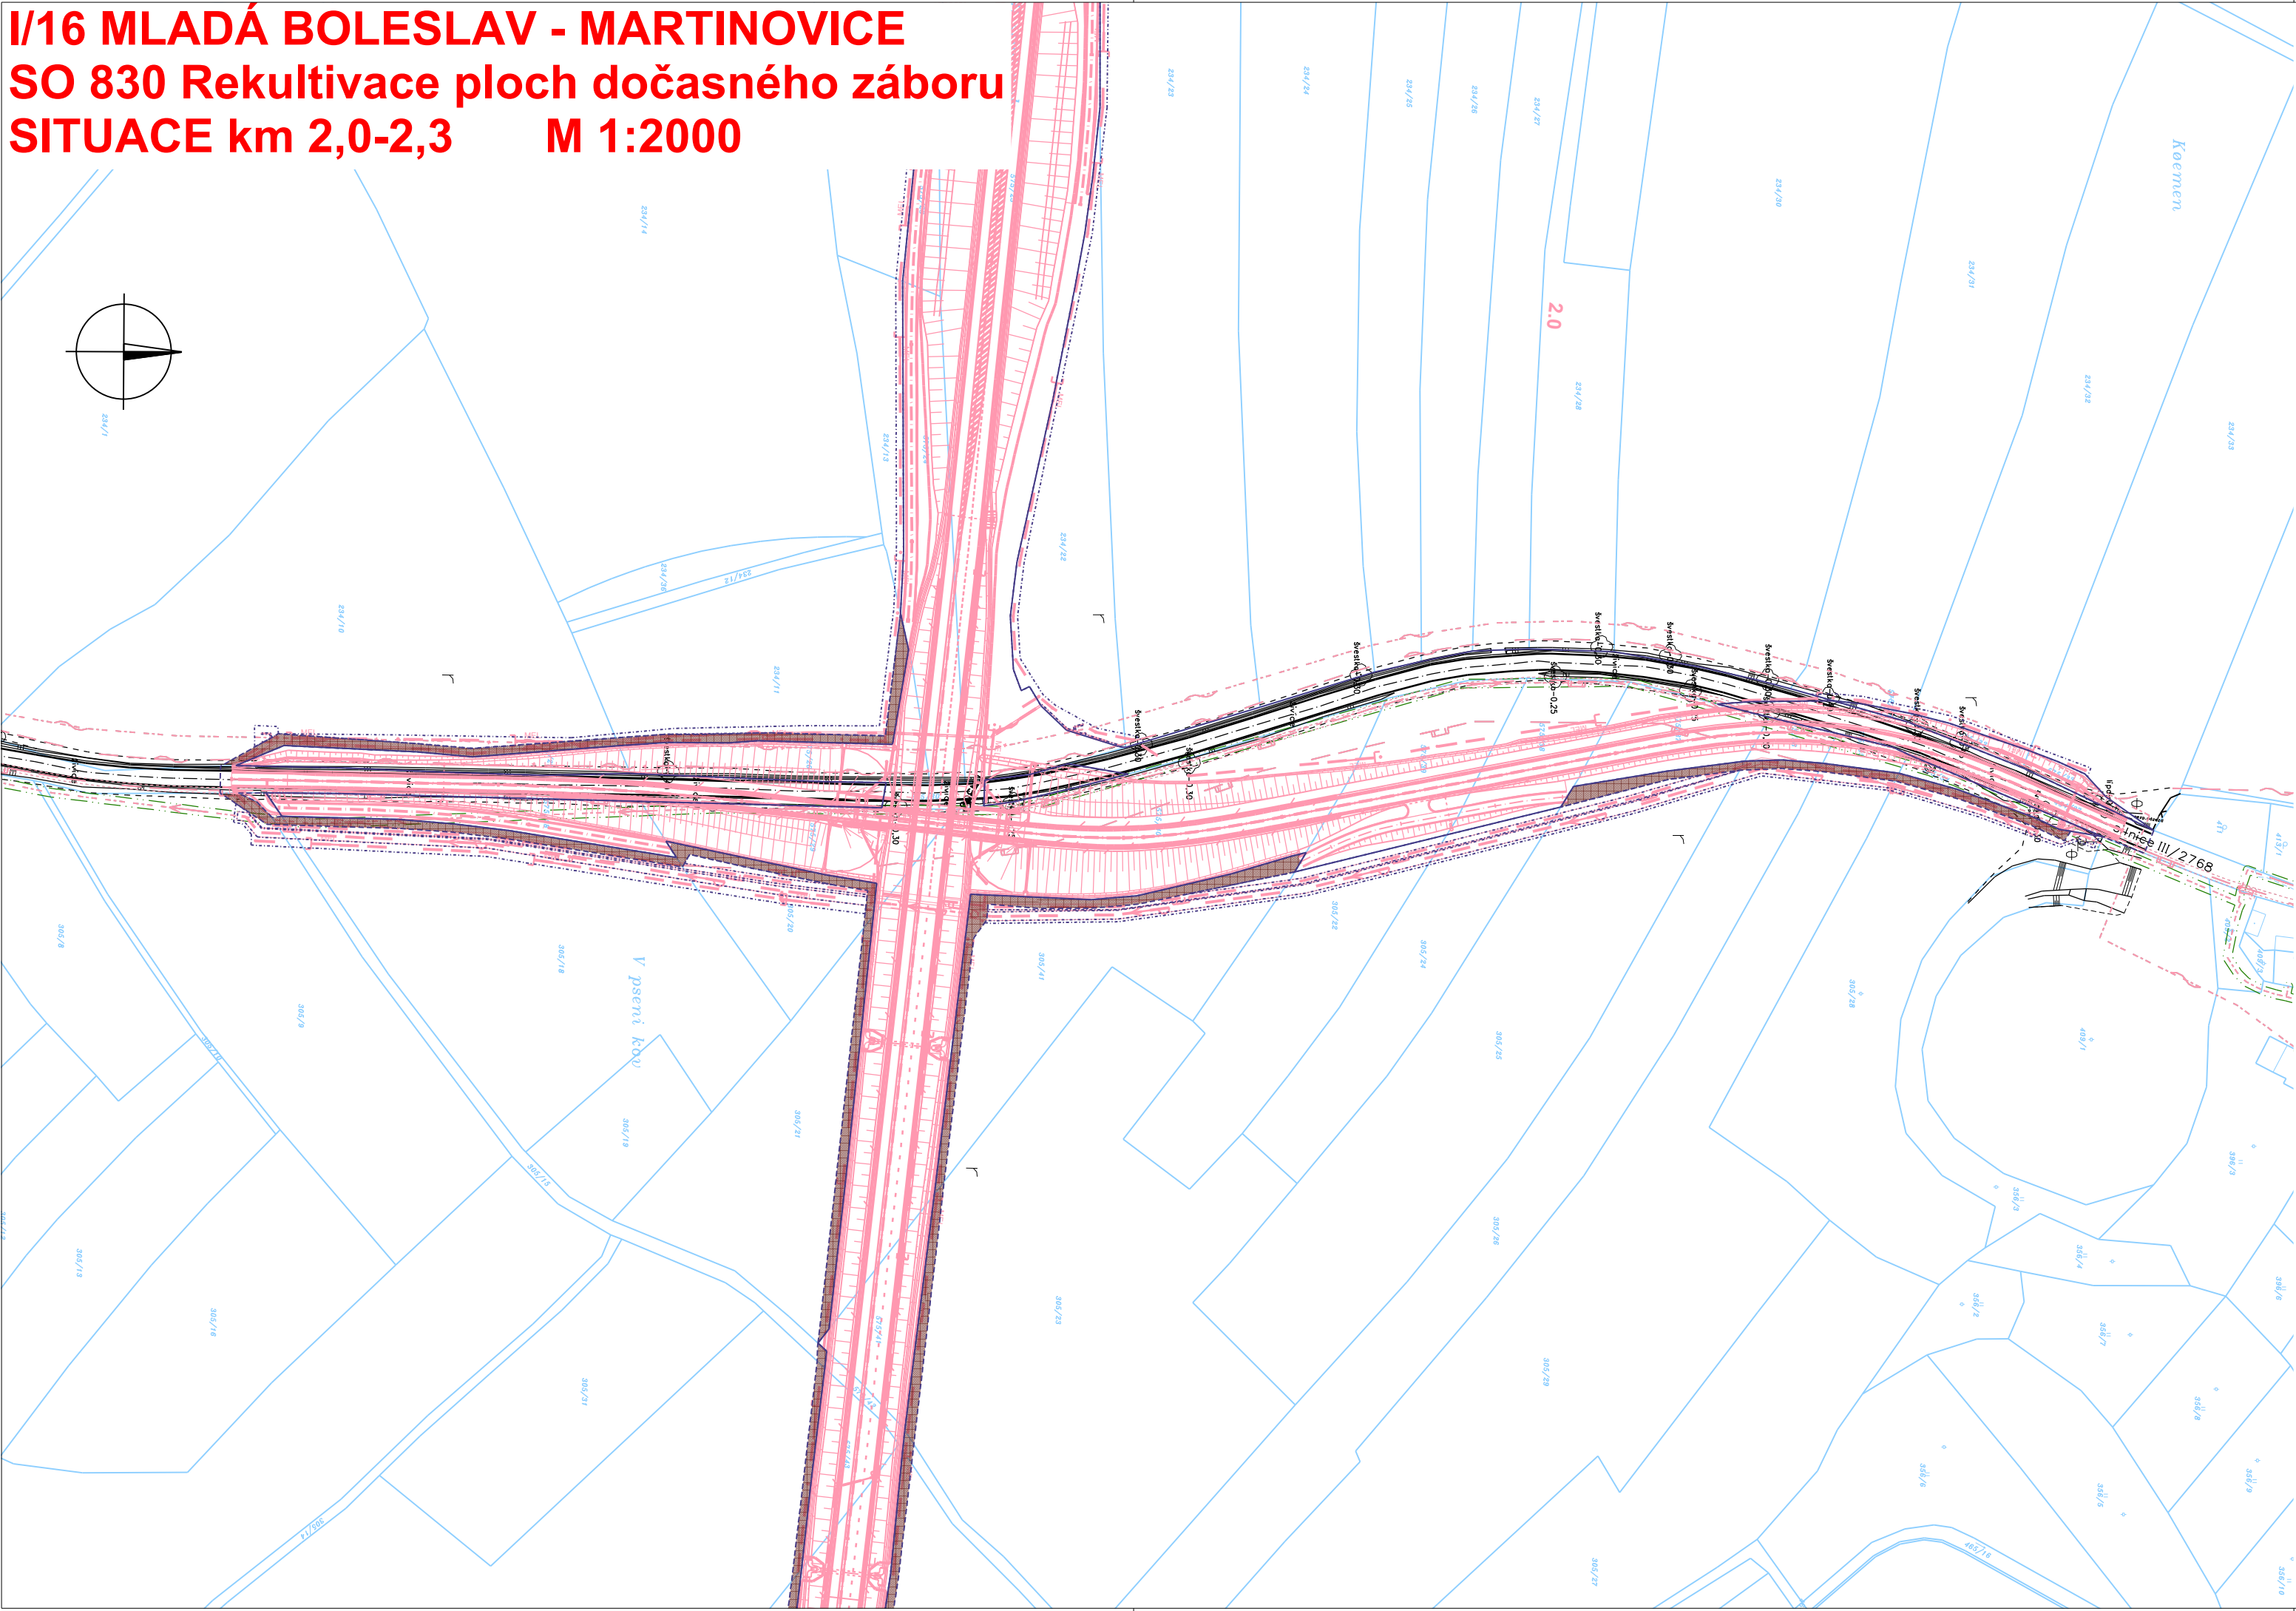

- LEGENDA
- REKULTIVACE PUPFL
 - REKULTIVACE ZPF - ORNÁ PŮDA
 - REKULTIVACE ZPF - TTP
 - REKULTIVACE ZPF - OSTATNÍ
 - REKULTIVACE OSTATNÍCH PLOCH
 - TRVALÝ ZÁBOR
 - DOČASNÝ ZÁBOR NAD 1 ROK

Souřadnicový systém: S-JTSK
Výškový systém: Bpv

SO 830 Rekultivace ploch dočasného záboru

Objednatel:



ŘEDITELSTVÍ
SILNIC
A DÁLNIC

Ředitelství silnic a dálnic s. p.

Čerčanská 2023/12, Krč, 140 00 Praha 4

Zhotovitel:



Valbek

Valbek, spol. s r.o.

Vaňurova 505/17
460 07 Liberec 3

HIP:

ING. T. KLIMENT

	Vypracoval	ING. Š. SOKOLÁŘOVÁ		Zak. číslo	21-LI13-001
	Zodp. projektant	ING. Š. SOKOLÁŘOVÁ		Datum	02/2025
	Tech. kontrola	ING. K. TUŠEROVÁ		Stupeň	PDPS
	Akce I/16 MLADÁ BOLESLAV - MARTINOVICE			Počet formátů	3 x A4
				Měřítko	1 : 2000
Zhotovitel: Valbek, spol. s r.o. Vaňurova 505/17 460 07 Liberec 3		Příloha SITUACE km 2,0-2,3		Č. přílohy 3	Paré