


I/16 MLADÁ BOLESLAV - MARTINOVICE  
SO 830 Rekultivace ploch dočasného záboru  
SITUACE km 2,3-4,5 M 1:2000

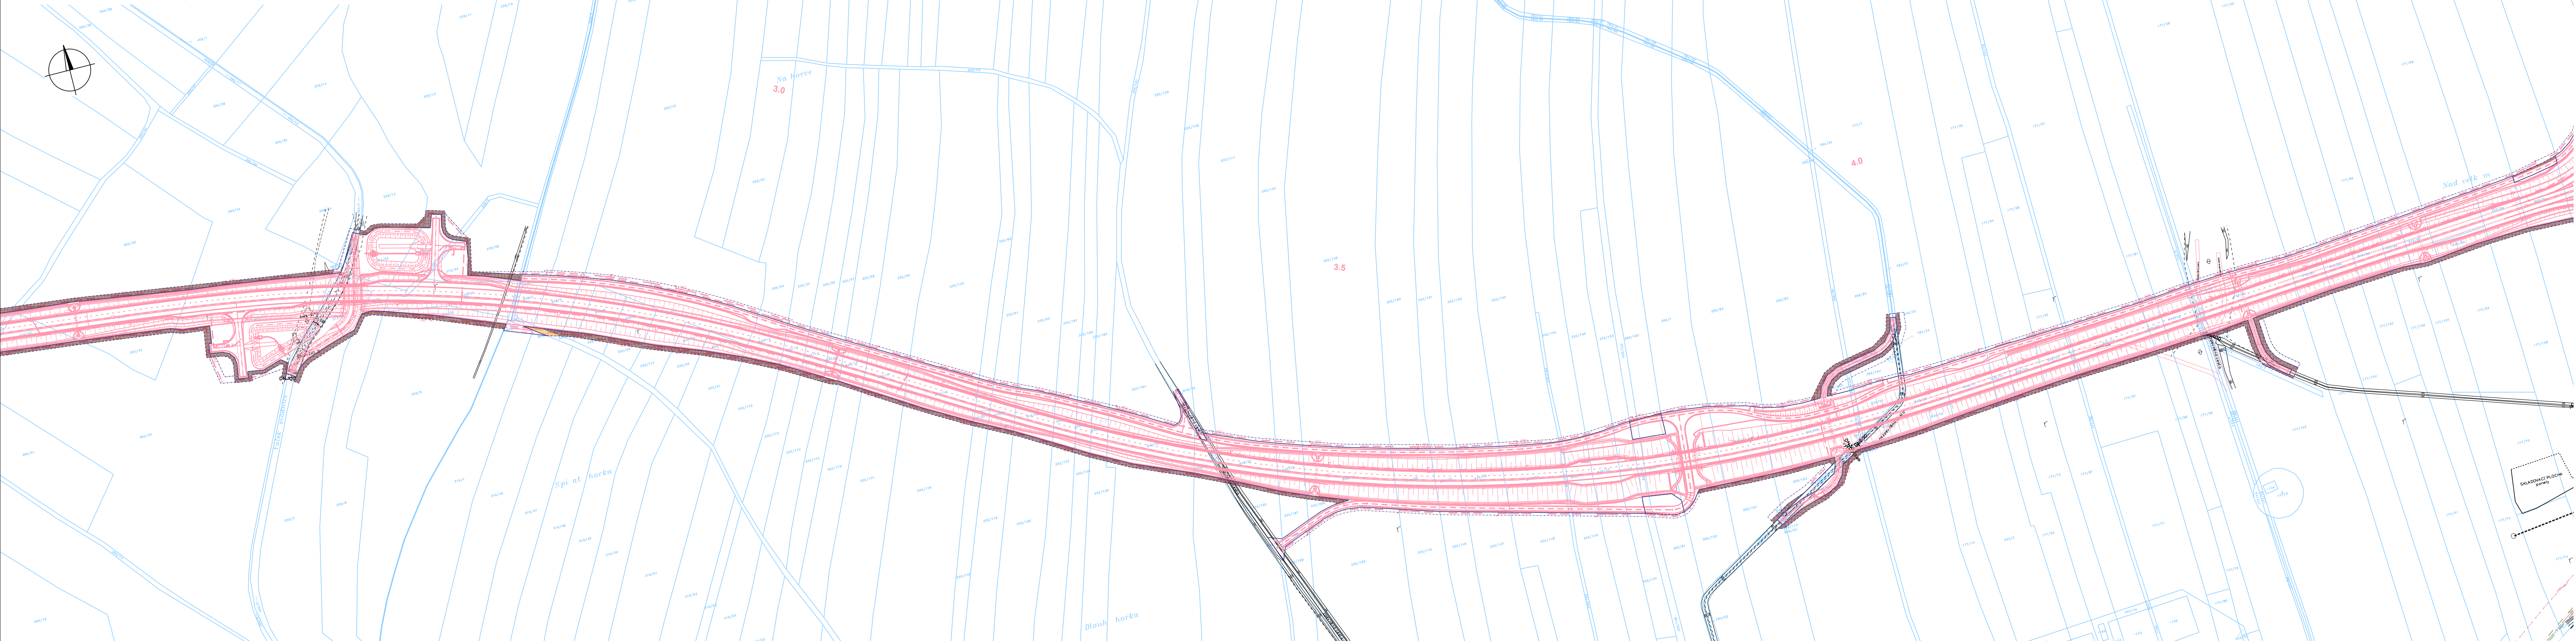

- LEGENDA
- REKULTIVACE PUPFL
  - REKULTIVACE ZPF - ORNÁ PŮDA
  - REKULTIVACE ZPF - TTP
  - REKULTIVACE ZPF - OSTATNÍ
  - REKULTIVACE OSTATNÍCH PLOCH
  - TRVALÝ ZÁBOR
  - DOČASNÝ ZÁBOR NAD 1 ROK

Souřadnicový systém: S-JTSK  
Výškový systém: Bpv

SO 830 Rekultivace ploch dočasného záboru

Objednatel:



Ředitelství silnic a dálnic s. p.  
Čerčanská 2023/12, Krč, 140 00 Praha 4

Zhotovitel:



Valbek, spol. s r.o.  
Vaňurova 505/17  
460 07 Liberec 3

HIP:

ING. T. KLIMENT



|                  |                                   |  |               |             |
|------------------|-----------------------------------|--|---------------|-------------|
| Vypracoval       | ING. Š. SOKOLÁŘOVÁ                |  | Zak. číslo    | 21-LI13-001 |
| Zodp. projektant | ING. Š. SOKOLÁŘOVÁ                |  | Datum         | 02/2025     |
| Tech. kontrola   | ING. K. TUŠEROVÁ                  |  | Stupeň        | PDPS        |
| Akce             | I/16 MLADÁ BOLESLAV - MARTINOVICE |  | Počet formátů | 6 x A4      |
|                  |                                   |  | Měřítko       | 1 : 2000    |
|                  |                                   |  | Č. přílohy    | Paré        |

Zhotovitel:

Valbek, spol. s r.o.  
Vaňurova 505/17  
460 07 Liberec 3

Příloha

SITUACE km 2,3-4,5

4