


I/16 MLADÁ BOLESLAV - MARTINOVICE
SO 830 Rekultivace ploch dočasného záboru
SITUACE km 6,5-KÚ M 1:2000

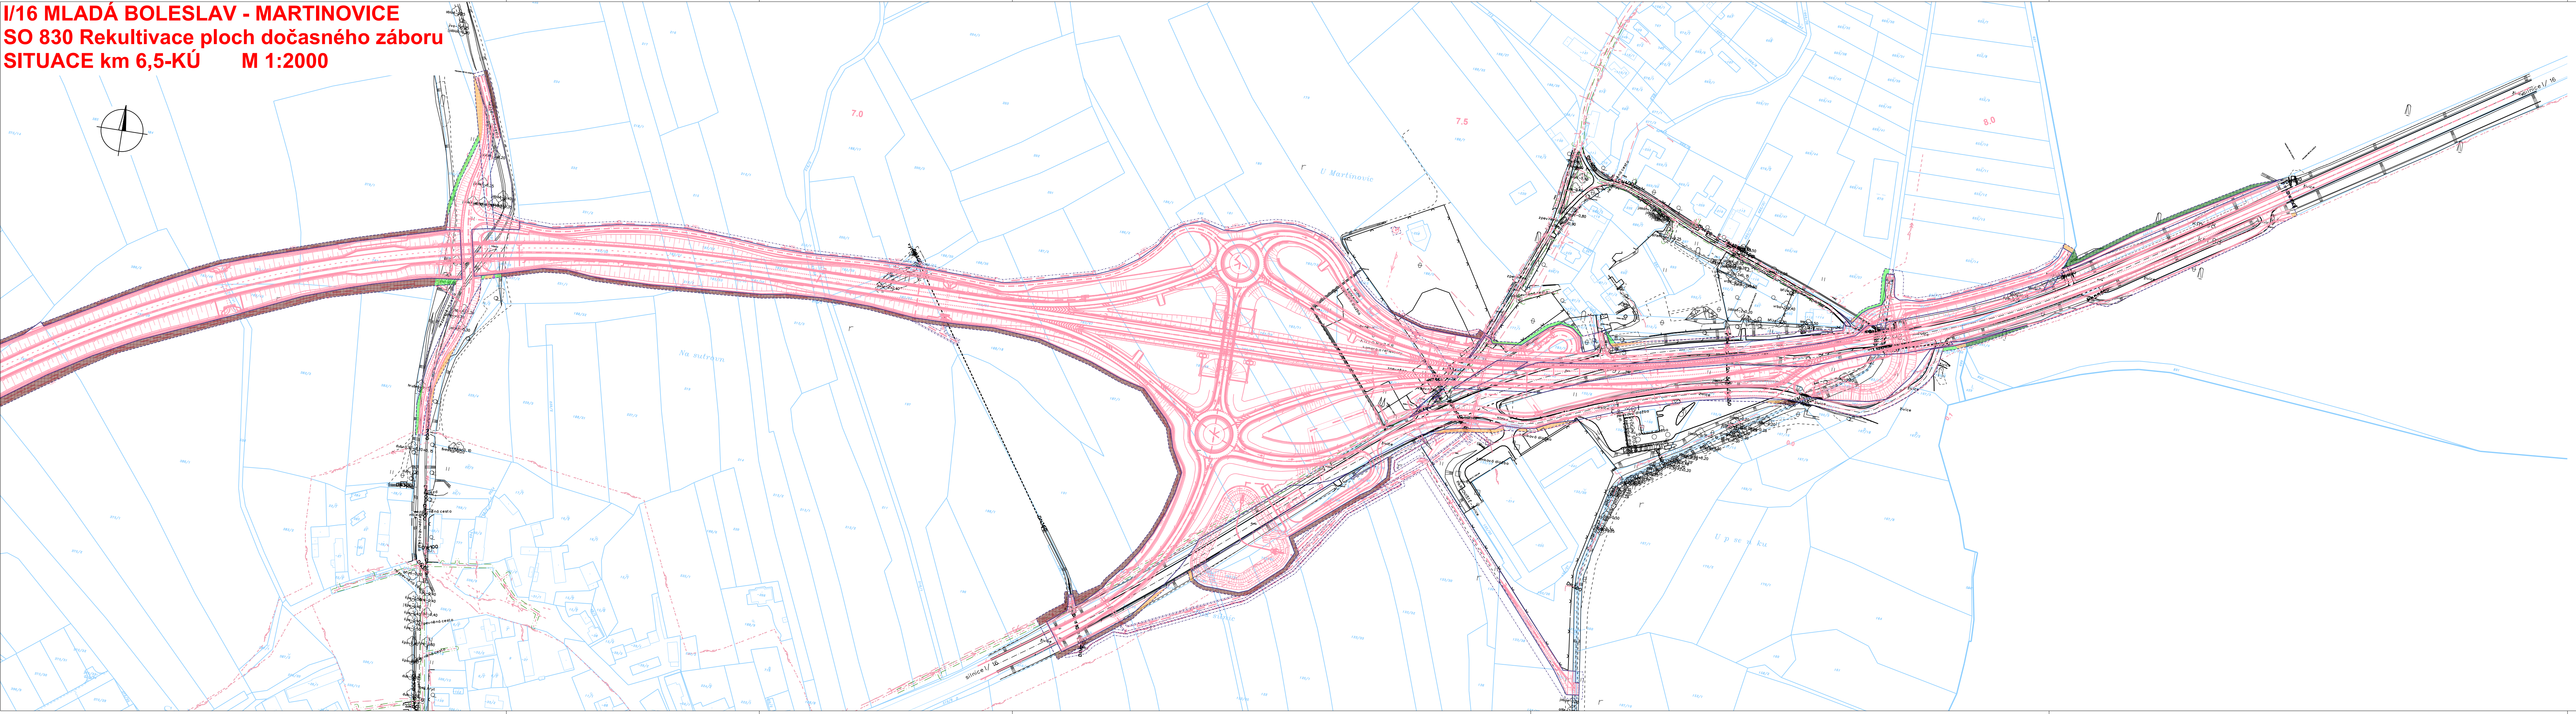

- LEGENDA
- REKULTIVACE PUPFL
 - REKULTIVACE ZPF - ORNÁ PŮDA
 - REKULTIVACE ZPF - TTP
 - REKULTIVACE ZPF - OSTATNÍ
 - REKULTIVACE OSTATNÍCH PLOCH
 - TRVALÝ ZÁBOR
 - DOČASNÝ ZÁBOR NAD 1 ROK

Souřadnicový systém: S-JTSK
Výškový systém: Bpv

SO 830 Rekultivace ploch dočasného záboru

Objednatel:



**ŘEDITELSTVÍ
SILNIC
A DÁLNIC**

Ředitelství silnic a dálnic s. p.
Čerčanská 2023/12, Krč, 140 00 Praha 4

Zhotovitel:	 Valbek	Valbek, spol. s r.o. Vaňurova 505/17 460 07 Liberec 3	HIP:	ING. T. KLIMENT
-------------	--	--	------	-----------------

 Valbek	Vypracoval	ING. Š. SOKOLÁŘOVÁ	<i>JSŠ</i>	Zak. číslo	21-L113-001	
	Zodp. projektant	ING. Š. SOKOLÁŘOVÁ	<i>JSŠ</i>	Datum	02/2025	
	Tech. kontrola	ING. K. TUŠEROVÁ	<i>TuŠ</i>	Stupeň	PDPS	
	Akce			Počet formátů	6 x A4	
I/16 MLADÁ BOLESLAV - MARTINOVICE					Měřítko	1 : 2000
					Č. přílohy	Paré
Zhotovitel:	Příloha				6	
Valbek, spol. s r.o. Vaňurova 505/17 460 07 Liberec 3	SITUACE km 6,5-KÚ					