


SO 860 - OPLOCENÍ
SITUACE č.1, km 0,000 - km 2,300, M 1 : 2 000

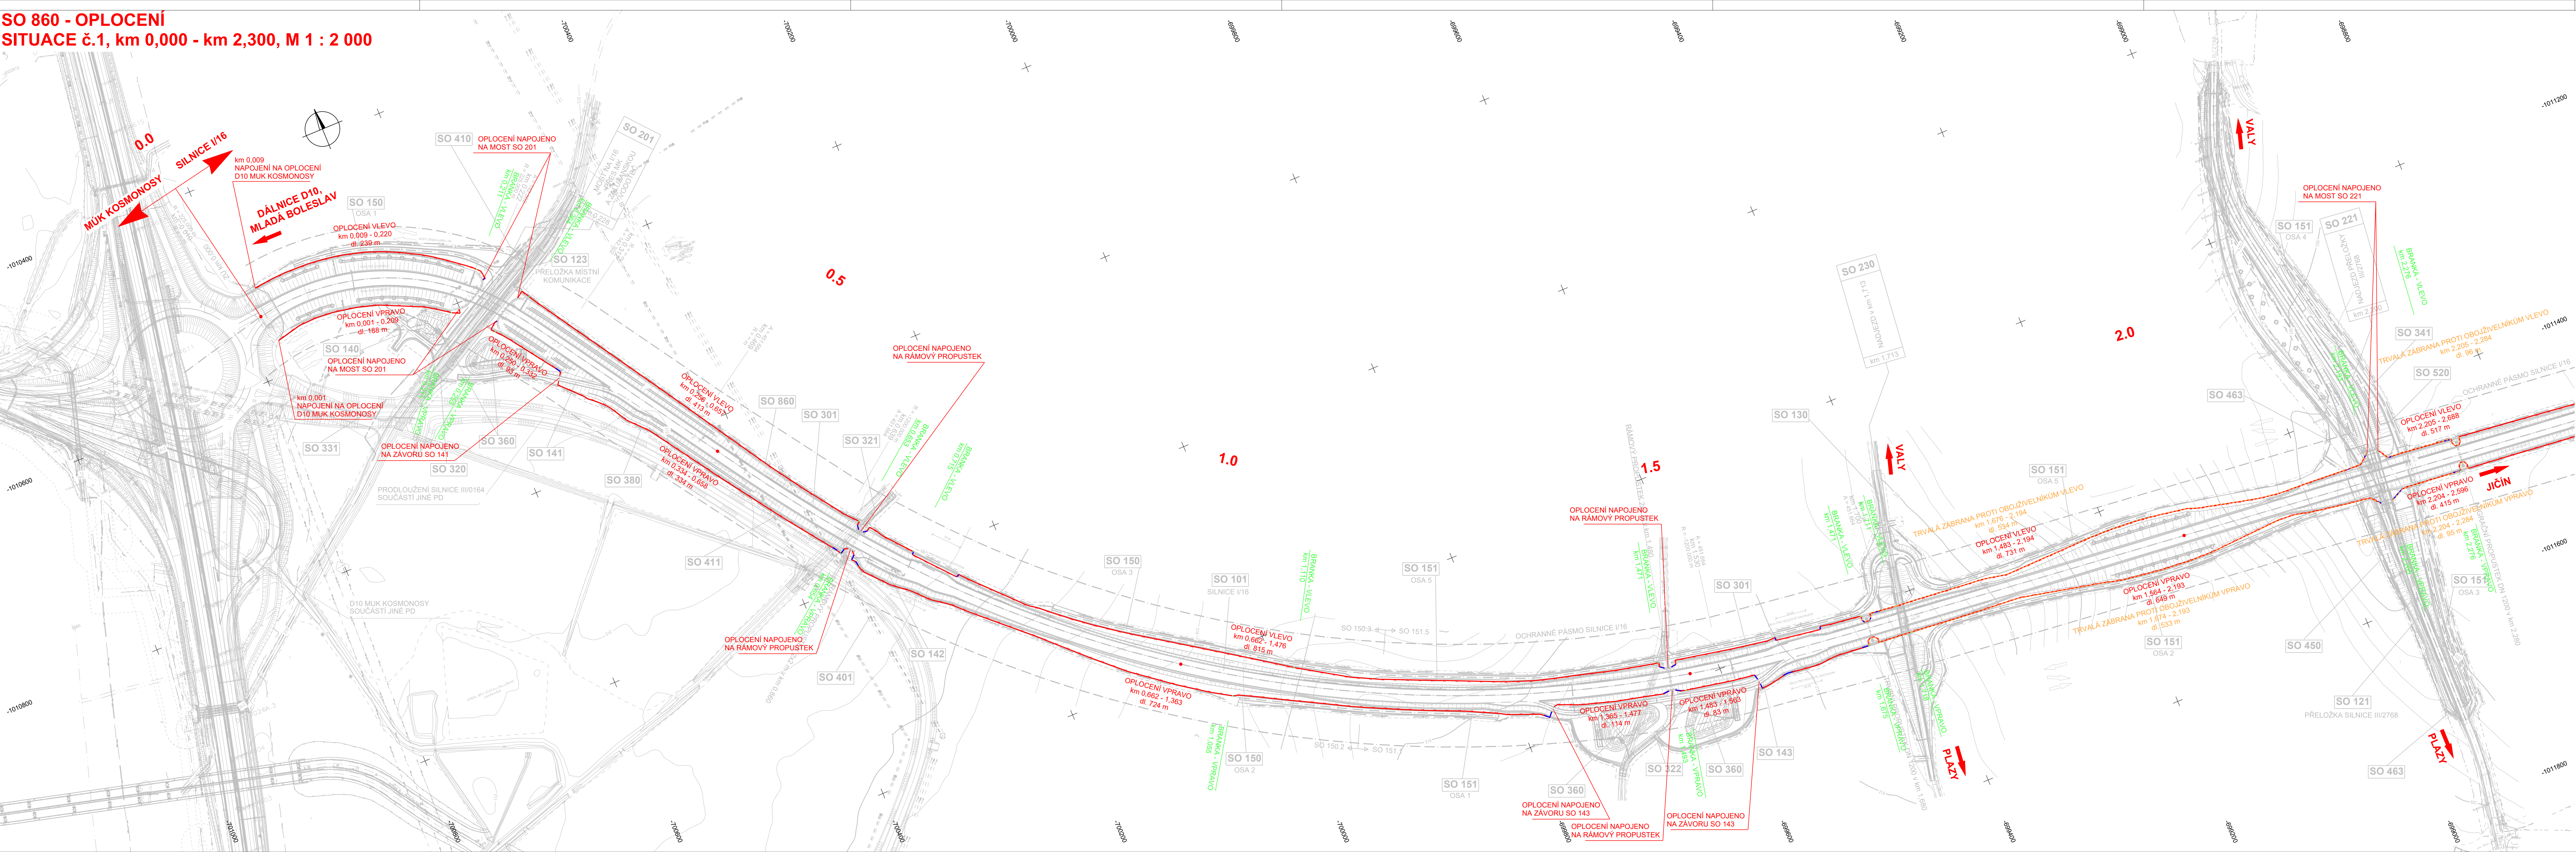

LEGENDA:

HRANY

- OPLOCENÍ
- JINÁ ROZTEČ NEŽ 4m
- BRANKY
- TRVALÁ ZÁBRANA PROTI OBOJÍVELNÍKŮM

Souřadnicový systém: S-JTSK
Výškový systém: Bpv

SO 860 Oplocení

Objednatel:



Ředitelství silnic a dálnic

Ředitelství silnic a dálnic s. p.

Čerčanská 2023/12, Křt, 140 00 Praha 4

Zhotovitel:



Valbek

Valbek, spol. s r.o.

Vaňurova 505/17
460 07 Liberec 3

	Vypracoval	P. MATYS	Zak. číslo	21-LH3-001
	Zodp. projektant	ING. T. KLIMENT	Datum	02 / 2025
	Tech. kontrola	ING. M. HANŽL	Stupeň	PDPS
	Akce	I/16 MLADÁ BOLESLAV - MARTINOVICE		Počet formátů
Zhotovitel: Ing. apl. Jiří B. Jurova 505/17 07 Liberec 3	Příloha	SITUACE č.1, km 0,000 - km 2,300	Měřítko	1 : 2 000
			Č. přílohy	Paré
			2.1	