


SO 860 - OPLOCENÍ
SITUACE č.2, km 2,300 - km 5,300, M 1 : 2 000



LEGENDA:

HRANY

- OPLOCENÍ
- JINÁ ROZTEČ NEŽ 4m
- BRANKY
- TRVALÁ ZÁBRANA PROTI OBOUJZVNÍKŮM

Souřadnicový systém: S-JTSK
Výškový systém: Bpv

SO 860 Oplocení

Objednatel:

**ŘEDITELSTVÍ
SILNIC
A DÁLNIC**

Ředitelství silnic a dálnic s. p.
Čerčanská 2023/12, Krč, 140 00 Praha 4

Zhotovitel:

Valbek, spol. s r.o.
Vaňurova 505/17
460 07 Liberec 3

	Vypracoval	P. MATYS	Zak. číslo	21-L13-001	
	Zodp. projektant	ING. T. KLIMENT	Datum	02 / 2025	
	Tech. kontrola	ING. M. HANŽL	Stupeň	PDP8	
	Akce	I/16 MLADÁ BOLESLAV - MARTINOVICE			
Zhotovitel: Valbek, spol. s r.o. Vaňurova 505/17 460 07 Liberec 3	Příloha SITUACE č.2, km 2,300 - km 5,300			Počet formátů	16 x A4
				Měřítko	1 : 2 000
				Č. přílohy	Pare
				2.2	