



SO 860 - OPLOCENÍ
VZOROVÉ PŘÍČNÉ ŘEZY, M 1 : 25, 1: 10

PODÉLNÝ ŘEZ - PLOTOVÉ POLE

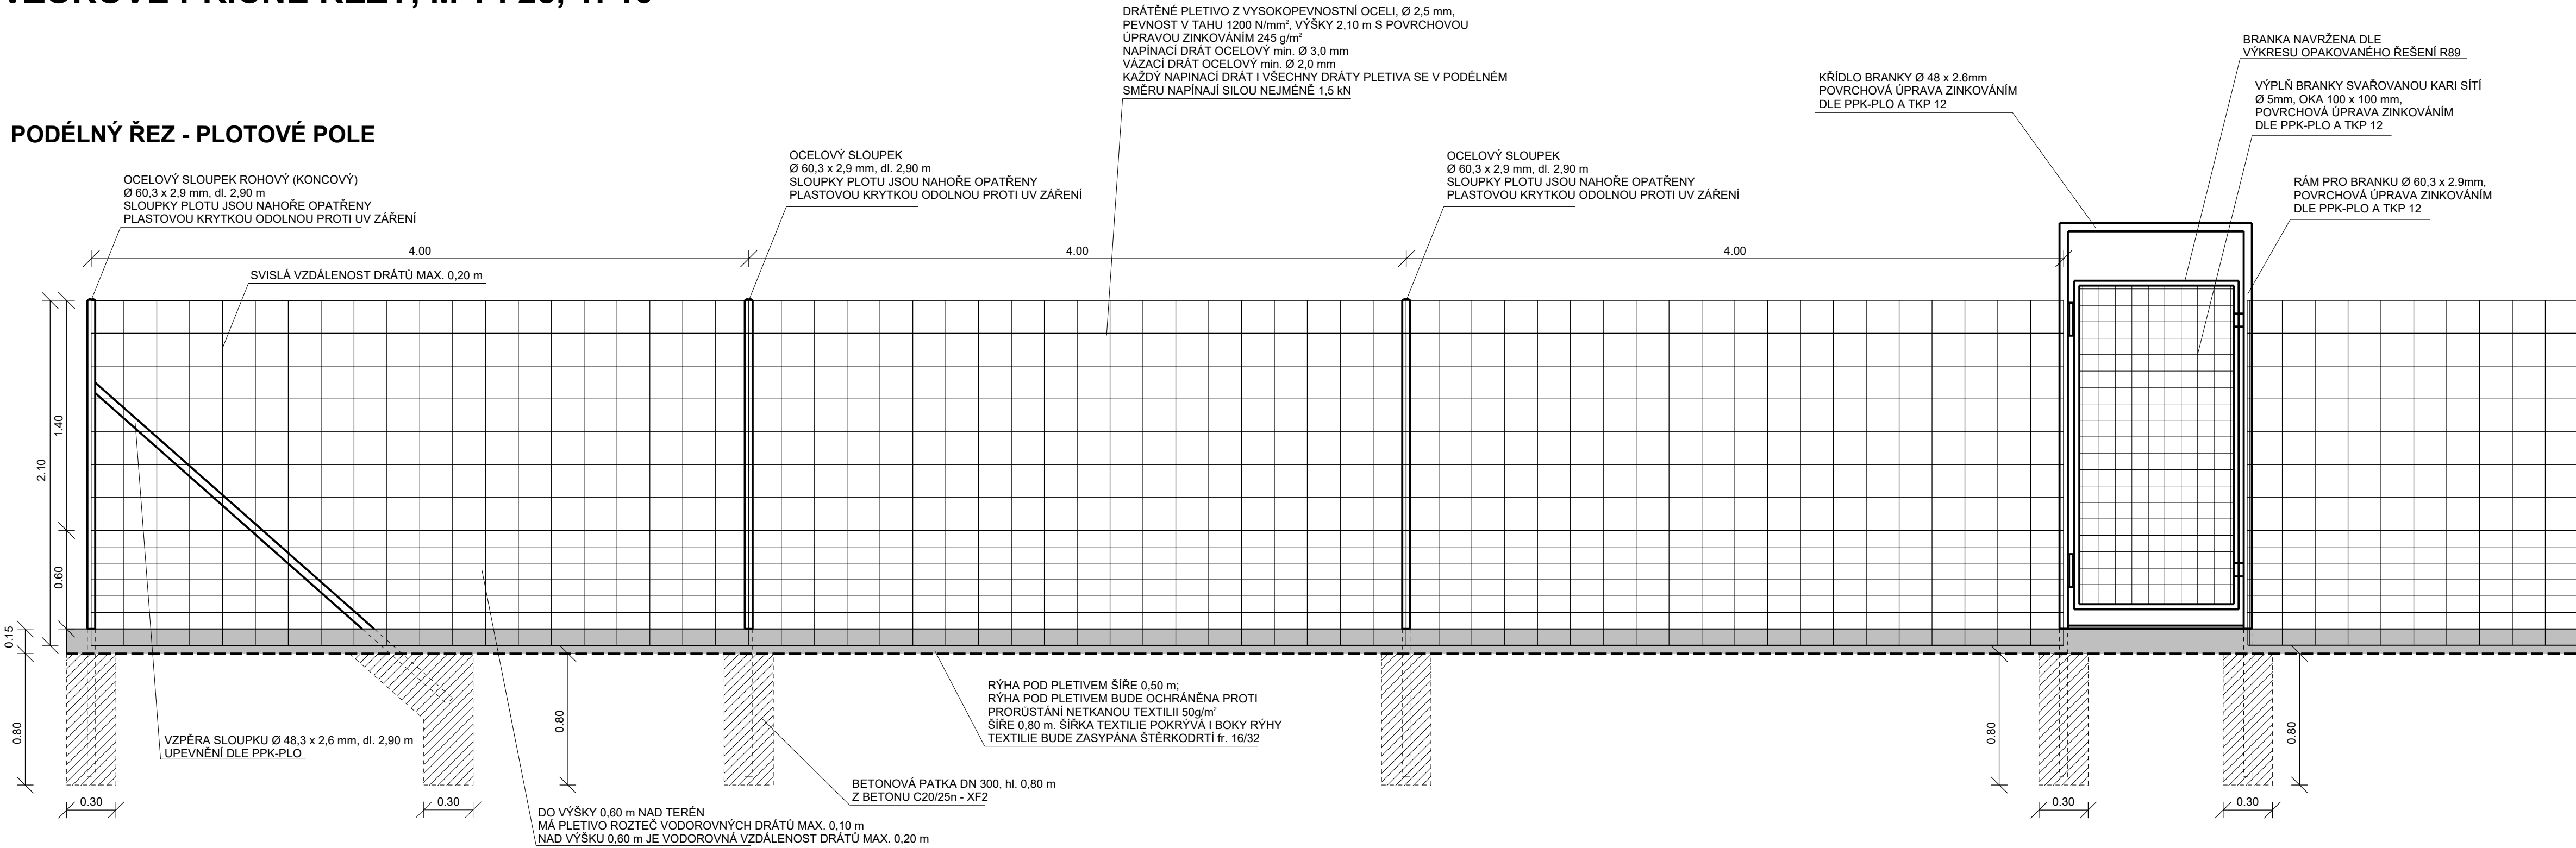

PŘÍČNÝ ŘEZ OPLOCENÍM

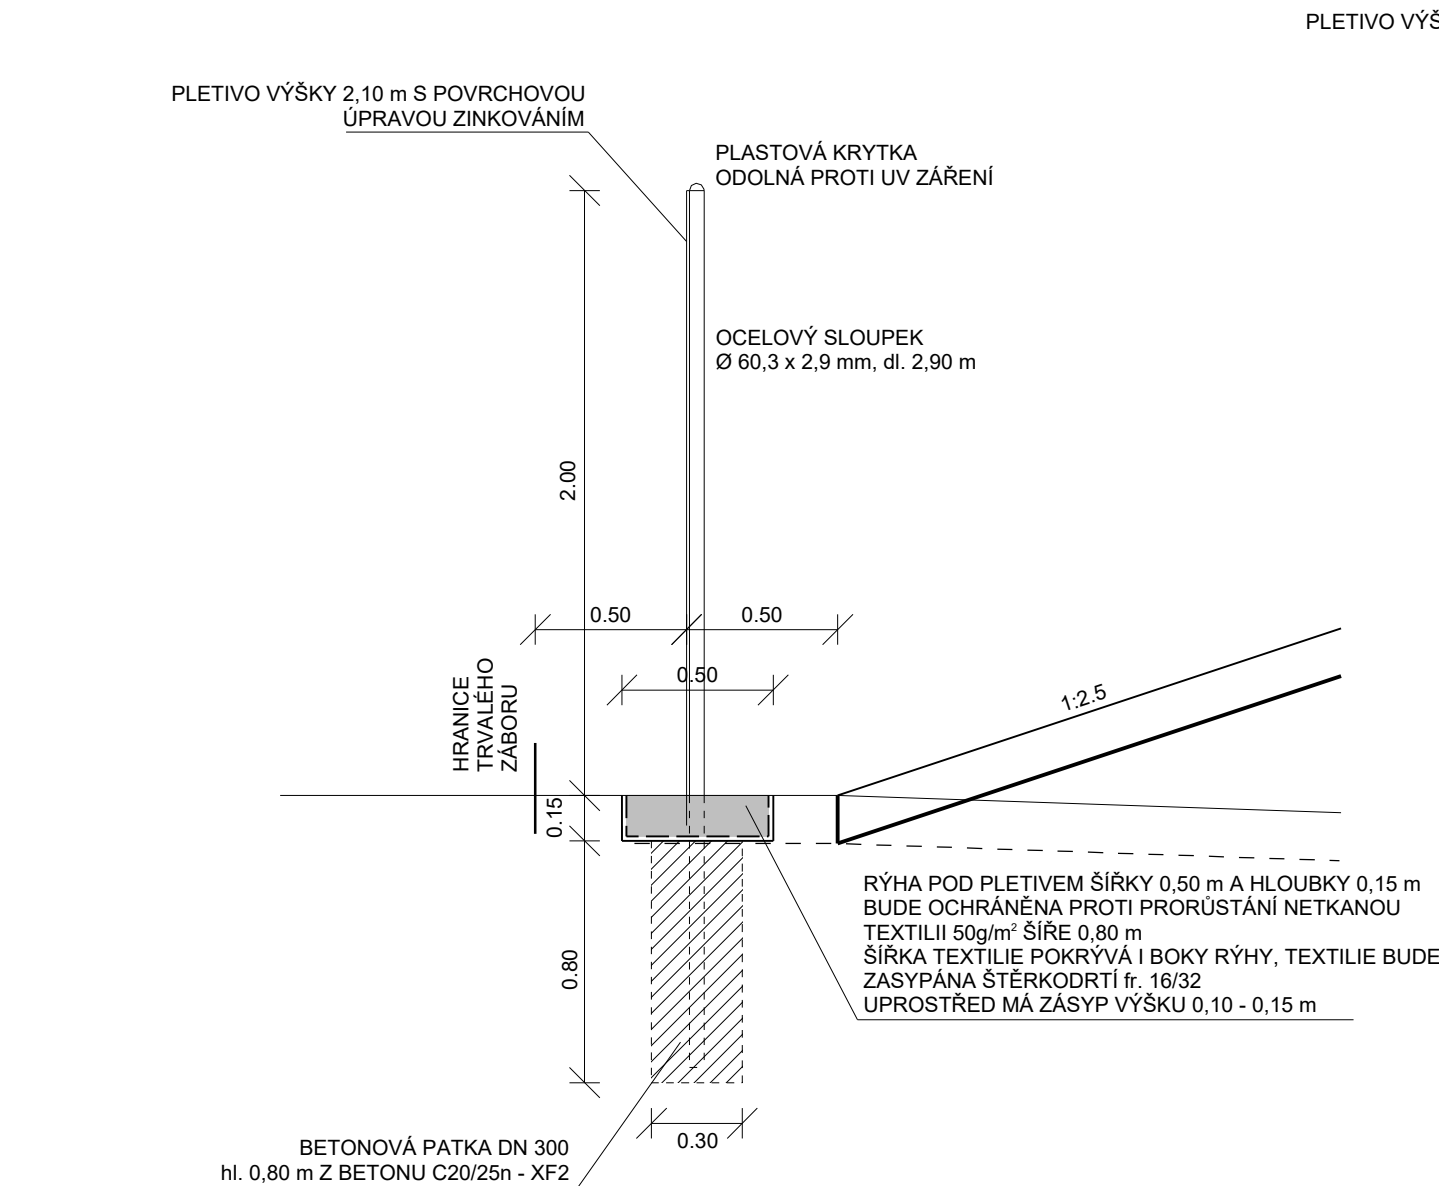

DETAIL č.1
BARIÉRA PROTI MIGRUJÍCÍM OBOJŽIVELNÍKŮM, M 1:10

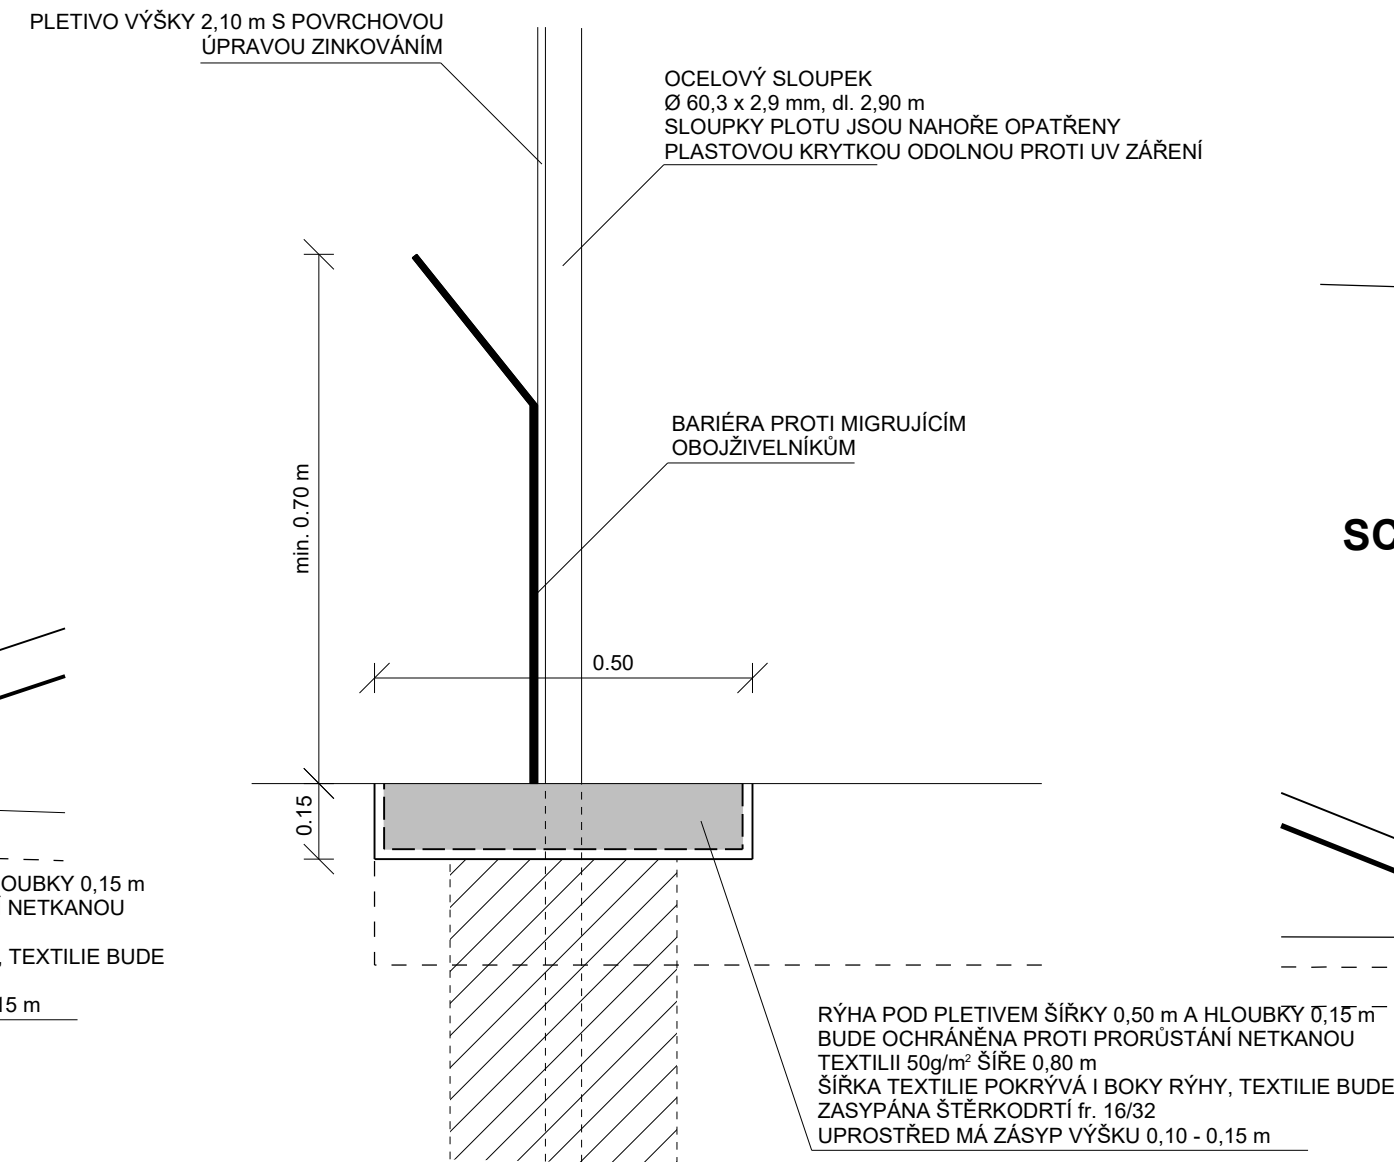


SCHÉMA UMÍSTĚNÍ OPLOCENÍ - ZÁŘEZ


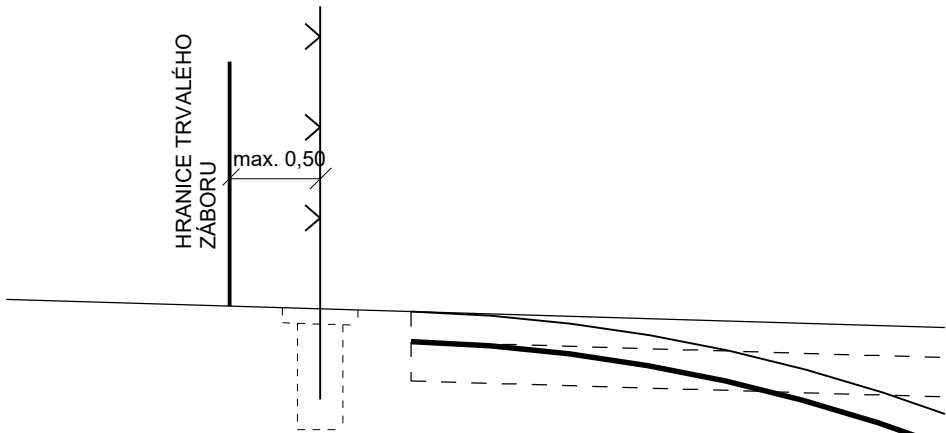


SCHÉMA UMÍSTĚNÍ OPLOCENÍ - NÁSYP

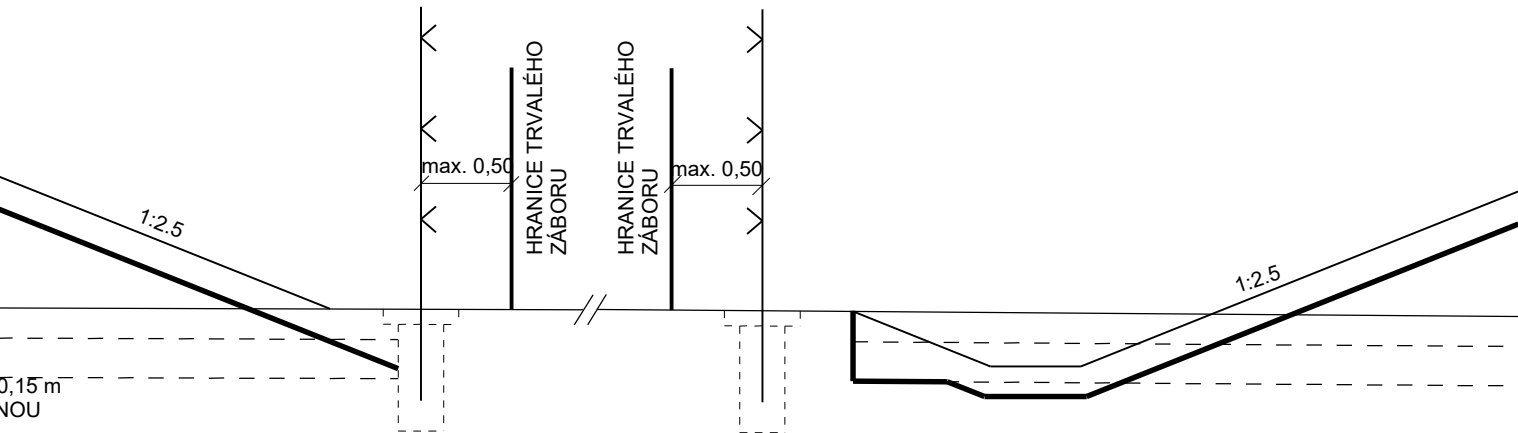

POZNÁMKY:

V MÍSTECH, KDE JE OPLOCENÍ OD HRANY KOMUNIKACE 5,00 m A MÉNĚ, DOPORUČUJEME OSADIT SLOUPKY VE VZDÁLENOSTECH 3,00 m, KVŮLI ZIMNÍ ÚDRŽBĚ (SHRNUTÝ SNÍH Z CELE ŠÍŘE KOMUNIKACE).

VŠECHNY OCELOVÉ PRVKY MUSÍ BÝT ZINKOVÁNY PODLE ČSN EN ISO 1461 NEBO SYSTÉMEM III E DLE TKP 19B.

NAPÍNAČÍ DRÁT PLETIVA MUSÍ SPLŇOVAT POŽADOVANY PPK-PLO.

DÉLKA POLÍ PLOTU JE 4,0 m, V ODŮVODNĚNÝCH PŘÍPADECH MAX. 6,0 m.

UMÍSTĚNÍ BRANEK BUDE V SOULADU S POŽADAVKY PPK-PLO.

V MÍSTĚ DELŠÍCH ROVNÝCH ÚSEKŮ BUDOU PO 25 m OSAZENY VZPĚRY KE SLOUPKŮM, VZPĚRY BUDOU OSAZENY I NA KONCI OPLOCENÍ A VE SMĚROVÝCH A VÝŠKOVÝCH LOMECH.

VEŠKERÉ PRVKY OPLOCENÍ MUSÍ BÝT V SOULADU S PPK-PLO A TKP 12.

BRANKA

OCELOVÁ BRANKA S POSUVNÝMI ZÁVĚSY
NAVRŽENA DLE VÝKRESU OPAKOVANÉHO ŘEŠENÍ R89

SO 860 Oplocení

Objednatel:



ŘEDITELSTVÍ
SILNIC
A DÁLNIC

Ředitelství silnic a dálnic s. p.
Čerčanská 2023/12, Krč, 140 00 Praha 4

Zhotovitel:



Valbek, spol. s r.o.
Vaňurova 505/17
460 07 Liberec 3



Vypracoval	P. MATYS	Zak. číslo	21-L113-001	
Zodp. projektant	ING. T. KLIMENT	Datum	02 / 2025	
Tech. kontrola	ING. M. HANŽL	Stupeň	PDPS	
Akce	I/16 MLADÁ BOLESLAV - MARTINOVICE		Počet formátů	8 x A4
Příloha	VZOROVÉ PŘÍČNÉ ŘEZY	Měřítko	1 : 25, 1 : 10	
		Č. přílohy	Paré	
		3		